
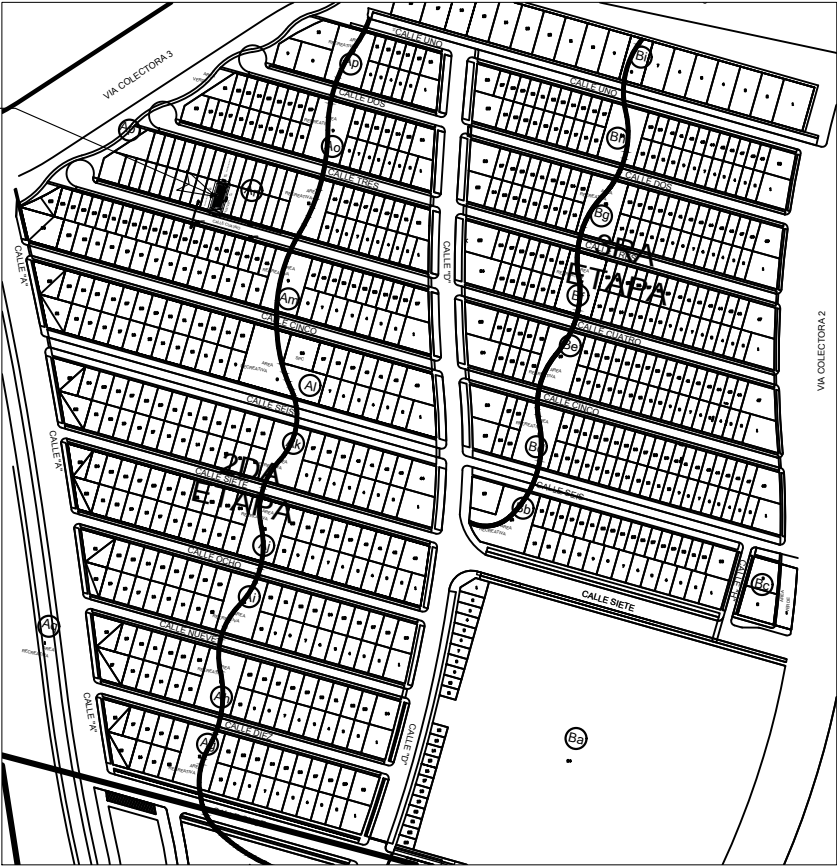


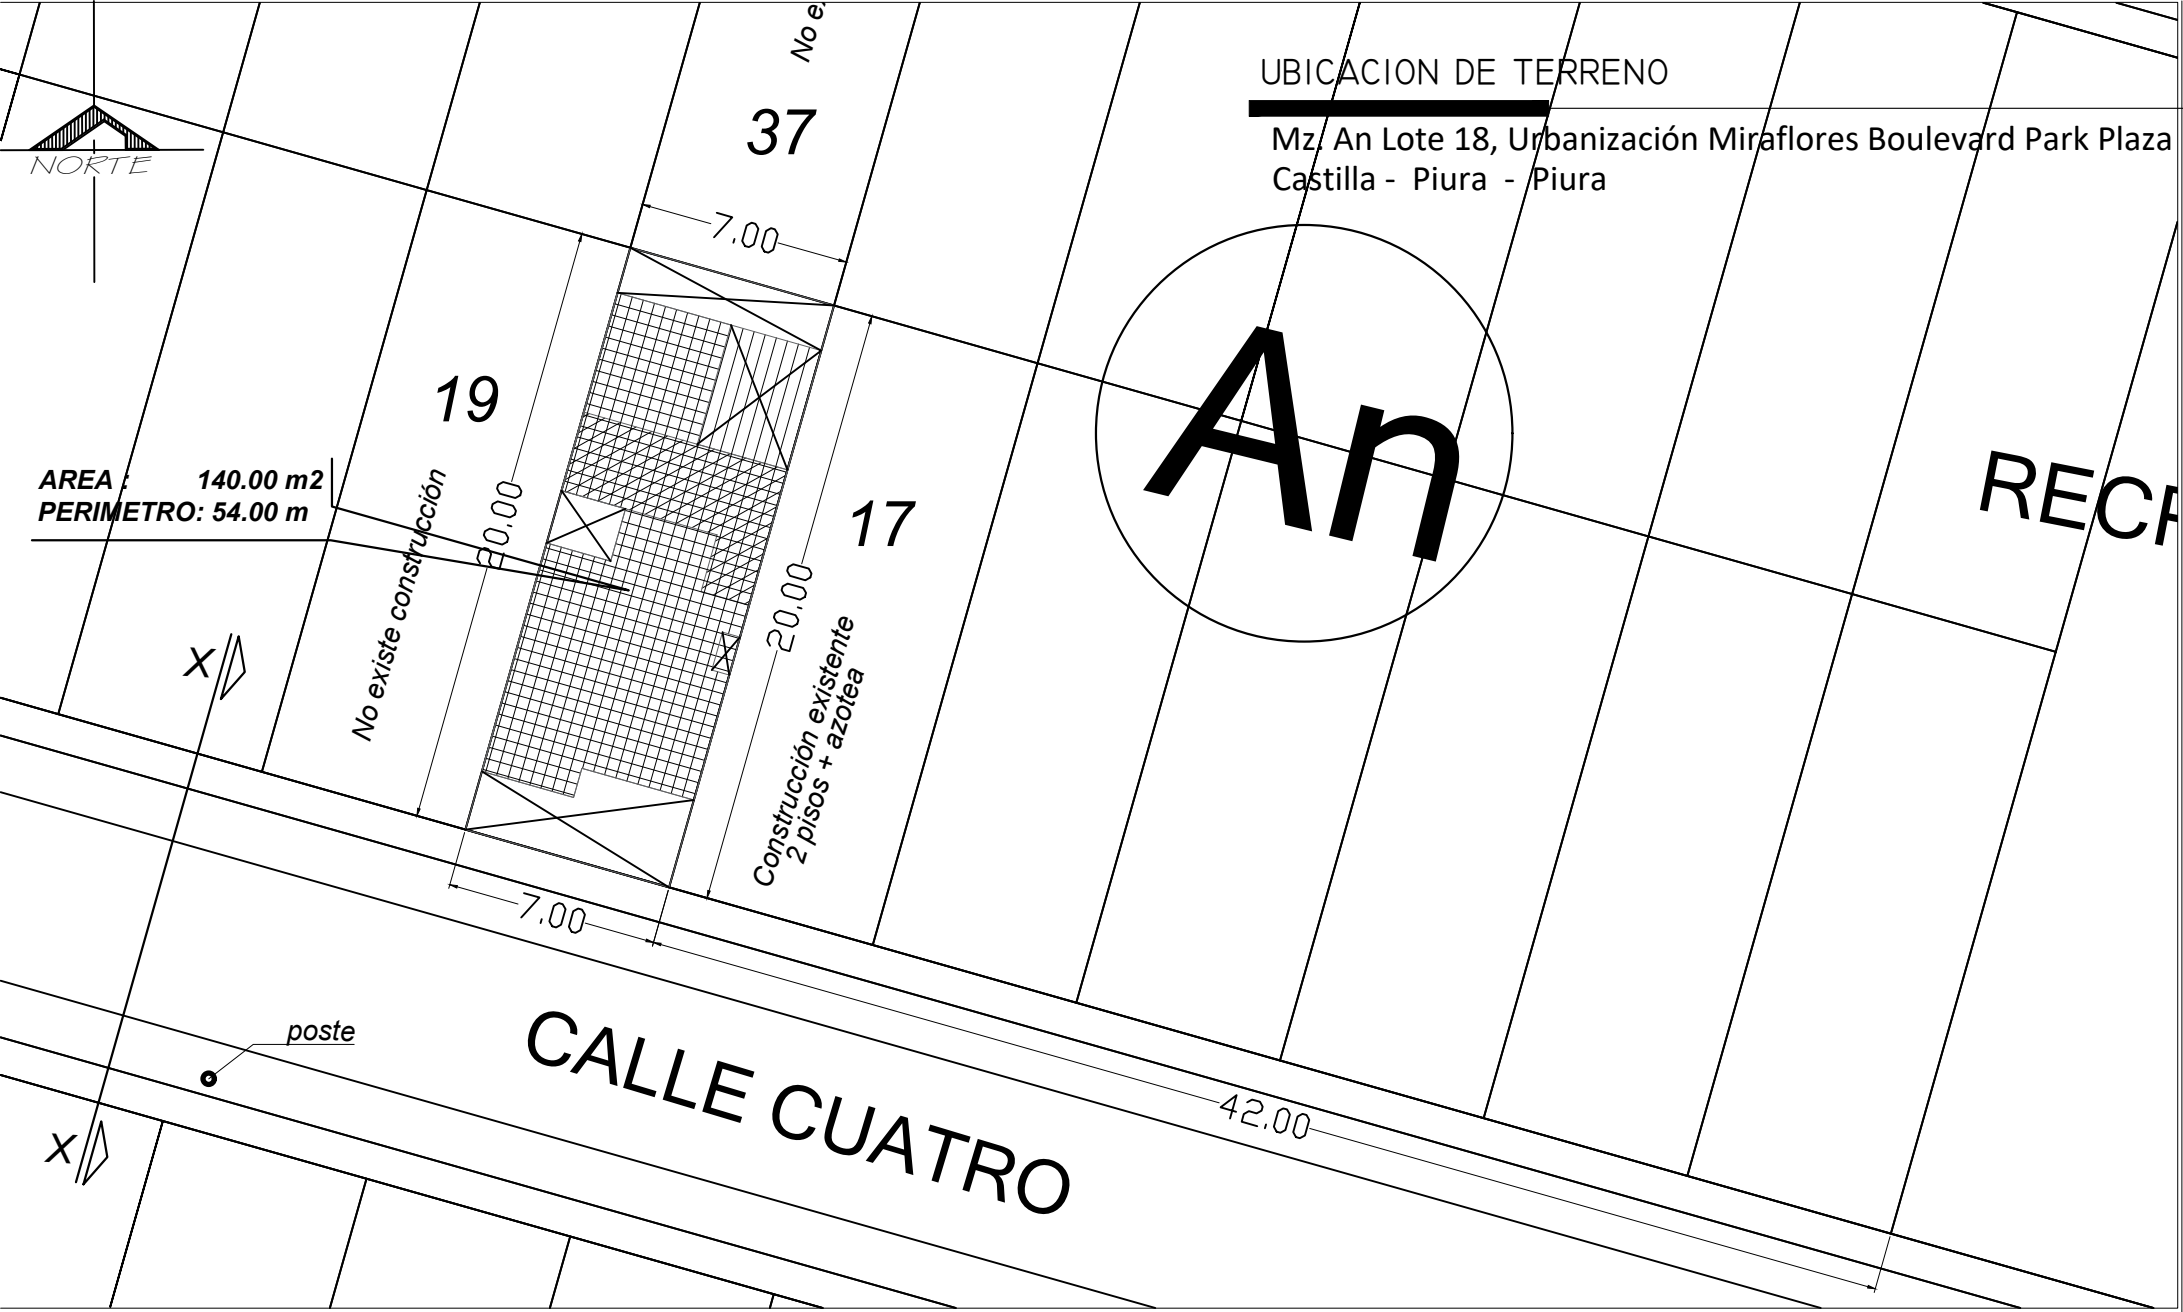

PLANO DE LOCALIZACION	ESCALA 1/5000
ZONIFICACIÓN:	R. D. M. - RESIDENCIAL DENSIDAD MEDIA
AREA DE ESTRUCTURACION URBANA:	-
DEPARTAMENTO:	PIURA
PROVINCIA:	PIURA
DISTRITO:	CASTILLA
URBANIZACION:	URB. MIRAFLORES BOULEVARD PARK PLAZA - SEGUNDA ETAPA
NOMBRE DE LA CALLE:	CALLE CUATRO
N° INMUEBLE:	S/N
MANZANA:	"AN"
LOTE:	18
SUB LOTE:	-

PROFESIONAL	PROPIEDAD :
	Sra. ROSSEMERY YANIRE FERNÁNDEZ ROJAS

PROYECTO


VIVIENDA UNIFAMILIAR

Mz. AN Lote 18, Urb. Miraflores Boulevard Park Plaza

Segunda Etapa , Castilla - Piura


NOMBRE DEL PLANO	UBICACIÓN Y LOCALIZACIÓN
DIBUJADO POR JLAY	ESCALA DE DIBUJO 1/250, 1/5000.
JULIO 2026	ID DE PLANO U.01

LEYENDA AREA TECHADA	
PRIMER PISO	
SEGUNDO PISO	
AZOTEA	

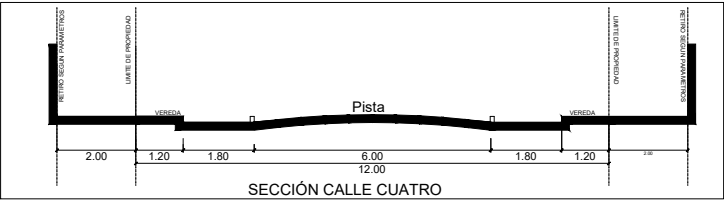

PLANO DE UBICACIÓN
ESCALA 1/250

CUADRO NORMATIVO			CUADRO DE ÁREAS (M2)							
PARÁMETROS		NORMATIVO	PROYECTO	PISOS	ÁREAS DECLARADAS					
					EXISTENTE	DEMOLICIÓN	NUEVA	AMP./REM.	PARCIAL	TOTAL
USOS		VIV. UNIFAMILIAR - MULTIF.	VIV. UNIFAMILIAR	PRIMER			102.20 M2			102.20 M2
DENSIDAD NETA		1300 HAB/HA	571.43 HAB/HA	SEGUNDO			102.20 M2			102.20 M2
COEF. DE EDIFICACIÓN		2.40	1.65	AZOTEA			26.00 M2			26.00 M2
% ÁREA LIBRE		27%	27%							
ALTURA MÁXIMA		03 PISOS+AZOTEA	02 PISOS + AZOTEA							
	FRONTAL	2.00 ML.	2.00 ML.							
RETIRO	LATERAL	-----	-----							
	POSTERIOR	-----	-----	AREA TECHADA						230.40 M2
ALINEAMIENTO FACHADA		RESPETAR SECC. VIAL	RESPETA EL EXISTENTE	AREA LIBRE						37.80 M2
Nº ESTACIONAMIENTO		01 CADA 02 VIVIENDAS	01 ESTACIONAMIENTO	AREA DEL TERRENO						140.00 M2

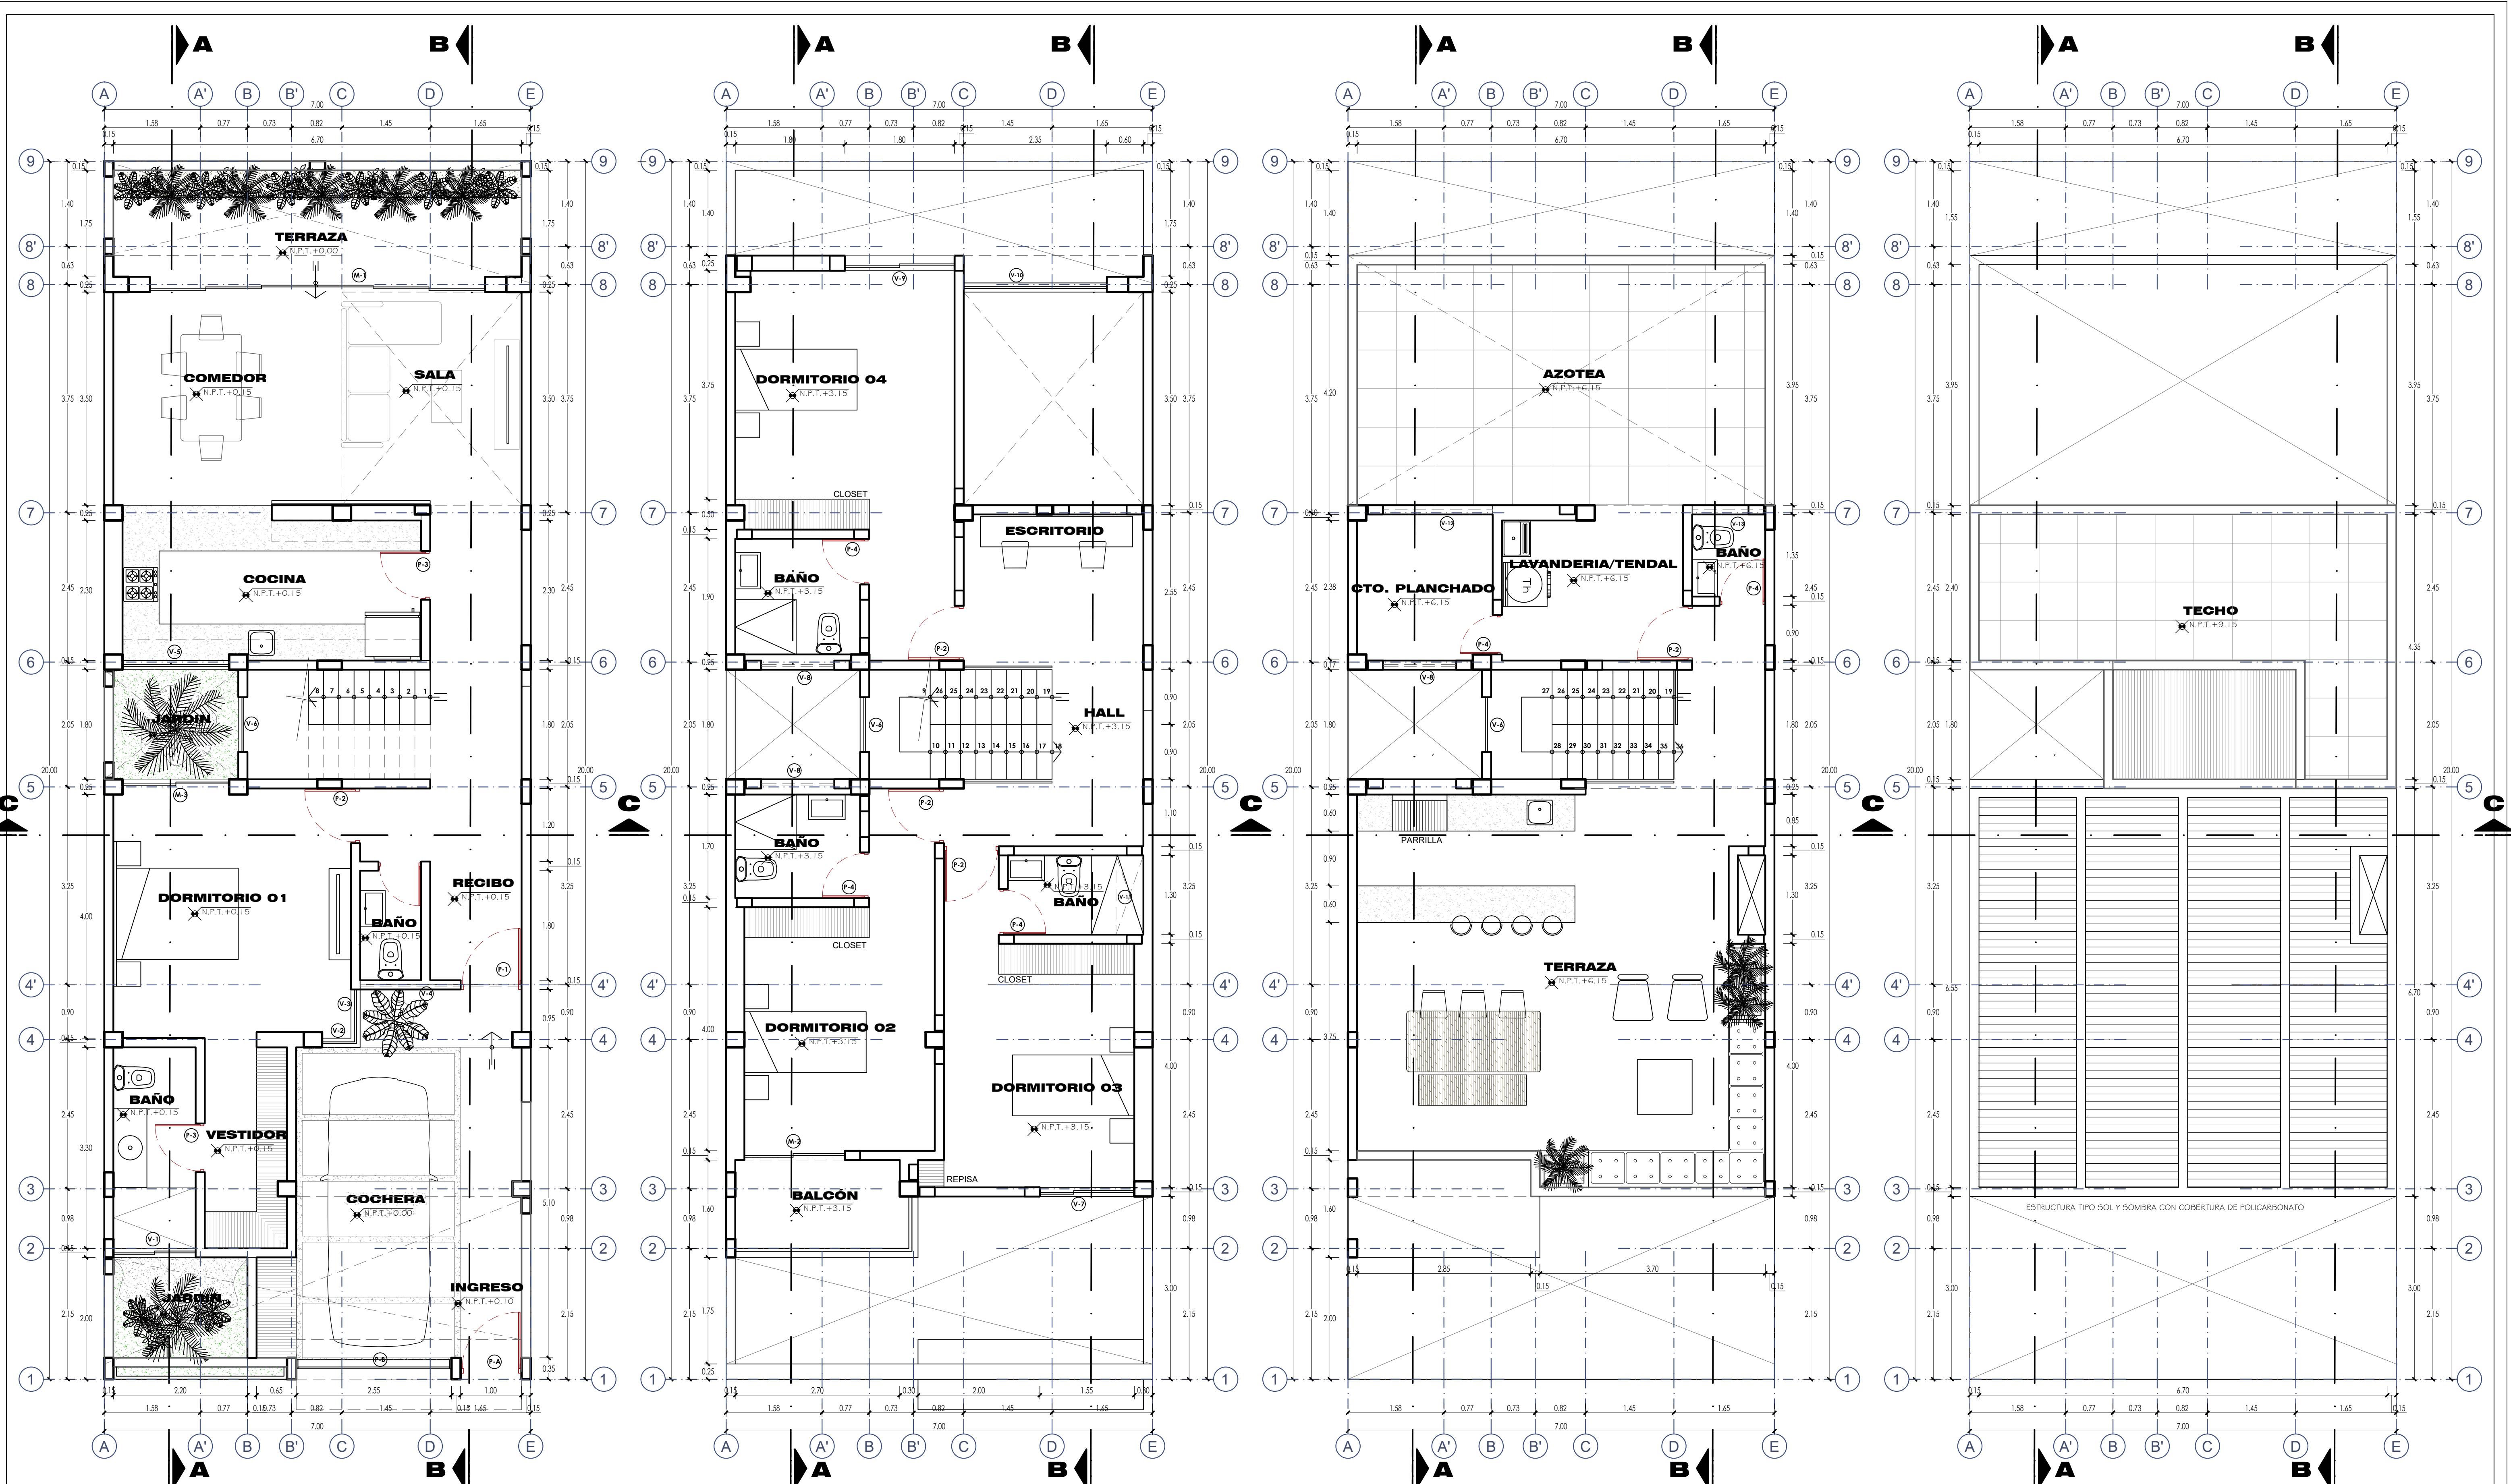

PLANTA PRIMER PISO
Esc: 1/50

PLANTA SEGUNDO PISO
Esc: 1/50


PLANTA AZOTEA
Esc: 1/50

PLANTA TECHO
Esc: 1/50

PROYECTO: VIVIENDA UNIFAMILIAR	UBICACIÓN : URB. MIRAFLORES BOULEVARD PARK PLAZA Mz. AN - Lote 18 - II ETAPA - CASTILLA PROPIETARIO: Sra. ROSSEMERY YANIRE FERNÁNDEZ ROJAS DNI: 80366589	DIBUJO : JLAY RESPONSABLE : ARQ. RENZO IZQUIERDO ESCALA : 1 / 50 FECHA : JULIO 2026	TITULO DE LÁMINA: ARQUITECTURA PLANTAS DE DISTRIBUCIÓN 1er, 2do PISO, AZOTEA Y TECHO	N° LÁMINA: A-01



SECCIÓN A - A
Esc: 1/50

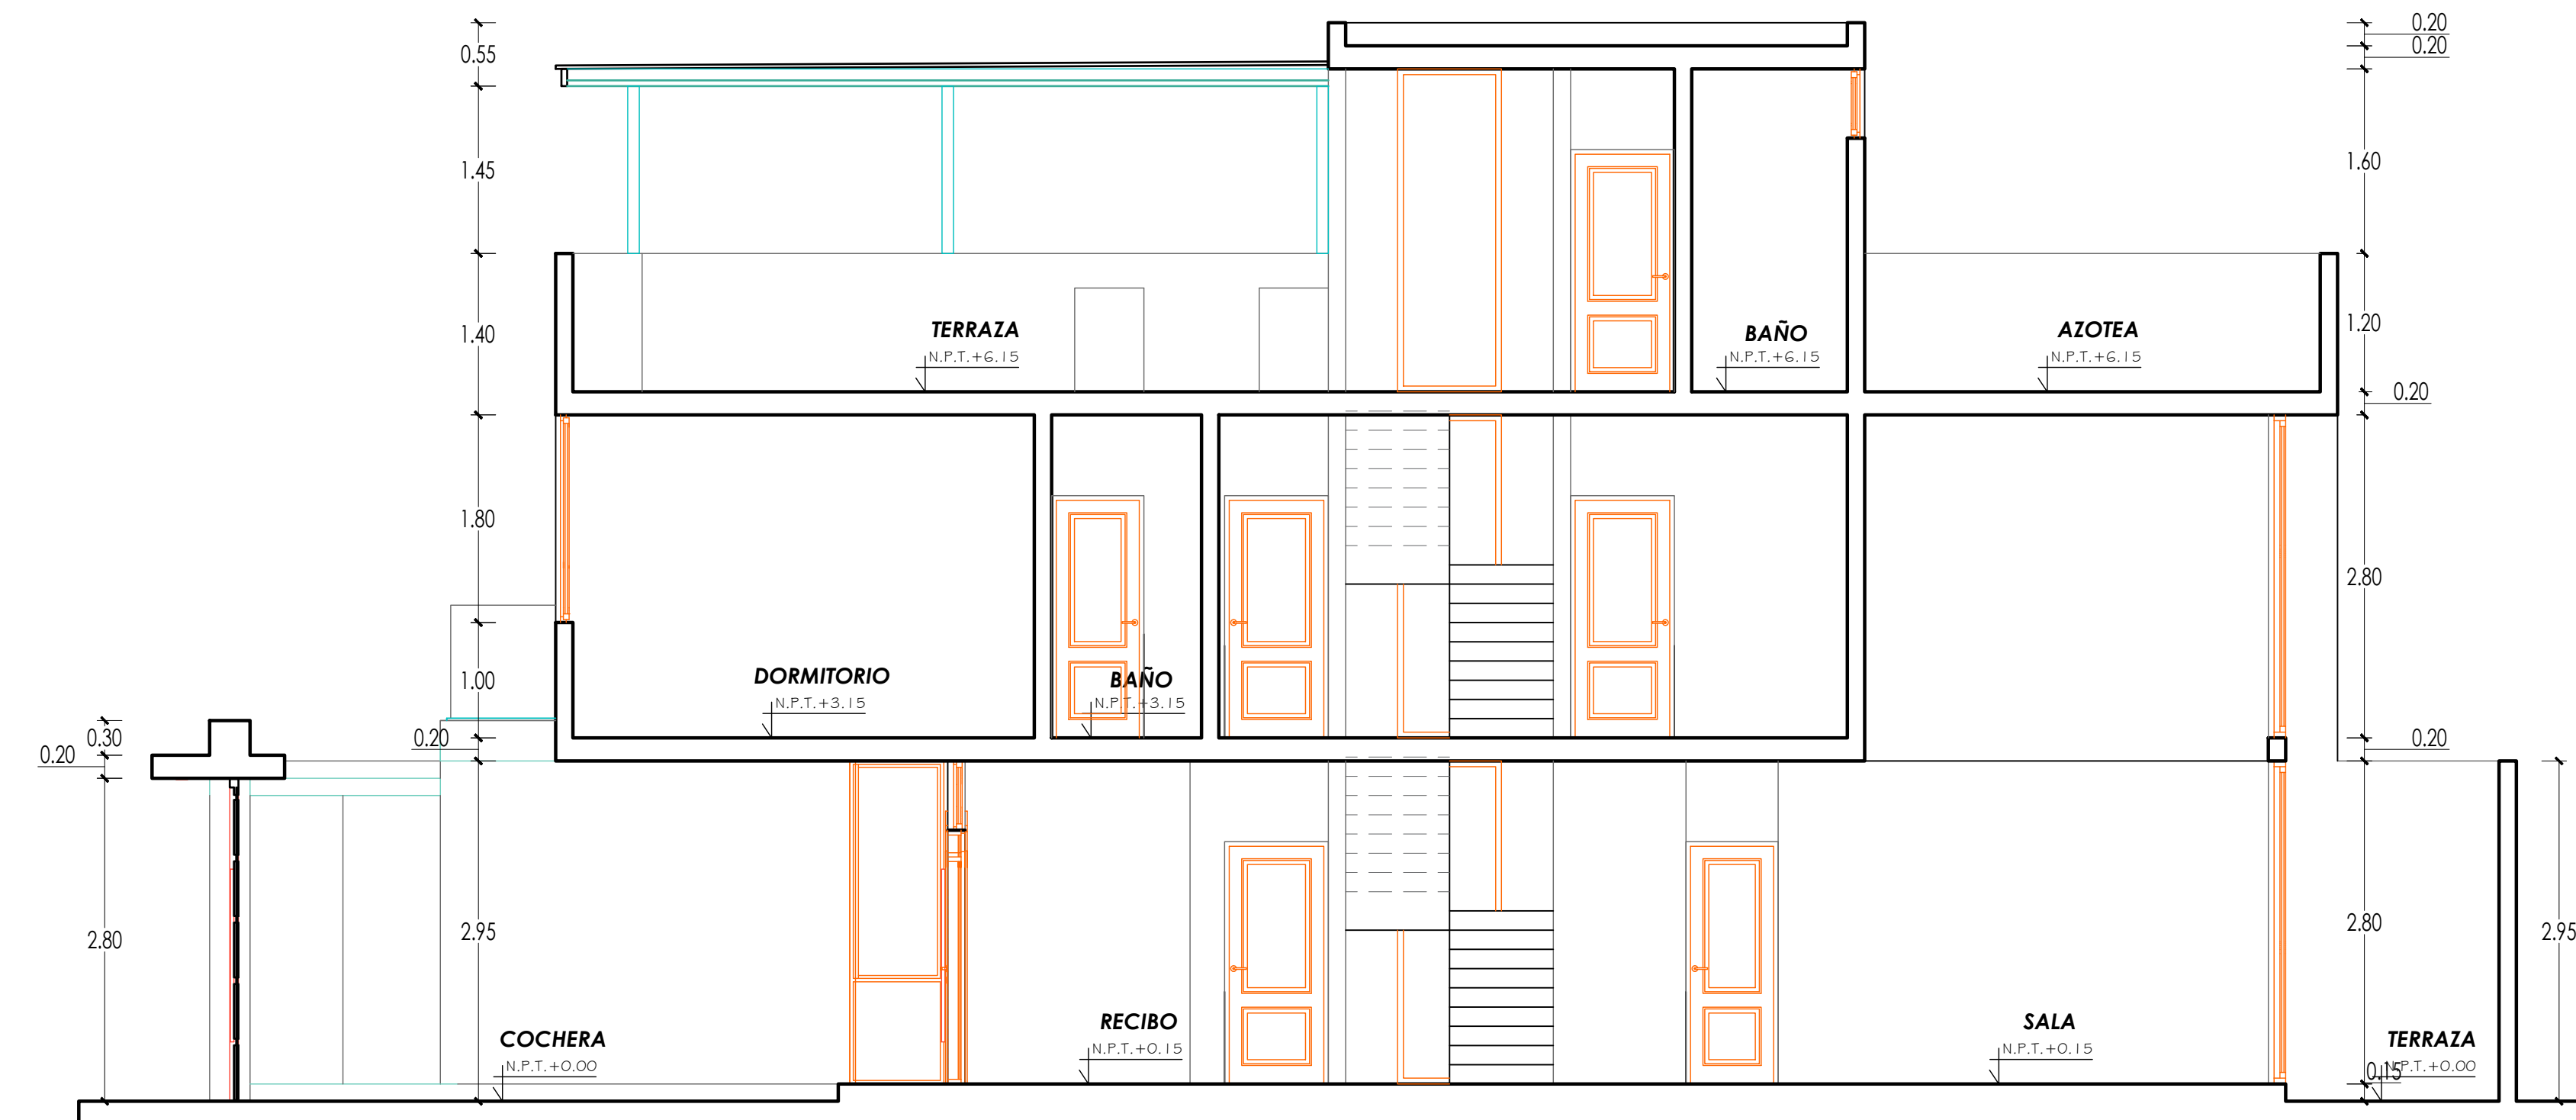

SECCIÓN B - B
Esc: 1/50

CUADRO DE VANOS - PUERTAS


TIPO	ANCHO	ALTO	ALFEIZER	AMBIENTE
P-A	1.00	2.80	----	INGRESO EXTERIOR PRINCIPAL
P-B	2.55	2.65	----	COCHERA
P-1	1.00	2.10	----	INGRESO INTERIOR PRINCIPAL
P-2	0.90	2.10	----	INGRESO DORMITORIOS
P-3	0.80	2.10	----	BAÑO
P-4	0.75	2.10	----	BAÑO

CUADRO DE VANOS - MAMPARA

TIPO	ANCHO	ALTO	ALFEIZER	AMBIENTE
M-1	5.50	2.60	----	SALA - COMEDOR
M-2	1.65	2.80	----	DORMITORIO 03
M-3	2.80	1.75	----	DORMITORIO 01

CUADRO DE VANOS - VENTANAS


TIPO	ANCHO	ALTO	ALFEIZER	AMBIENTE
V-1	2.65	1.35	----	BAÑO
V-2	0.65	2.80	----	DORMITORIO 01
V-3	0.95	2.80	----	BAÑO
V-4	0.60	2.65	2.20	BAÑO / RECIBO
V-5	1.80	1.75	1.00	COCHERA
V-6	2.80	0.90	----	ESCALERA
V-7	1.80	1.55	1.00	DORMITORIO 03
V-8	0.60	1.20	2.20	BAÑO
V-9	1.80	1.80	1.00	DORMITORIO 04
V-10	1.80	2.35	1.00	SALA
V-11	0.60	1.30	2.20	BAÑO
V-12	0.60	1.80	2.20	CTO. PLANCHAR
V-13	0.60	1.20	2.20	BAÑO

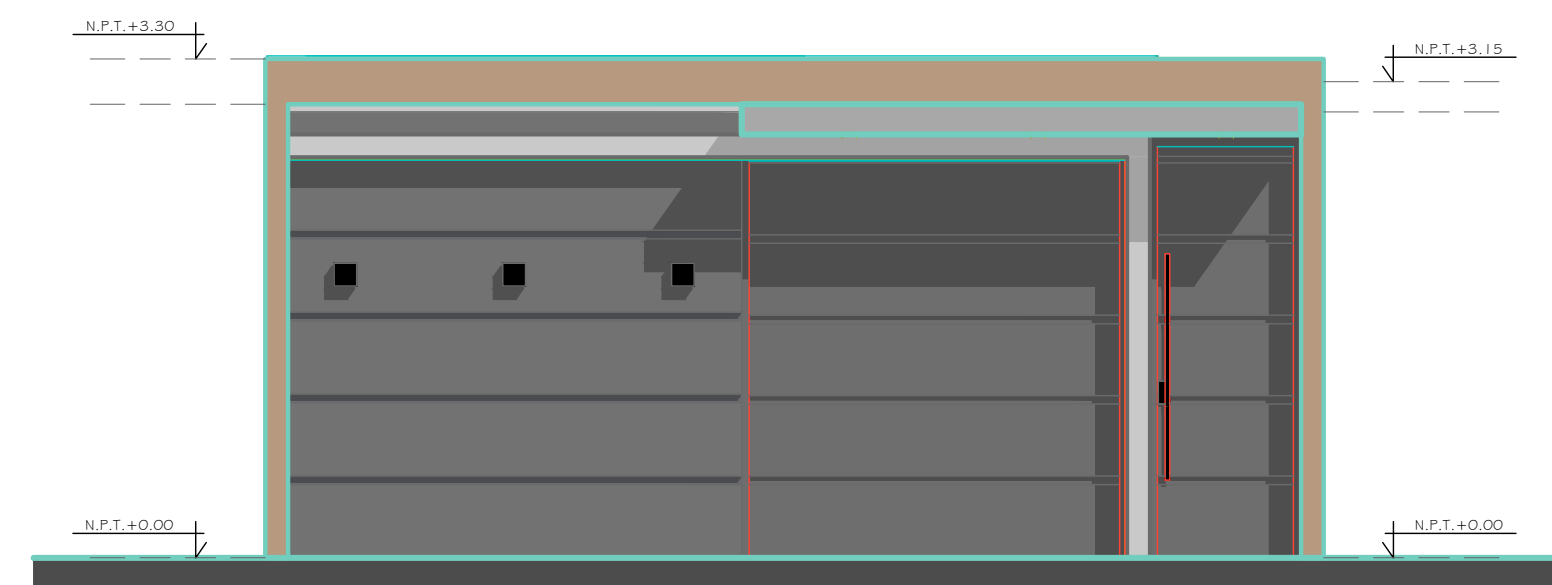

ELEVACIÓN CERCO
Esc: 1/50




ELEVACIÓN PRINCIPAL
Esc: 1/50

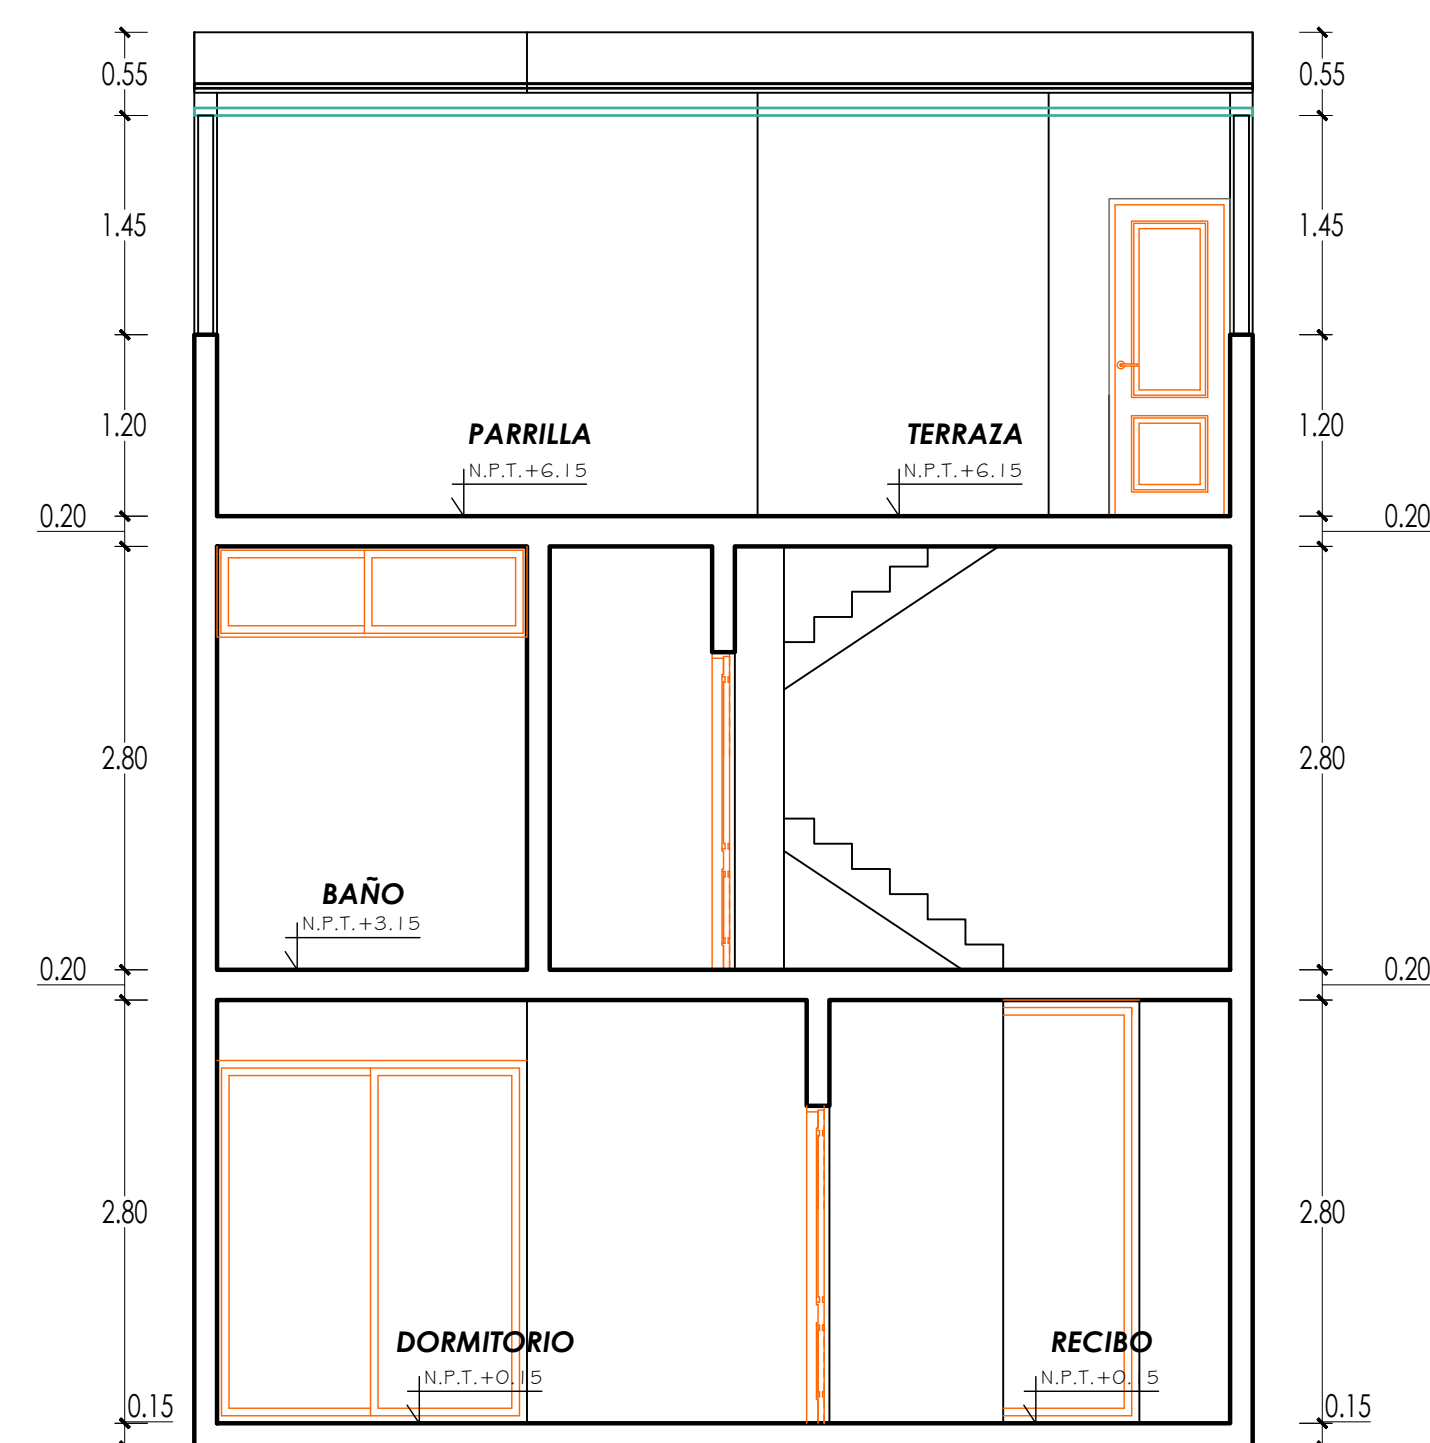



SECCIÓN C - C
Esc: 1/50

PROYECTO: VIVIENDA UNIFAMILIAR	UBICACIÓN :	DIBUJO : JLAY	TÍTULO DE LÁMINA: ARQUITECTURA SECCIONES Y ELEVACIONES	N° LÁMINA: A-02
	URB. MIRAFLORES BOULEVARD PARK PLAZA Mz. AN - Lote 18 - II ETAPA - CASTILLA	RESPONSABLE : ARQ. RENZO IZQUIERDO		
	PROPIETARIO:	ESCALA : 1 / 50		
	Sra. ROSSEMERY YANIRE FERNÁNDEZ ROJAS DNI: 80366589	FECHA : JULIO 2026		

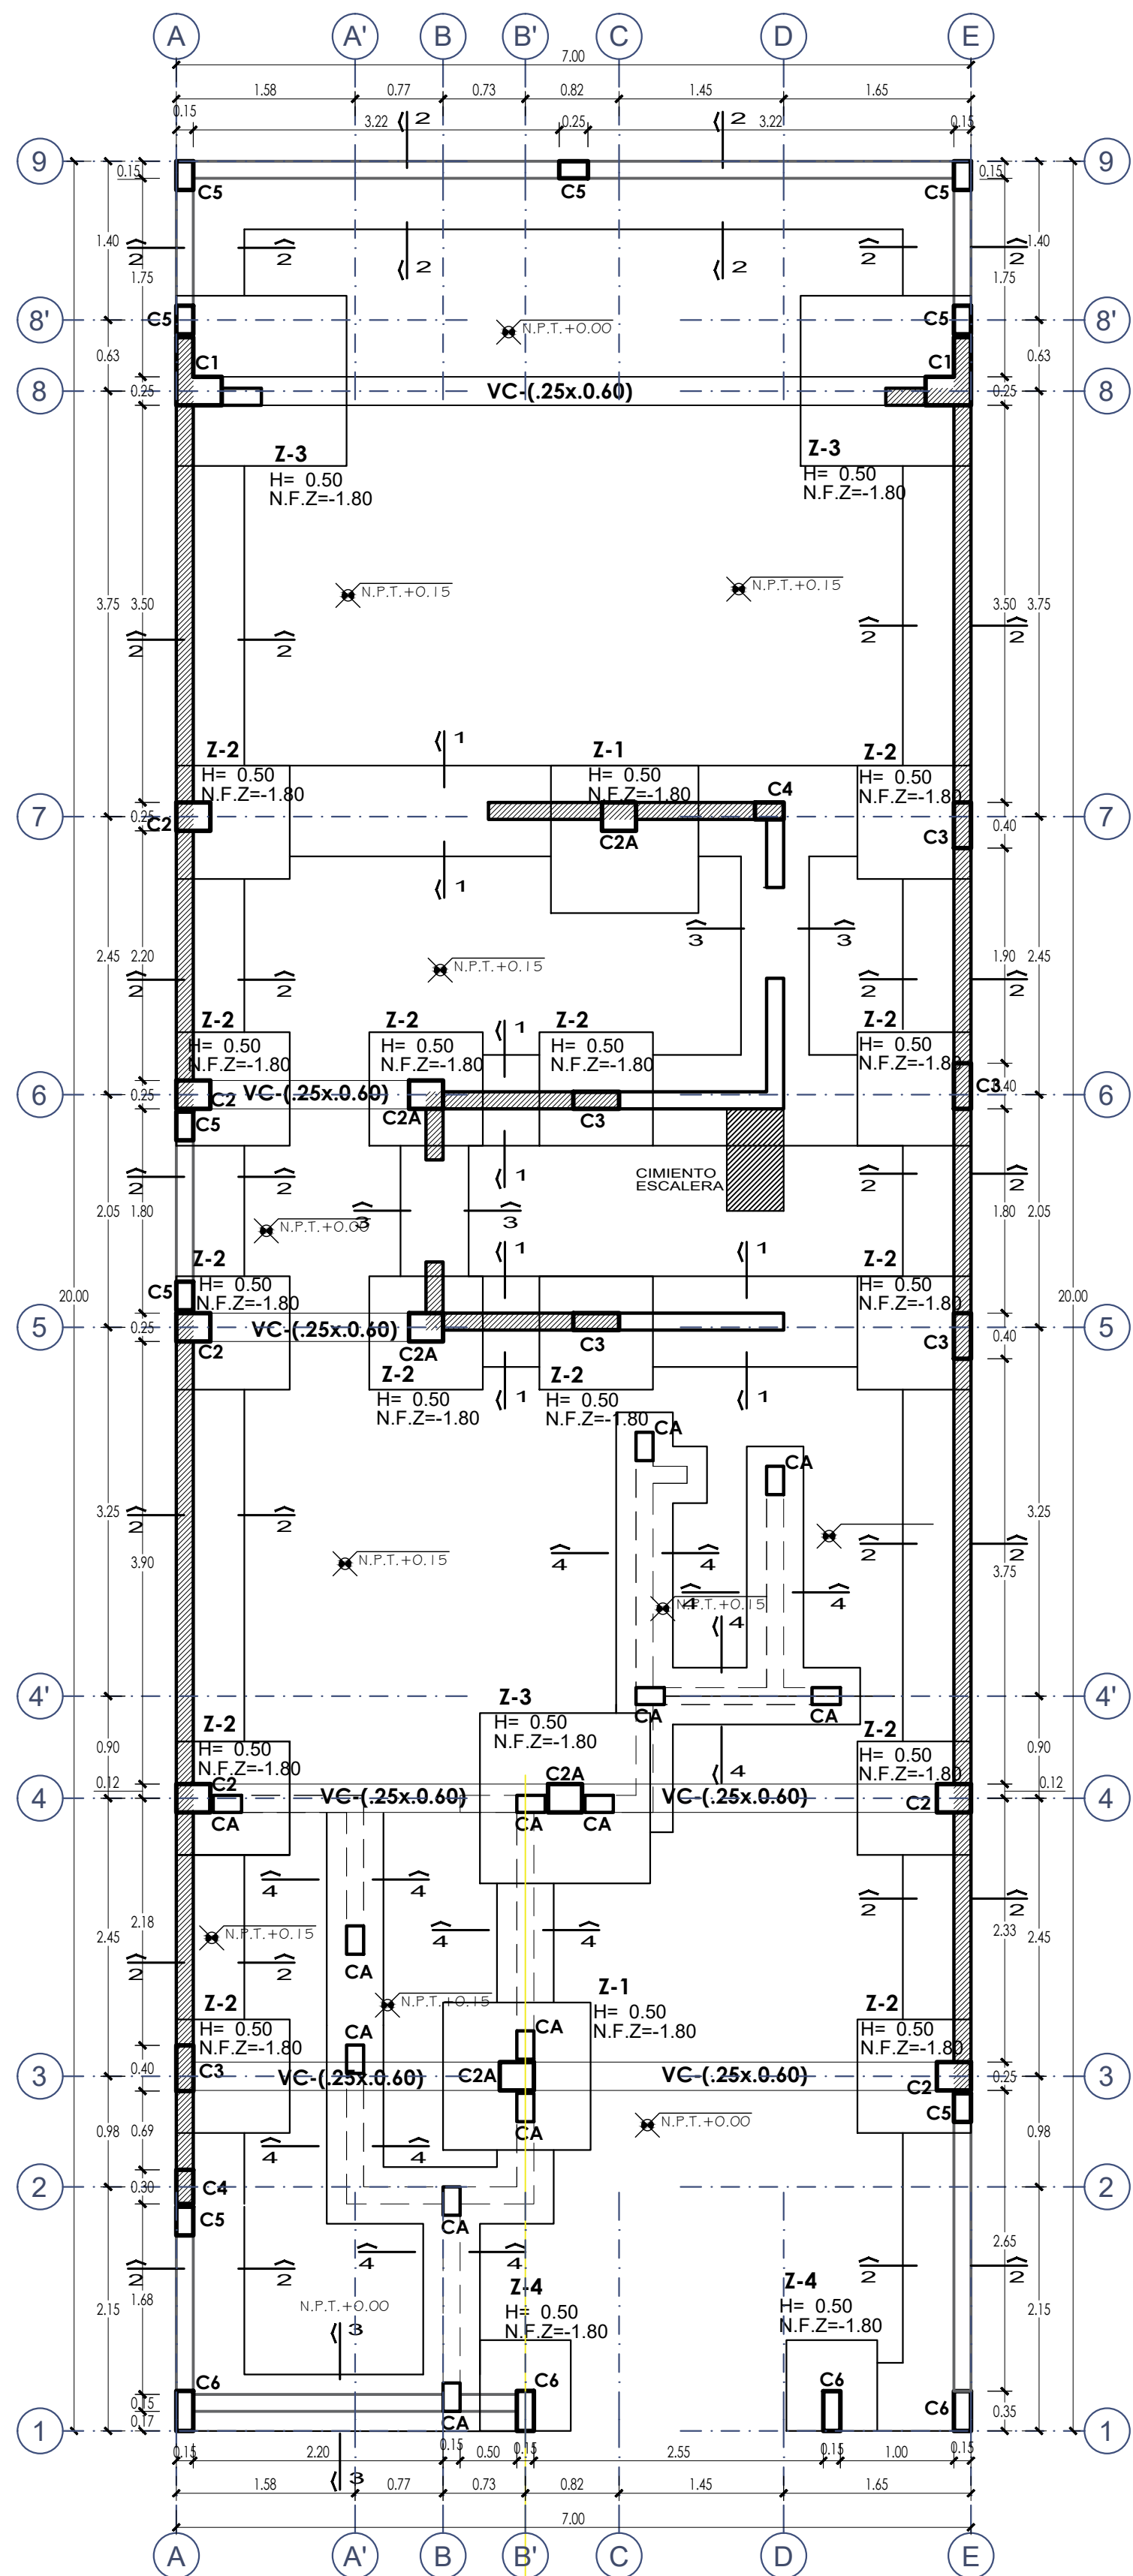


CIMENTACION
Escala 1/50

LEYENDA	
	MUROS TABIQUE
	MUROS PORTANTE
	COLUMNAS NUEVAS

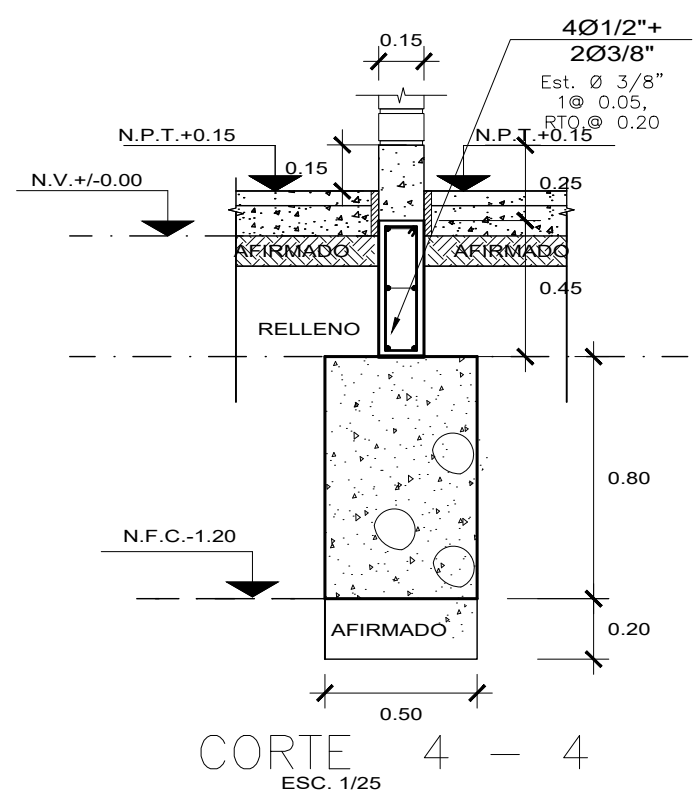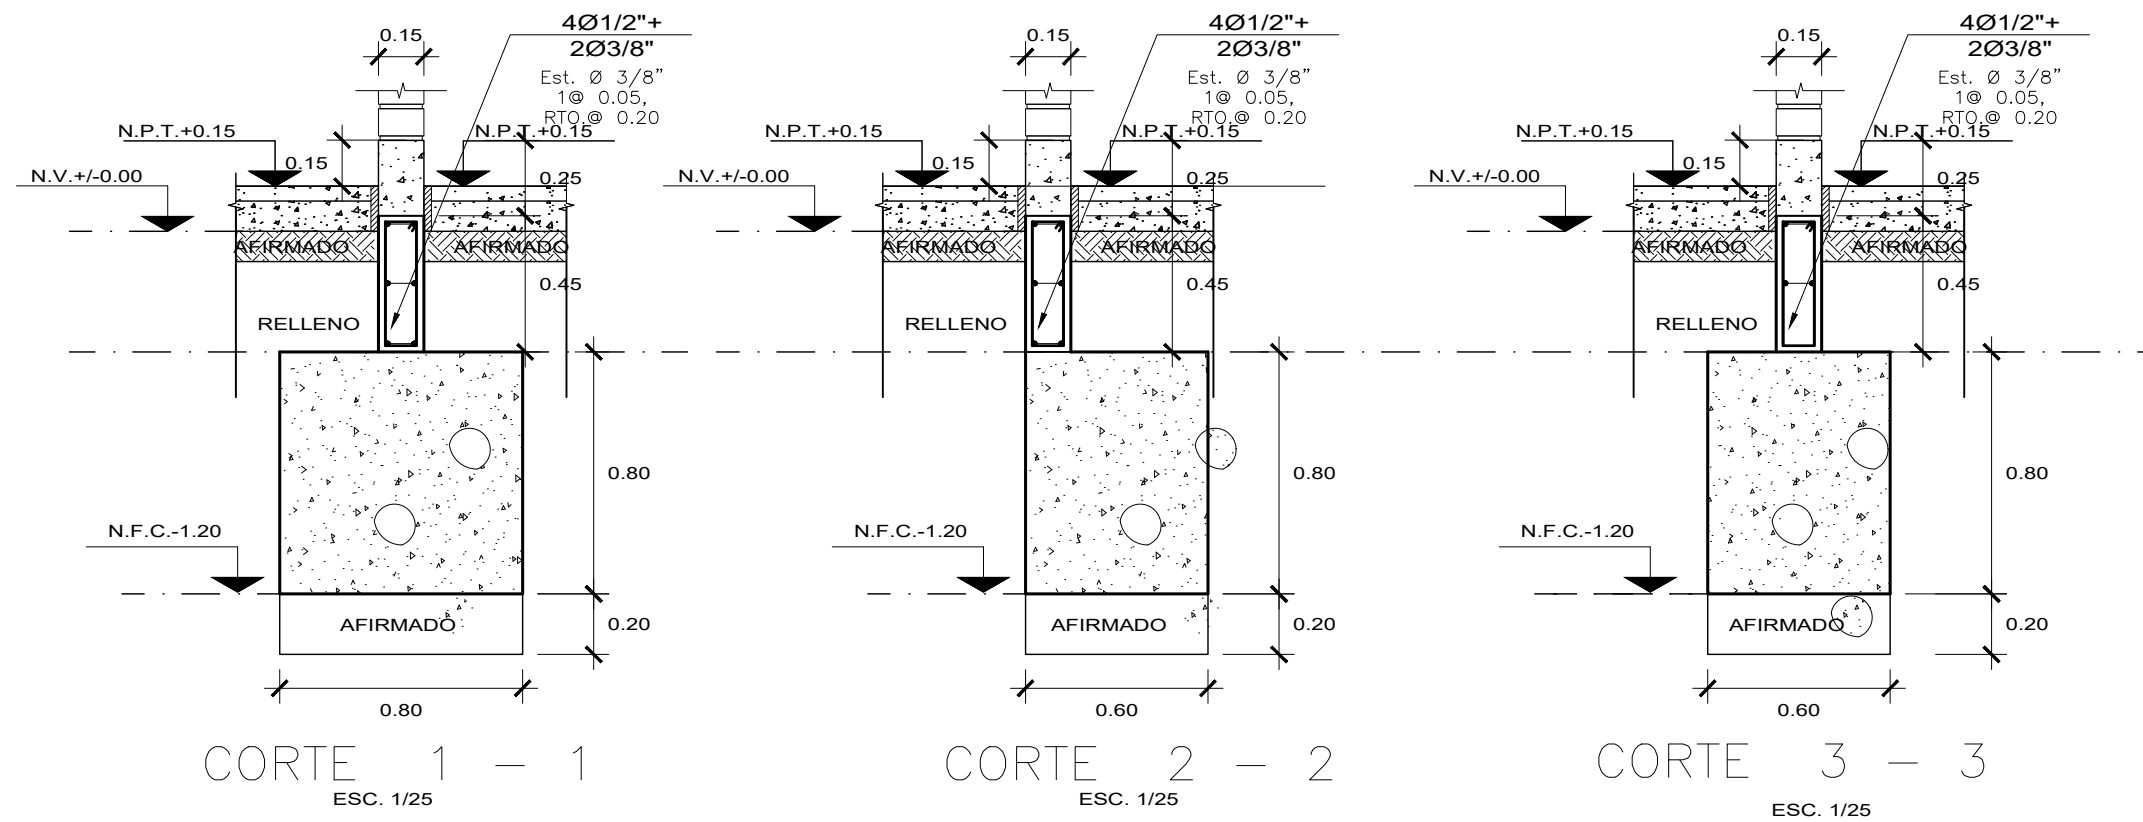

RESUMEN DE LAS CONDICIONES DE CIMENTACION	
Profesional Responsable:	:
Tipo de cimentación:	: ZAPATAS Y CIMENTOS CORRIDOS
Extrato o apoyo de cimentación	: Arena (Desde el nivel de terreno natural)
Profundidad de la napa frática	: No detectado
Parámetros de Diseño de la cimentación	
Profundidad de la cimentación Zapatas	: -1.80 m. a partir del NTN
Profundidad de la cimentación Cimientos corridos	: -1.20 m. a partir del NTN
Presión admisible	: 1.00 kg/cm2
Factor de seguridad por corte (Estático y dinámico)	: 3.00 y 2.50 respectivamente.
Asentamiento diferencial máximo aceptable	: 2.54 cms
Parámetros sísmicos del suelo (de acuerdo a la Norma E 030)	
Zona sísmica	: Zona 4 (Z = 0.45)
Tipo de perfil de suelo	: S3
Factor de suelo (S)	: 1.20
Periodo Tp (s)	: 0.90 seg
Periodo TL (s)	: 1.60 seg
Agresividad del suelo a la cimentación	: Insignificante
Tipo de cemento	: Tipo MS
Problemas especiales de cimentación	
Licuefacción	: No
Colapso	: No
Expansión	: No
Indicaciones adicionales	: Eliminar 40cm de turba, suelo inorgánico, tierra vegetal, desmonte, relleno sanitario o relleno superficial y estos materiales inadecuados deberán ser removidos en su totalidad antes de construir la edificación y ser reemplazados con materiales adecuados debidamente compactados.

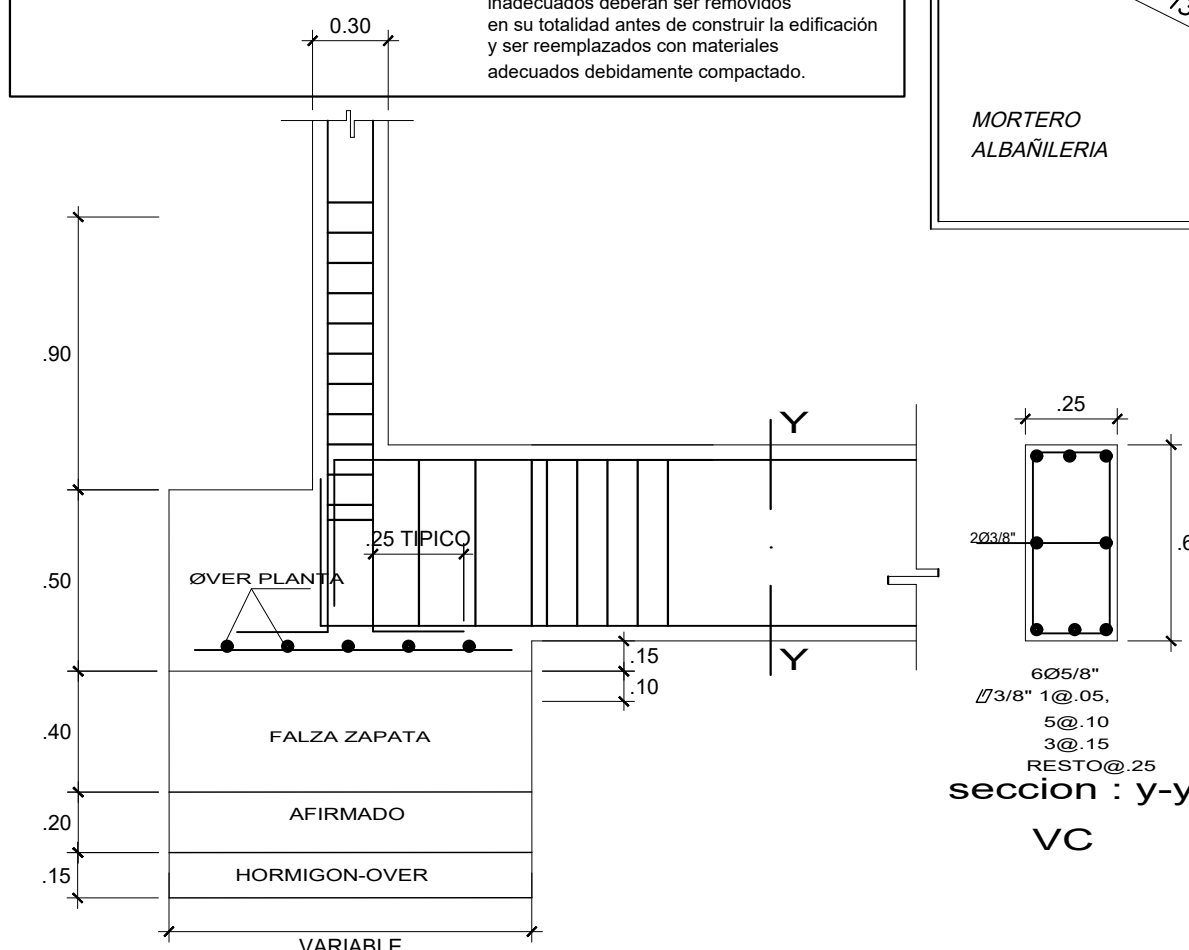

DETALLE TIPICO DE VIGA DE CIMENTACION
e = 1/25

ESPECIFICACIONES GENERALES

CONCRETO CICLOPEO

SOLADO / FALZA ZAPATA: 1:10 (CEMENTO : HORMIGON)+30%PG (6")

CIMENTOS: 1:10 (CEMENTO : HORMIGON)+30%PG (6")

FALSO PISO: 1:8 (CEMENTO : HORMIGON)

CONCRETO SIMPLE

SOBRECIMENTOS: CONCRETO $f_c = 175 \text{ Kg/cm}^2$

CONCRETO ARMADO

CONCRETO: $f_c = 210 \text{ Kg/cm}^2$ - ZAPATAS, VIGAS DE CIMENTACION

CONCRETO: $f_c = 210 \text{ Kg/cm}^2$ - COLUMNAS, VIGAS PRINCIPALES

CONCRETO: $f_c = 175 \text{ Kg/cm}^2$ - COLUMNAS, VIGAS AMARRE Y COLUMNETAS

ACERO DE REFUERZO: $f_y = 4,200 \text{ Kg/cm}^2$

RECUBRIMIENTOS

ZAPATAS: 7.5 cm.

MUROS Y PLACAS: 4.0 cm. (EN CARAS EN CONTACTO CON AGUA O TERRENO)

COLUMNAS Y VIGAS: 2.5 cm. (EN CARAS SECAS)

ALIFERADOS Y VIGAS CHATAS: 4.0 cm.

COLUMNAS Y VIGAS DE AMARRE: 2.5 cm.

TERRENO

CAPACIDAD PORTANTE: 1.00 Kg/cm2 (VERIFICAR EN OBRA)


PROF. DESPLANTE: 1.80 M (ZAPATAS)

1.20 M (CIMENTOS CORRIDOS)

SOBRE CARGA: S/C = INDICADA EN ENCOFRADOS


ALBAÑILERIA

UNIDAD DE ALBAÑILERIA: TODAS LAS UNIDADES DE ALBAÑILERIA DE MUROS SE FABRICARAN CON LAS DIMENSIONES MINIMAS INDICADAS EN ESTE PLANO, PODRAN SER DE ARCILLA O SILICO CALCCAREO, DEBERAN CLASIFICAR COMO MINIMO CON LA CLASE IV DE LA NORMA CORRESPONDIENTE.


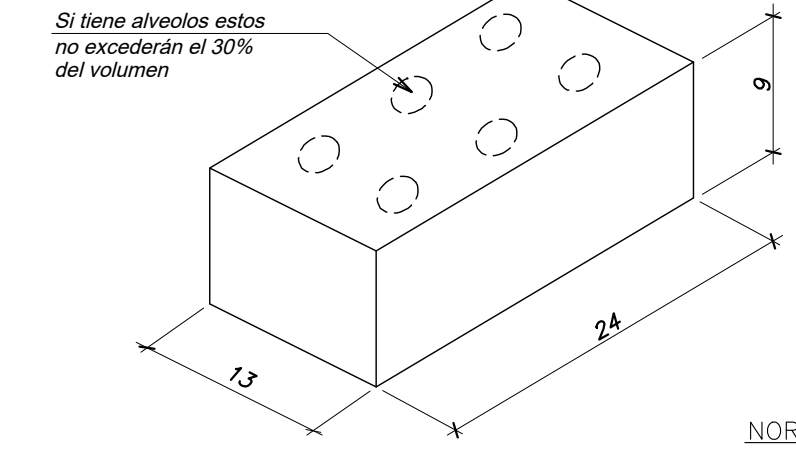


MORTERO: 1:4 (CEMENTO - ARENA)
ALBAÑILERIA: $f_m = 65 \text{ Kg/cm}^2$

NORMAS: E-070, E-060, E-050, E-030

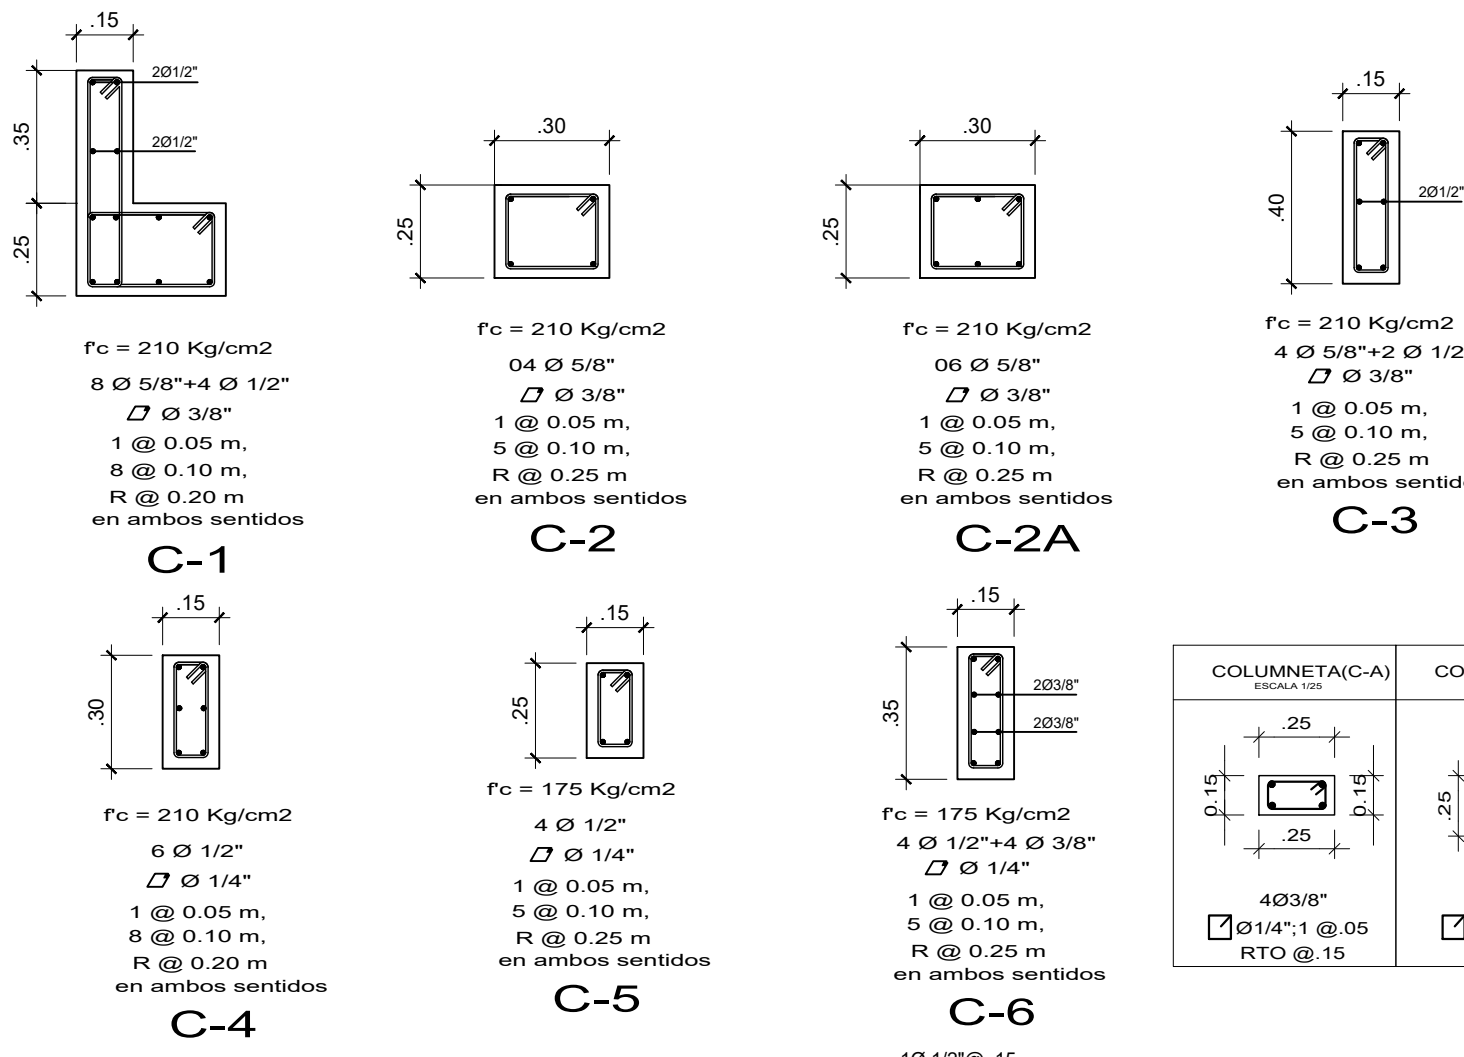


COLUMNAS -SECCIONES

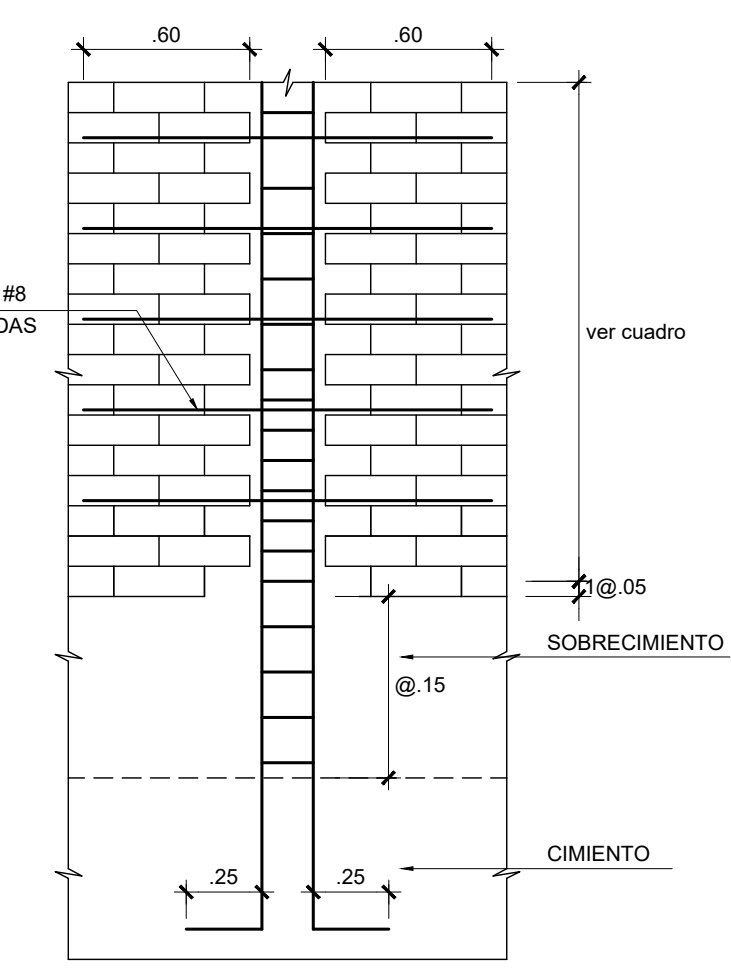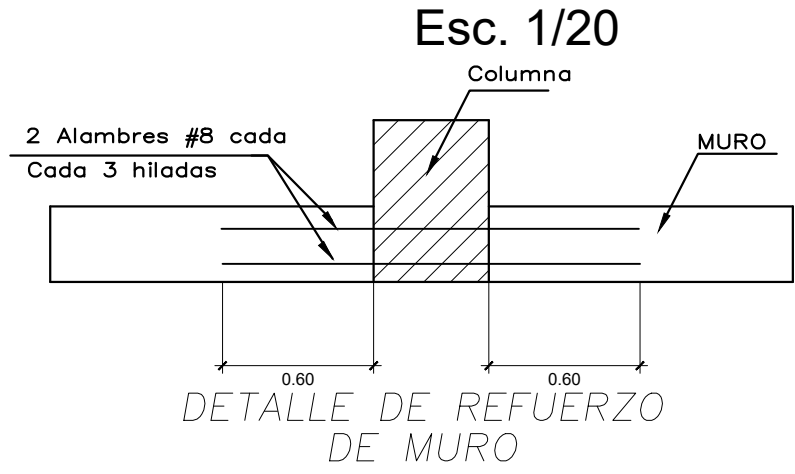

ANCLAJE DE COLUMNA EN CIMENTO CORRIDO EN MUROS PORTANTES

Nota: Los alambres doblan en U en las columnetas o son pasantes.

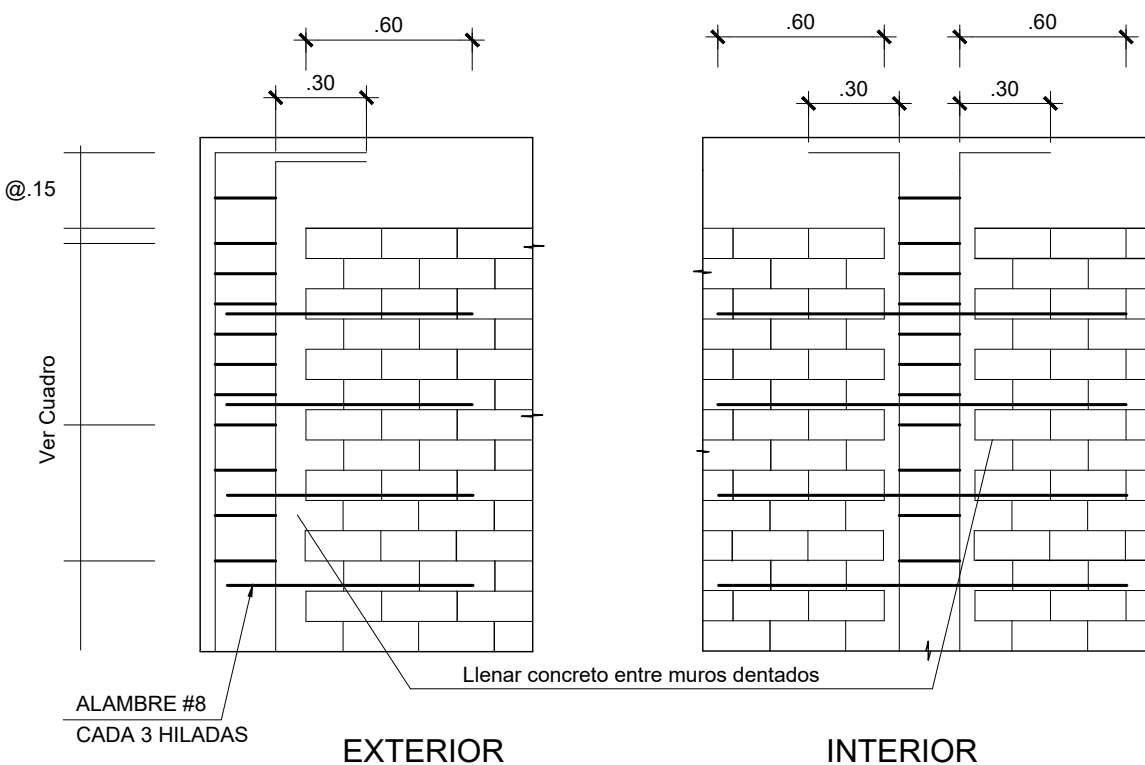


REMATE DE COLUMNAS EN MUROS

PLANTA DE ZAPATA

ESC: 1/25

CUADRO DE ZAPATAS

TIPO	DIMENSION A x B	H	PARRILLA
Z-1	1.30 x 1.30	0.50	Ø 1/2 @ 0.15
Z-2	1.00 x 1.00	0.50	Ø 1/2 @ 0.15
Z-3	1.50 x 0.50	0.50	Ø 1/2 @ 0.15
Z-4	0.80 x 0.80	0.50	Ø 1/2 @ 0.15

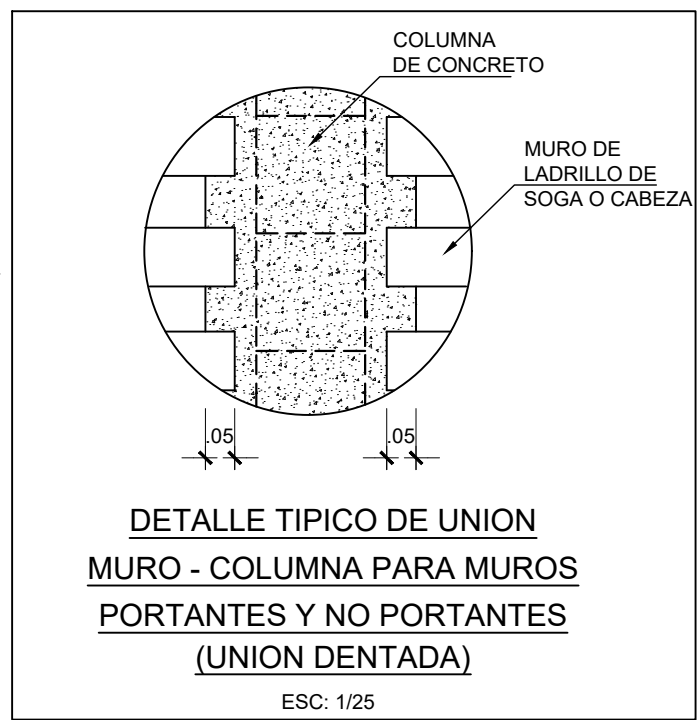

DETALLE TIPICO DE UNION MURO - COLUMNA PARA MUROS PORTANTES Y NO PORTANTES (UNION DENTADA)

ESC: 1/25

CONCENTRACION TIPICA DE ESTRIBOS EN COLUMNAS

Escala: 1/25

Z = 0.45	U = 1.00	S = 1.05	C = 2.50
Rx = 3 ALBAÑILERIA CONFINADA			
Rx = 3 ALBAÑILERIA CONFINADA			
	DESPLAZAMIENTO MAXIMO DEL ULTIMO NIVEL	MAXIMO DESPLAZAMIENTO RELATIVO ENTRE PISOS	LIMITE ADMISIBLE DE DESPLAZAMIENTO RELATIVO LATERAL DE ENTREPISO
X	0.72cm	0.003	5 / 000
Y	0.08 cm	0.0003	5 / 000
USAR JUNTA DE SEPARACION SISICA CON SECTORES ADYACENTES DE 5.00 cm.			

PROYECTO:

VIVIENDA UNIFAMILIAR

UBICACIÓN:

URBANIZACIÓN CAMPESTRE LOMA BLANCA Mz. M - Lote 15 - PIURA

PROPIETARIO:

Sr. PEREYRA FARIAS JAIME DOMINGO

DNI: 02609435

Sra. CABREJOS CARBONEL DORALIZA DAMINA ELENA

DNI: 02622737

DIBUJO: JLAY

RESPONSABLE: ARQ. RENZO IZQUIERDO

ESCALA: 1 / 50


FECHA: MAYO 2026

TITULO DE LÁMINA:


ESTRUCTURAS
PLANTA DE CIMENTACIÓN Y DETALLES

Nº LÁMINA:



E-01

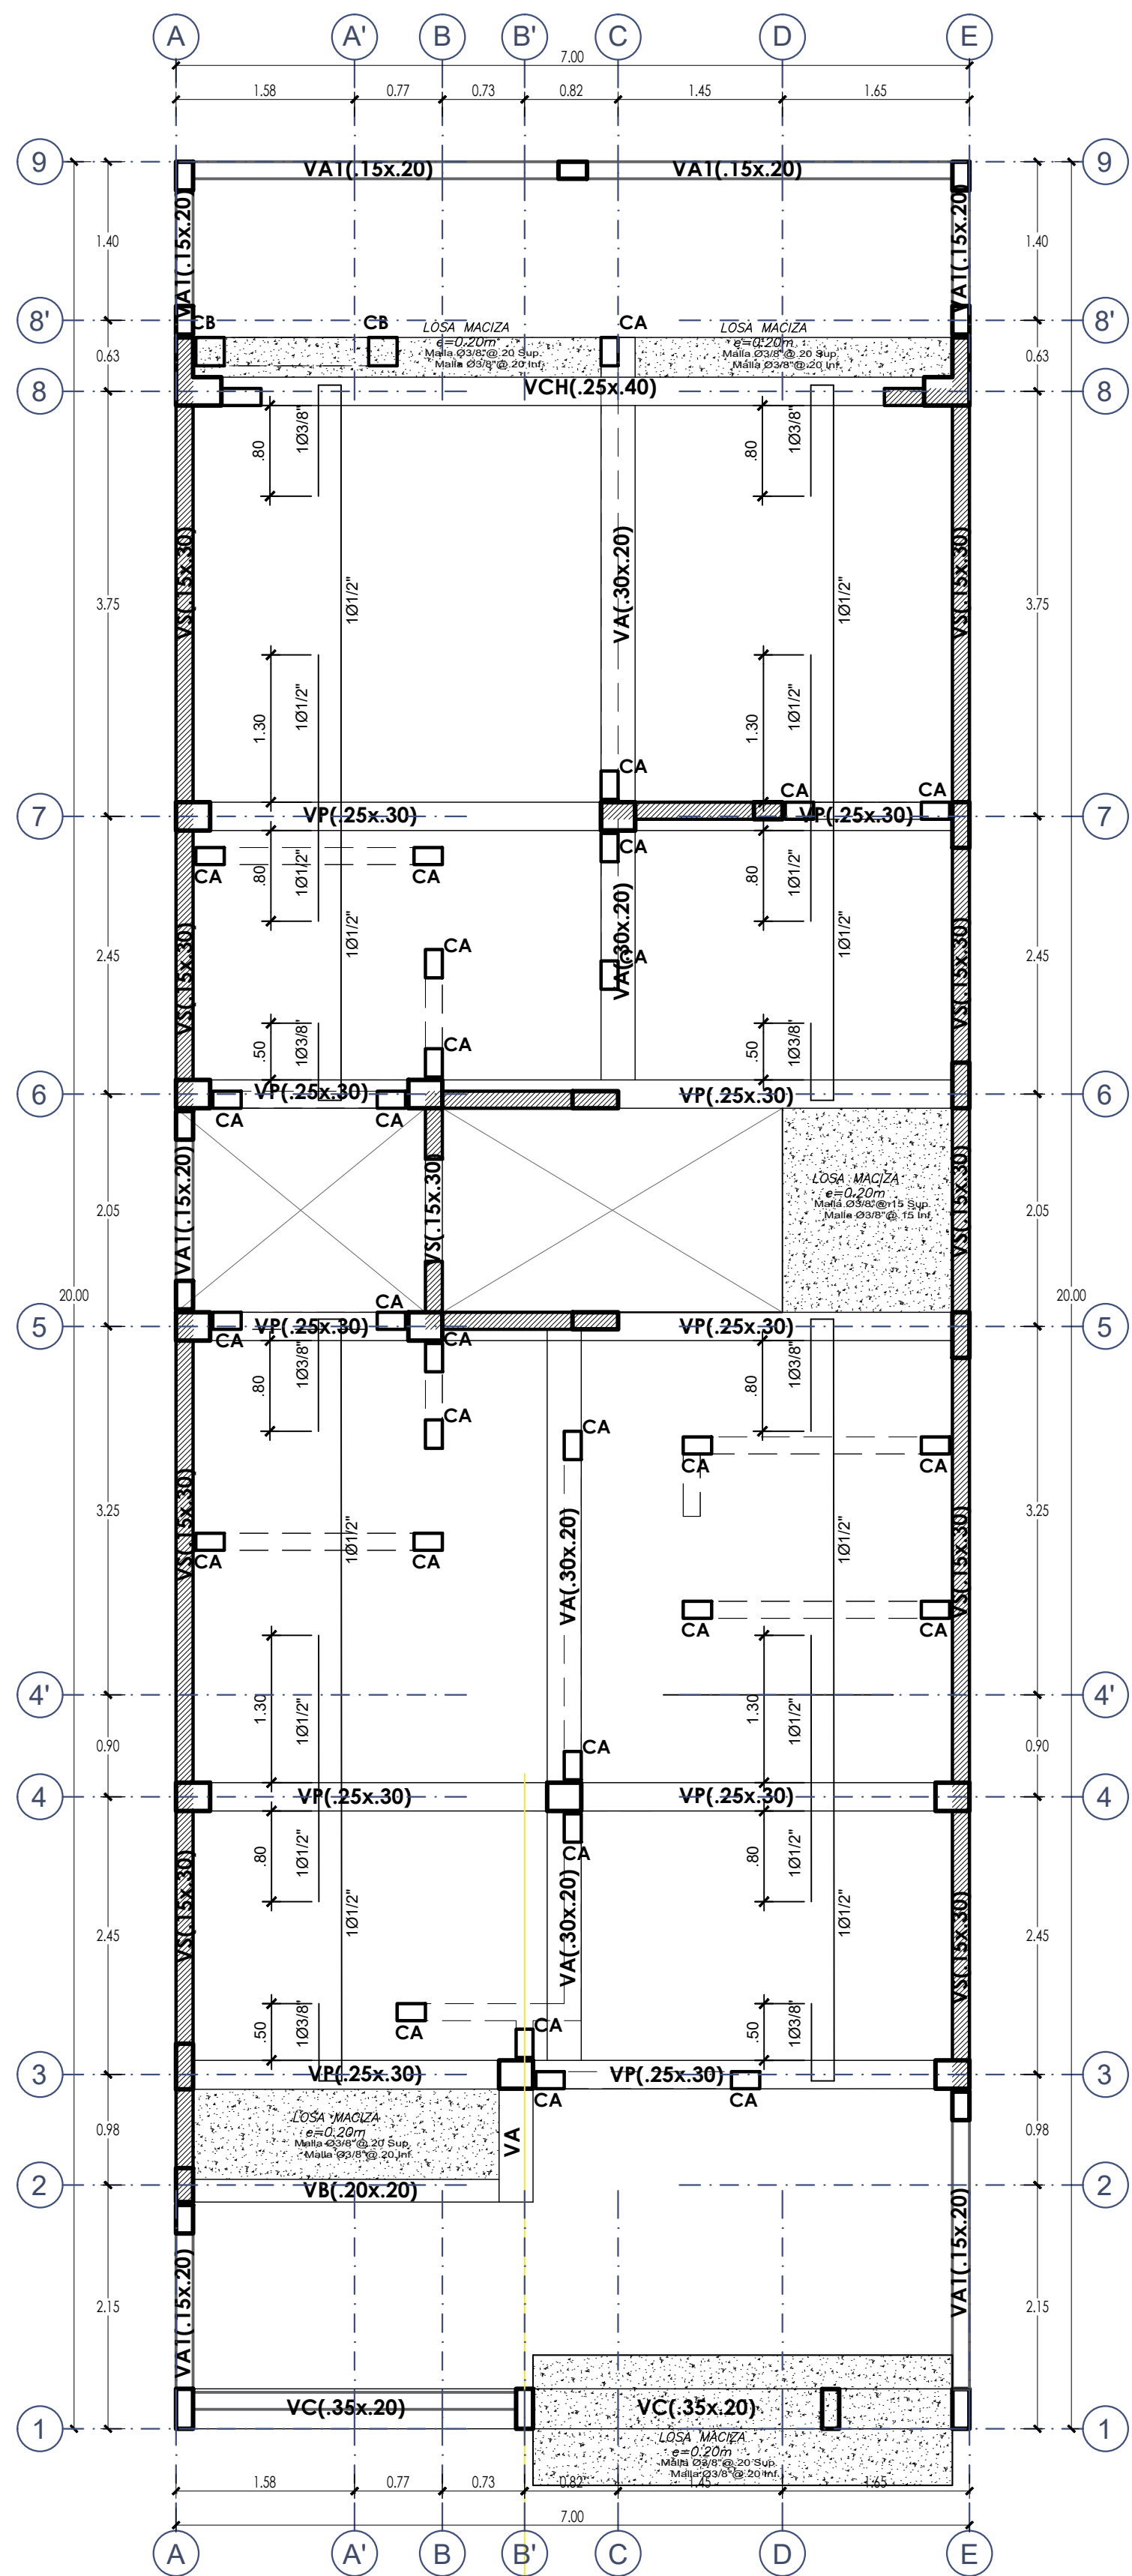



PRIMER PISO (S/C = 200 Kg/m²)

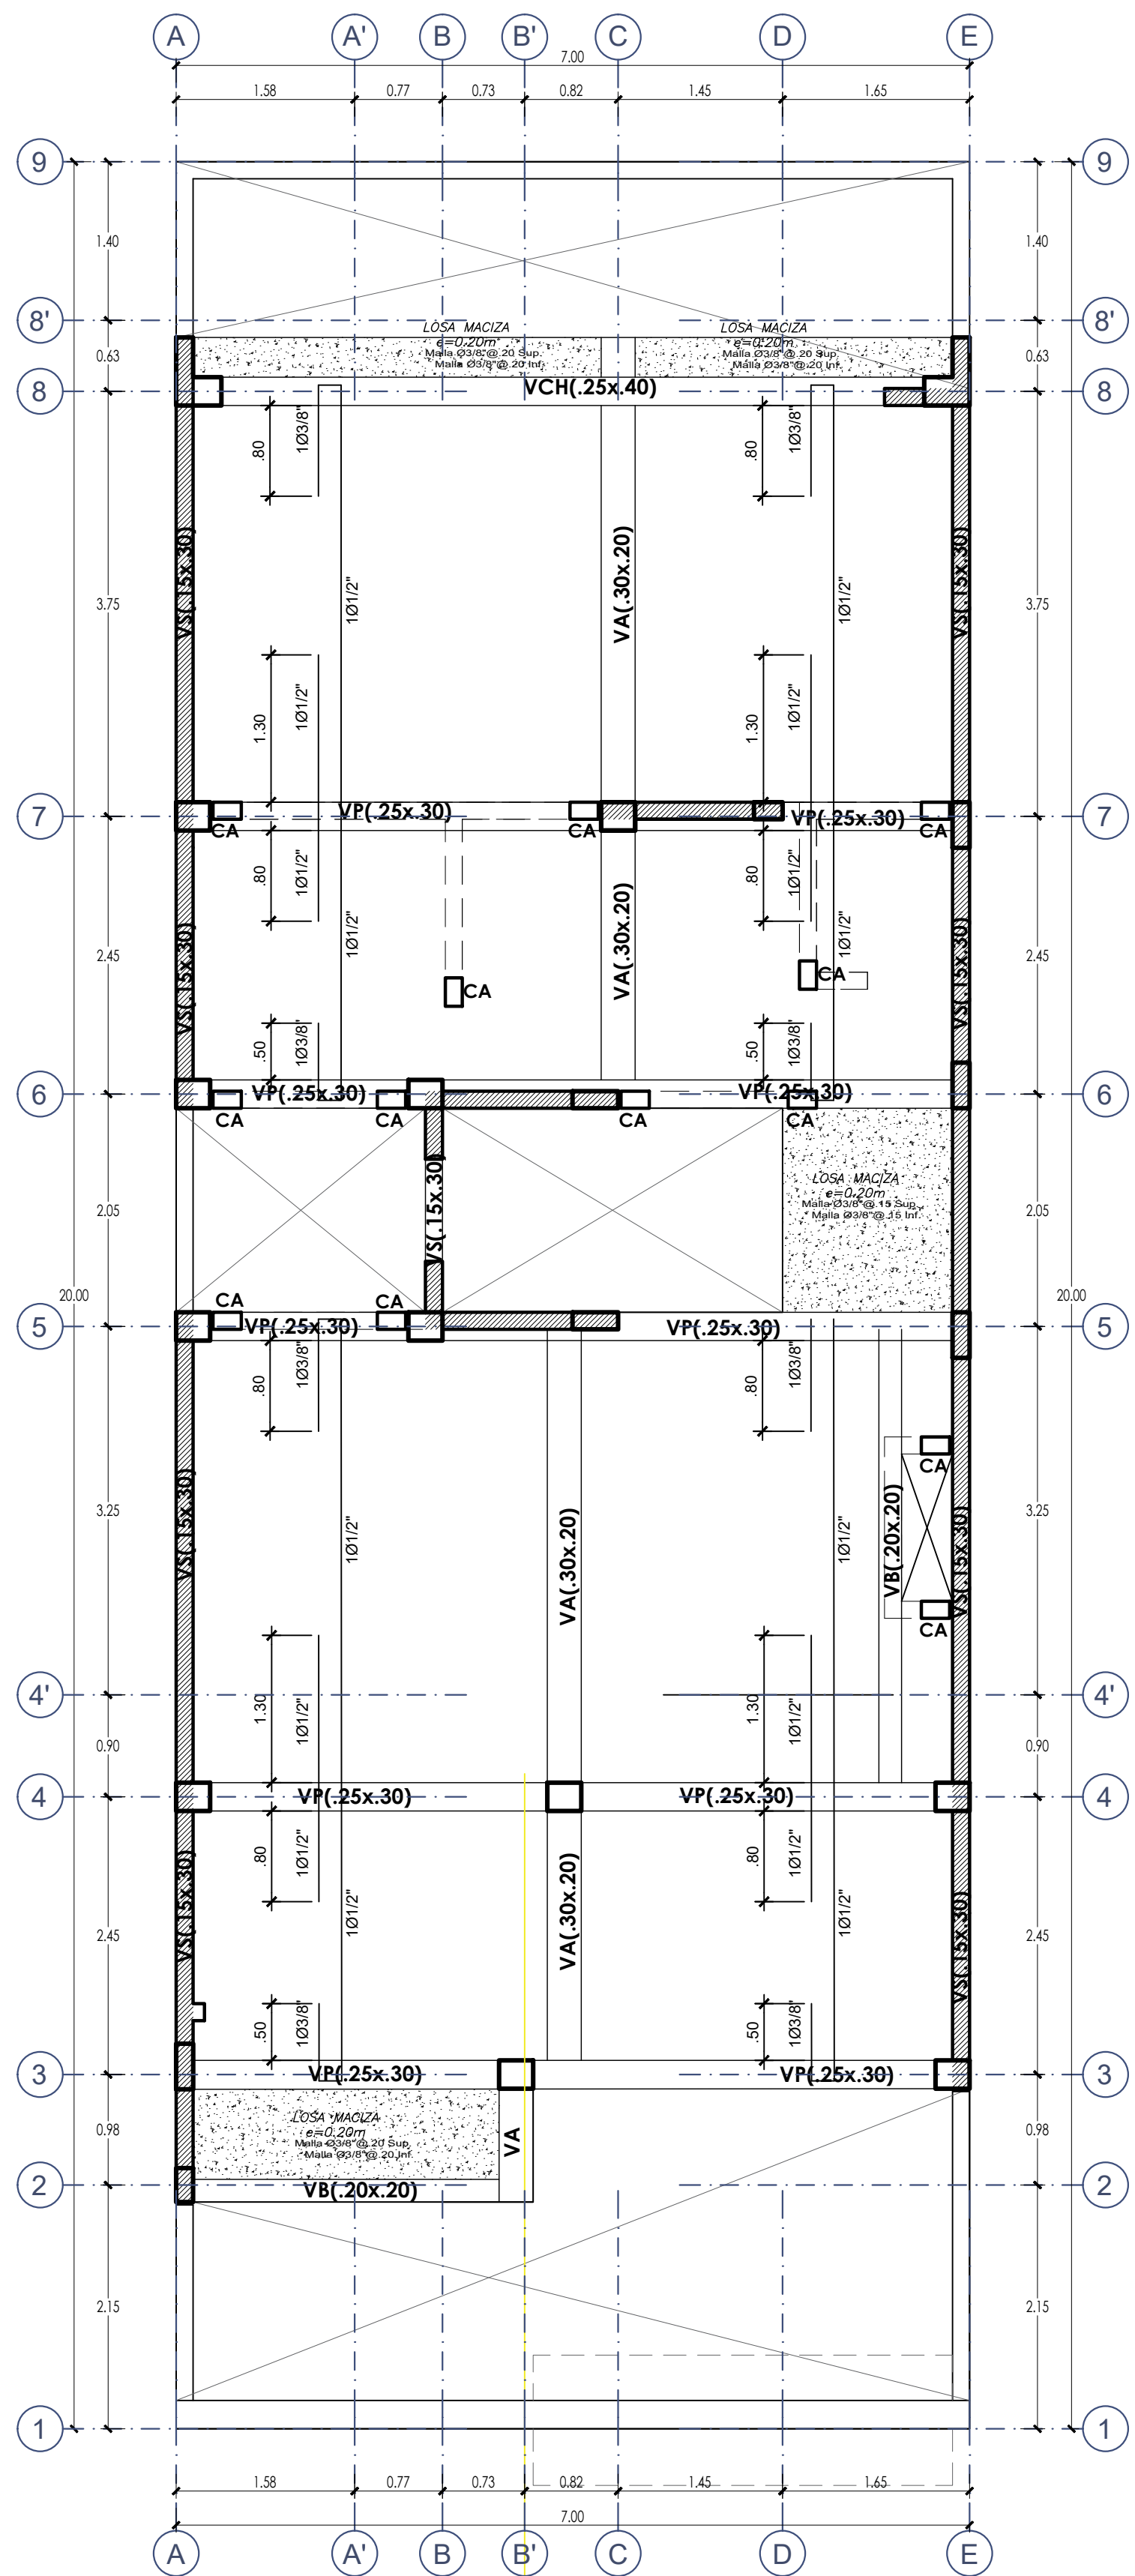

SEGUNDO PISO (S/C = 200 Kg/m²)

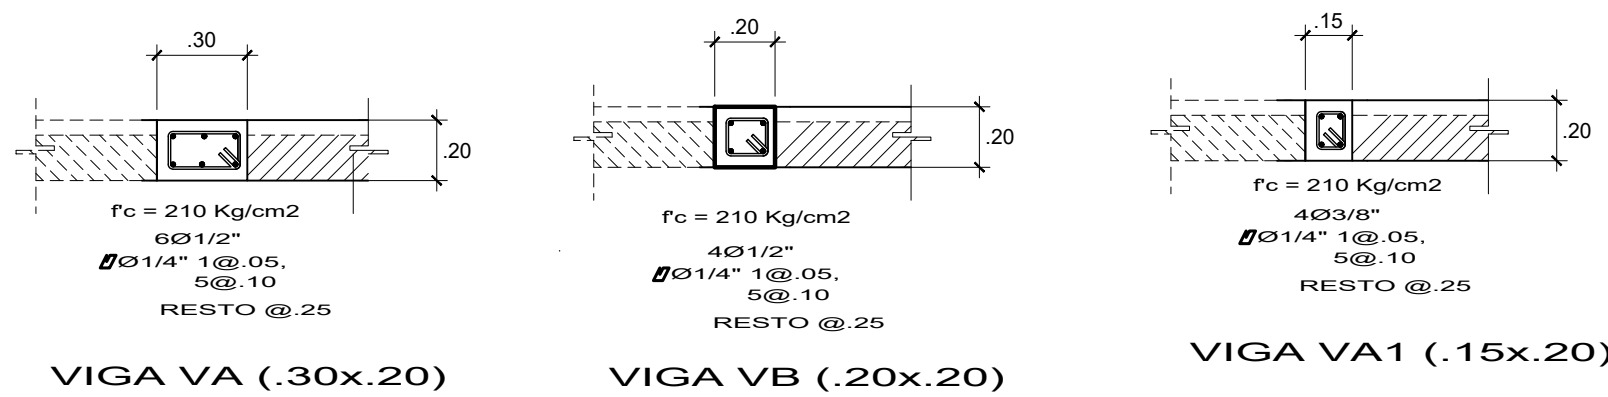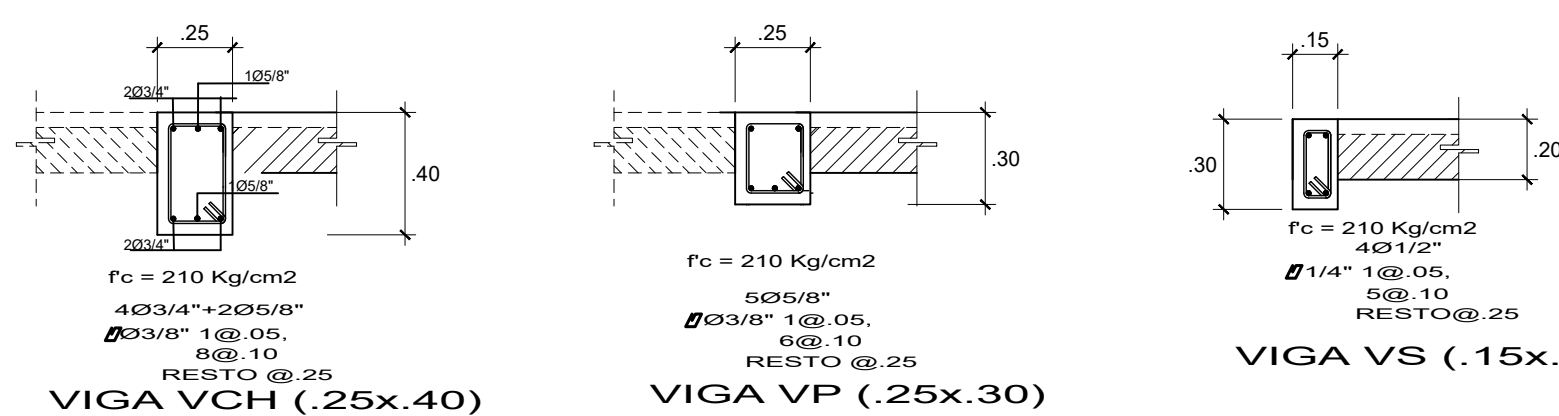


LEYENDA

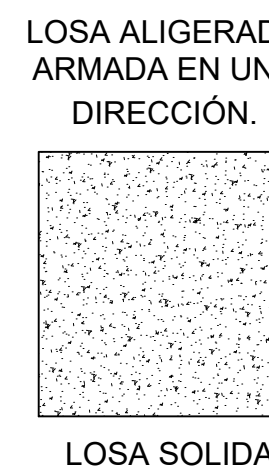 


LONGITUD DE TRASLAPE

1.) USO:

- SOLO DONDE NO SE INDIQUE EXPRESAMENTE EN LOS PLANOS
- SE TRASLAPARA MAXIMO EL 50% DEL REFUERZO QUE PASA POR UNA SECCION Y ENTRE DOS TRASLAPES SUCESIVOS HABRA UNA DISTANCIA MINIMA DE 40 DIAMETROS DEL REFUERZO MINIMO.

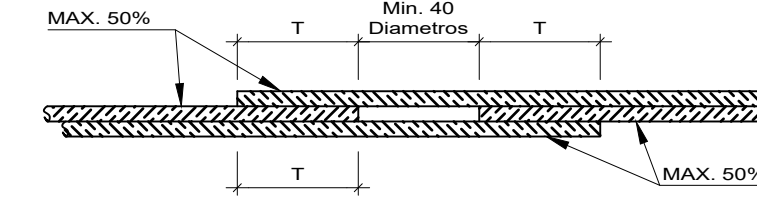


2.) LONGITUD:

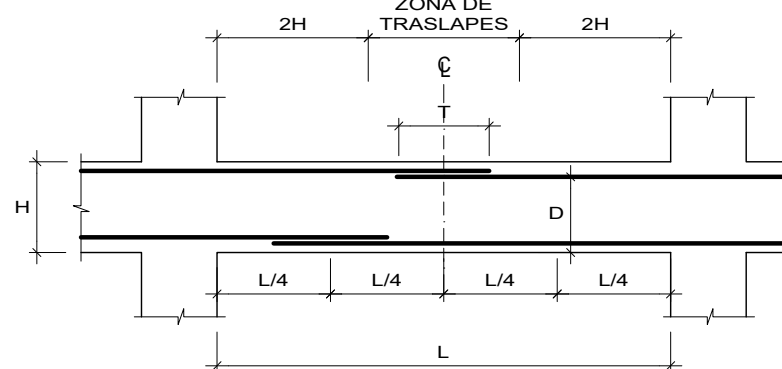

REFUERZO HORIZONTAL

LONGITUD (T) en cm		
Ø Horizontal con H>30cm	Ø Vertical y Ø Horizontal con H<30cm	
8mm	45	35
3/8"	45	40
1/2"	50	40
5/8"	60	45
3/4"	75	55


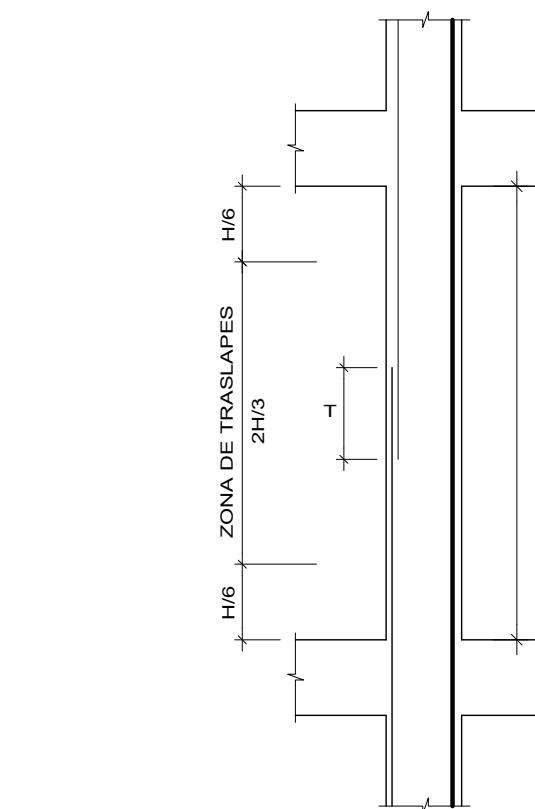


REFUERZO VERTICAL

COLUMNETA (C-A)	COLUMNETA (C-B)
403/8" Ø 1/4" 1 @ 05 RTO @ 15	403/8" Ø 1/4" 1 @ 05 RTO @ 15


CORTE TIPICO LOSA SOLIDA

ESC. 1/25

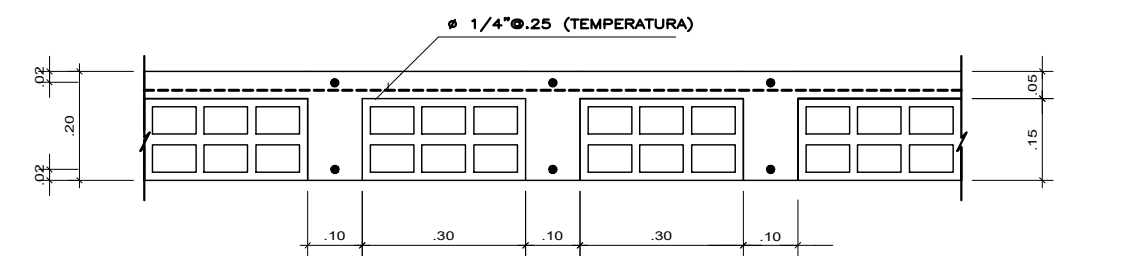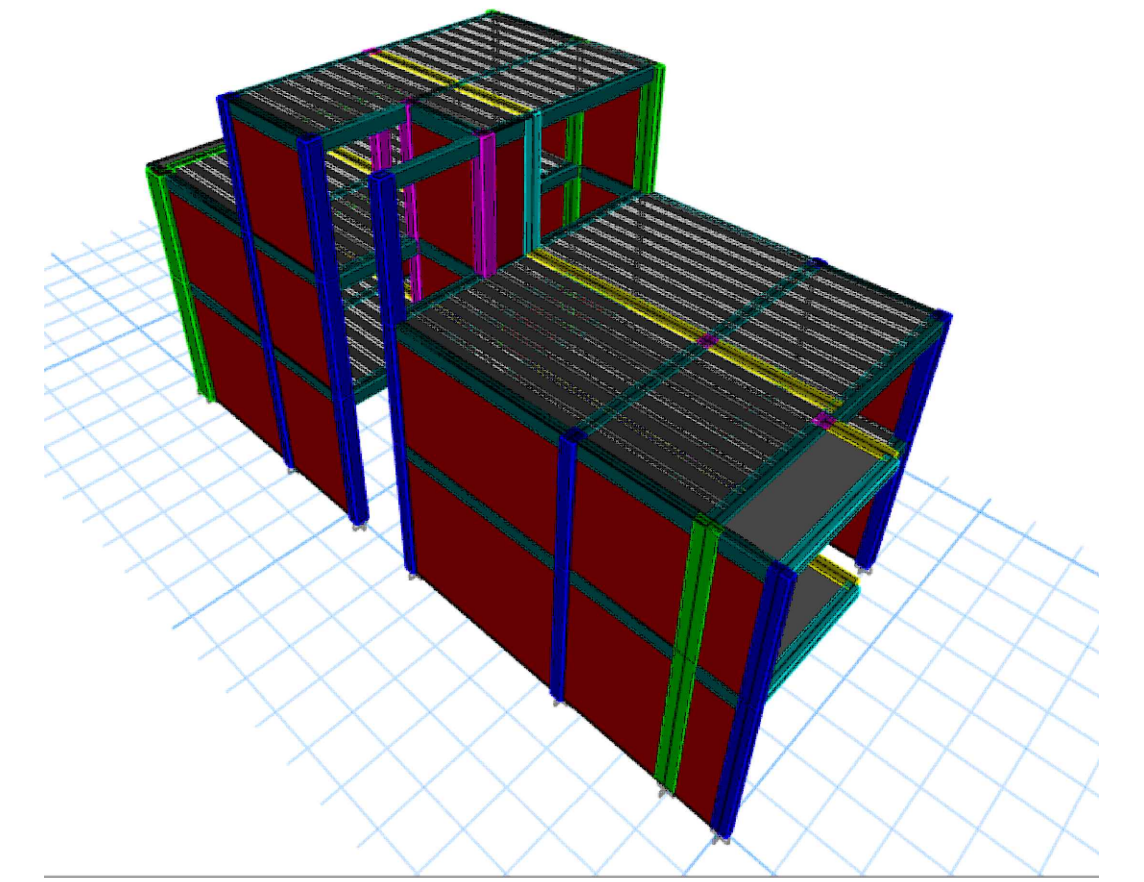



DETALLE TIPICO DE ALIGERADO h=0.20

ESCALA 1/10

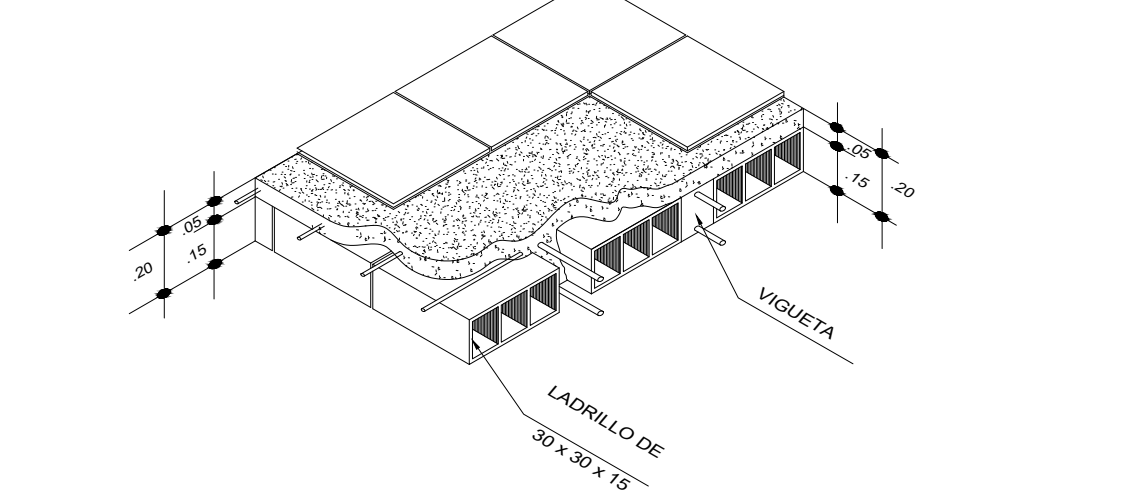

DETALLE TIPICO ISOMETRICO LOSA ALIGERADA

DINTEL EN ZONA DE VANOS

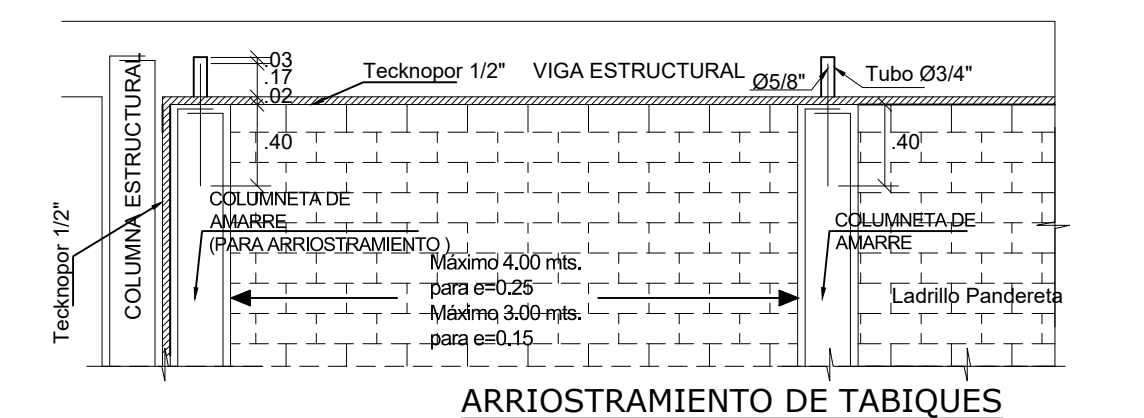
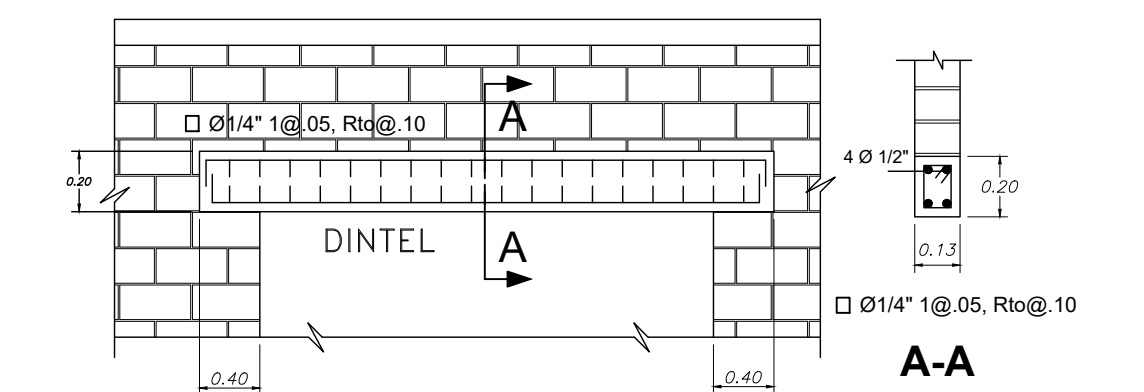


CORTE 1 - 1:

Columneta de Amarre (C.A.)

403/8"


Ø 1/4" 1 @ 05 RTO @ 15

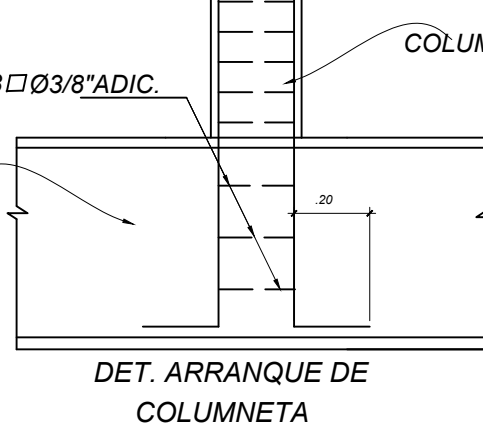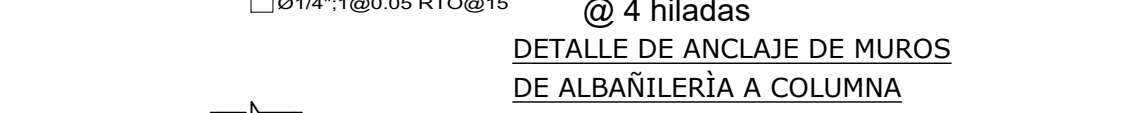




DET. ARRANQUE DE COLUMNETA

- 1) COLUMNETAS DE AMARRE DE MUROS TABIQUES COLOCARLAS ESPACIADAS MAXIMO 3.00m
- 2) DEJAR ANCLAJES EN EL ENCUENTRO DE MUROS TABIQUES CON COLUMNAS Y MUROS ESTRUCTURALES, ALAMBRE # 8 CADA 3 MUROS.
- 3) VACIAR LAS COLUMNETAS DESPUES DE DESMONTAR LOS TECHOS
- 4) SI LOS MUROS TABIQUES NO LLEGAN AL TECHO POR TENER VENTANA SE COLOCARA UNA VIGA SOLERA VA 15x20 EN LA PARTE SUPERIOR.
- 5) LOS MUROS DE TABIQUERIA SERAN CONSTRUIDOS CON UNIDADES DE ALBAÑILERIA LADRILLO DE ANCLAJE PANDERETA 20cm x 11cm x 9cm EN TABIQUERIA
- 6) EL MORTERO SERA EN PROPORCION: CEMENTO-ARENA 1:4 CON JUNTAS ENTRE HILADAS DE 1 CM CON MARIÑA VARIACION DE ±30mm.
- 7) SI NO ESTA APOYADO EN VIGA COLOCAR DOBLE VIGUETA EN LAS ZONAS DE MUROS TABIQUES



PROYECTO: VIVIENDA UNIFAMILIAR	UBICACIÓN : URBANIZACIÓN CAMPESTRE LOMA BLANCA Mz. M - Lote 15 - PIURA PROPIETARIO: Sr. PEREYRA FARIAS JAIME DOMINGO DNI: 02609435 Sra. CABREJOS CARBONEL DORALIZA DAMINA ELENA DNI: 02622737	DIBUJO : JLAY RESPONSABLE : ARQ. RENZO IZQUIERDO ESCALA : 1 / 50 FECHA : MAYO 2026	TITULO DE LÁMINA: ESTRUCTURAS ALIGERADOS Y DETALLES	N° LÁMINA: E-02

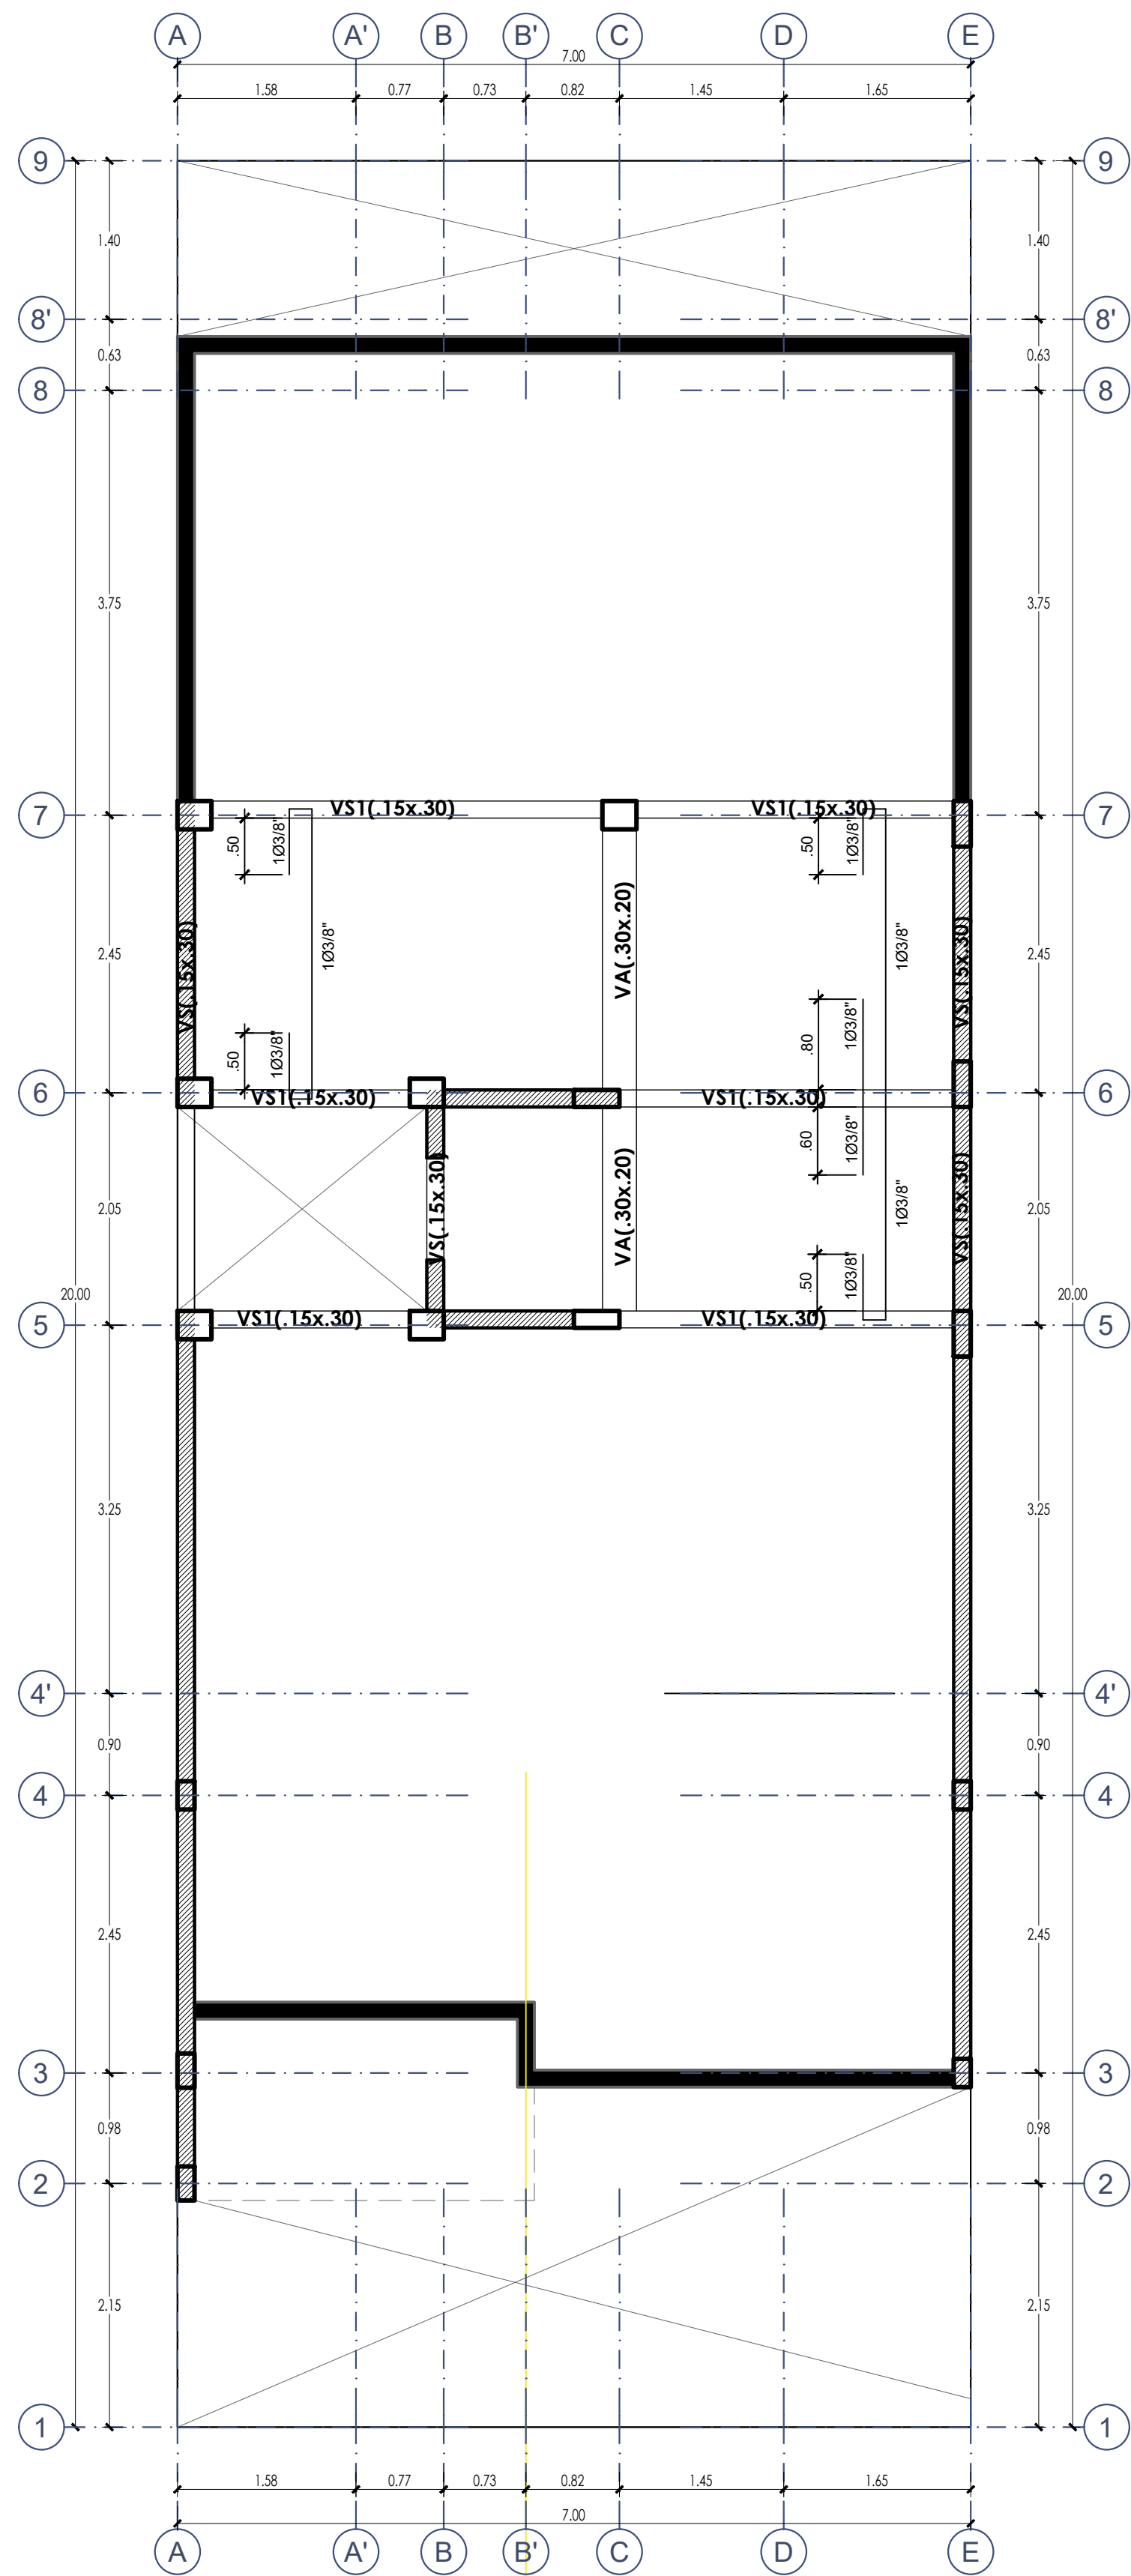

LEYENDA	
	MUROS TABIQUE
	MUROS PORTANTE
	COLUMNAS NUEVAS
	PARAPETO

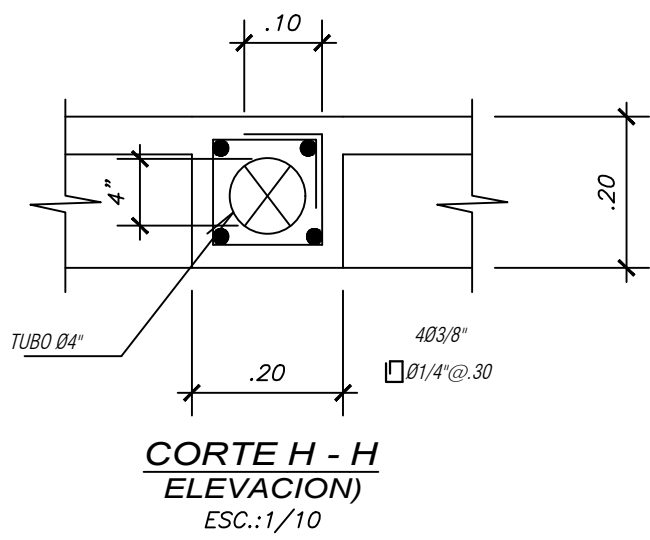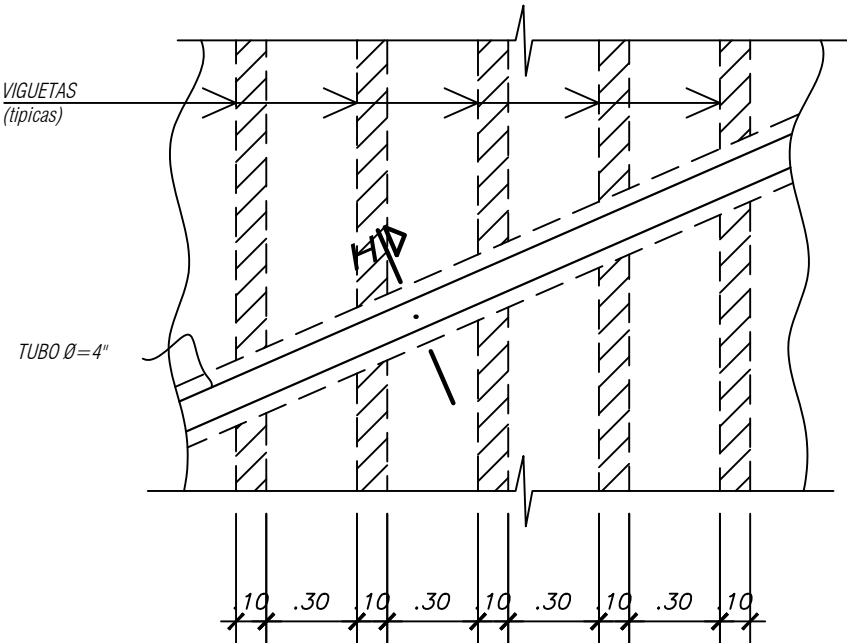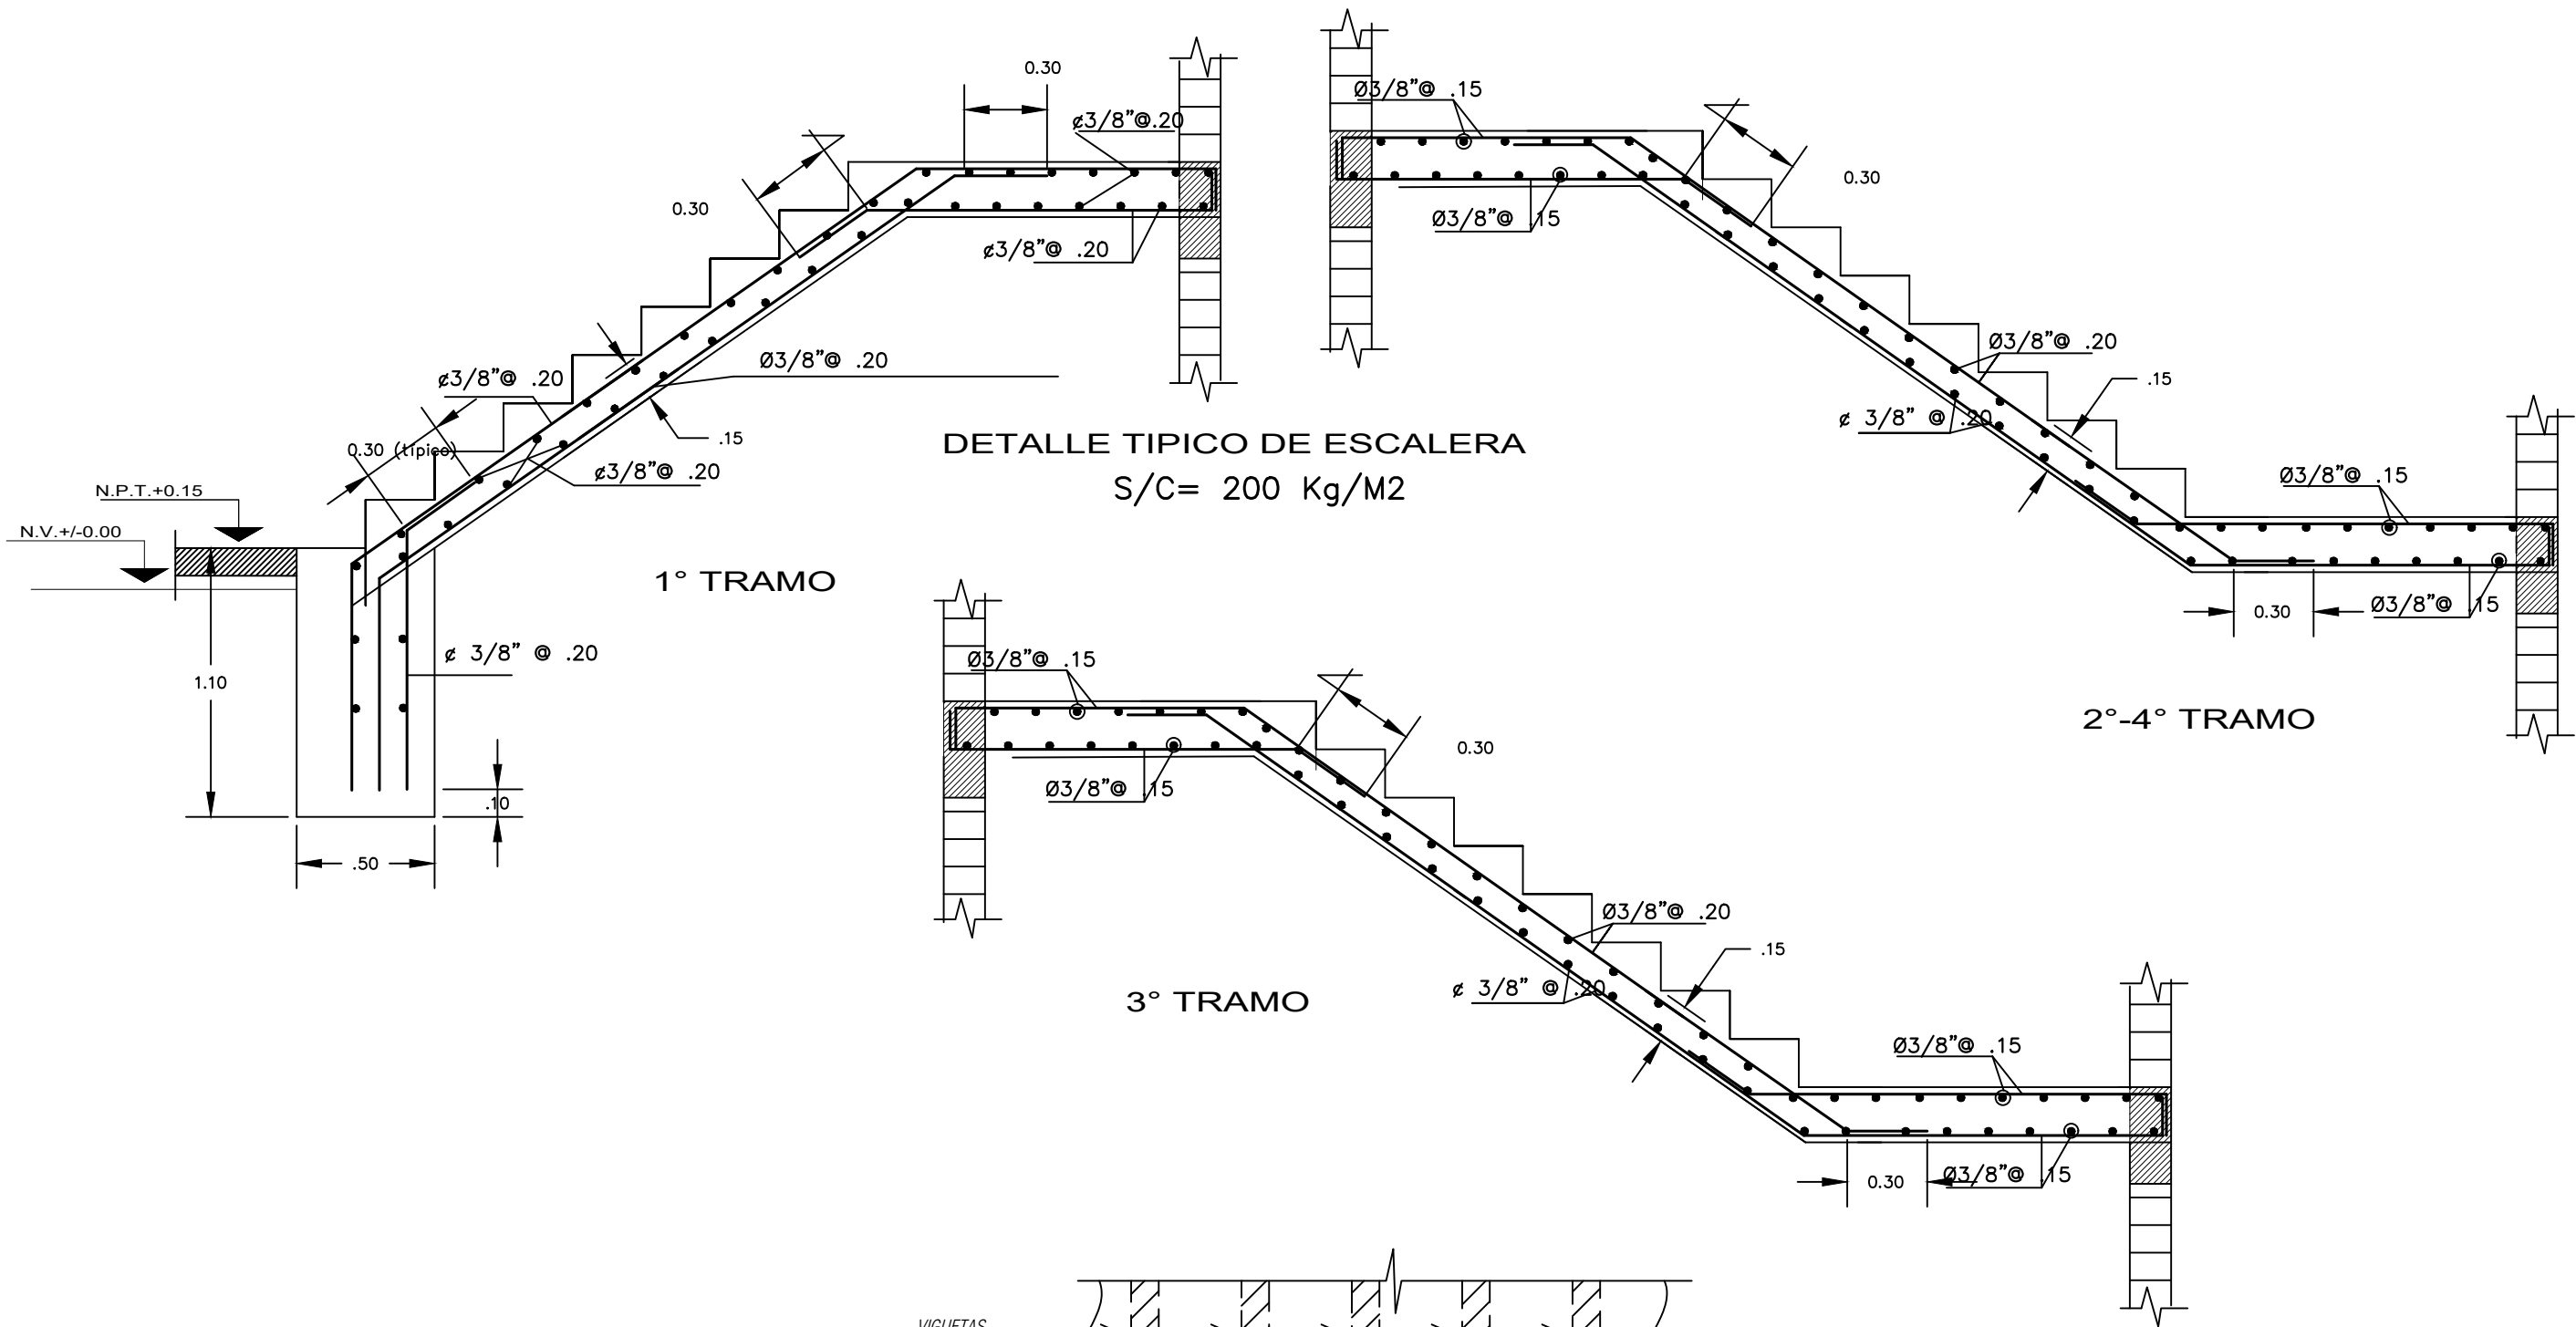

REFUERZO TÍPICO DE VIGUETAS EN CASO DE CRUCE DE TUBERIAS 4" EN ALIGERADO

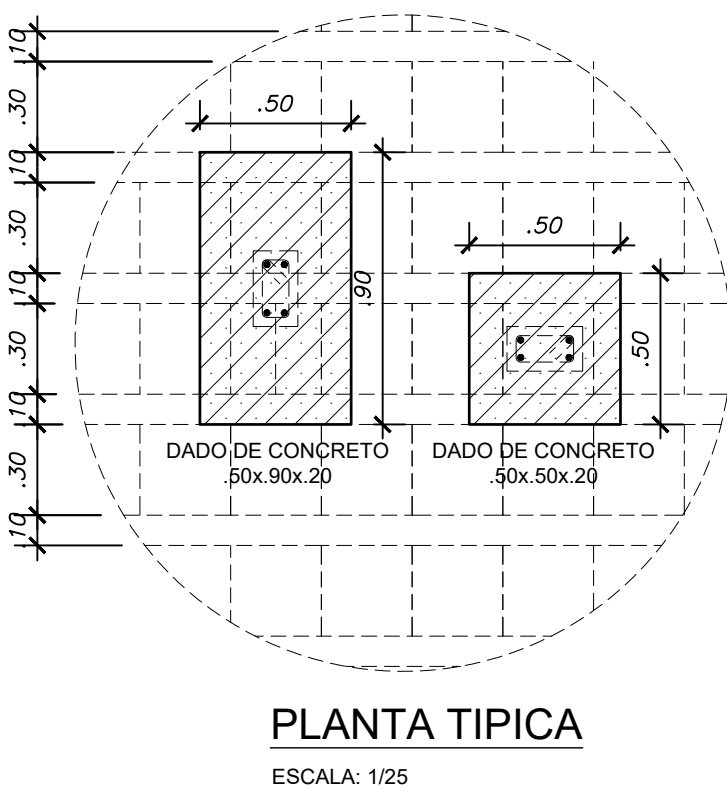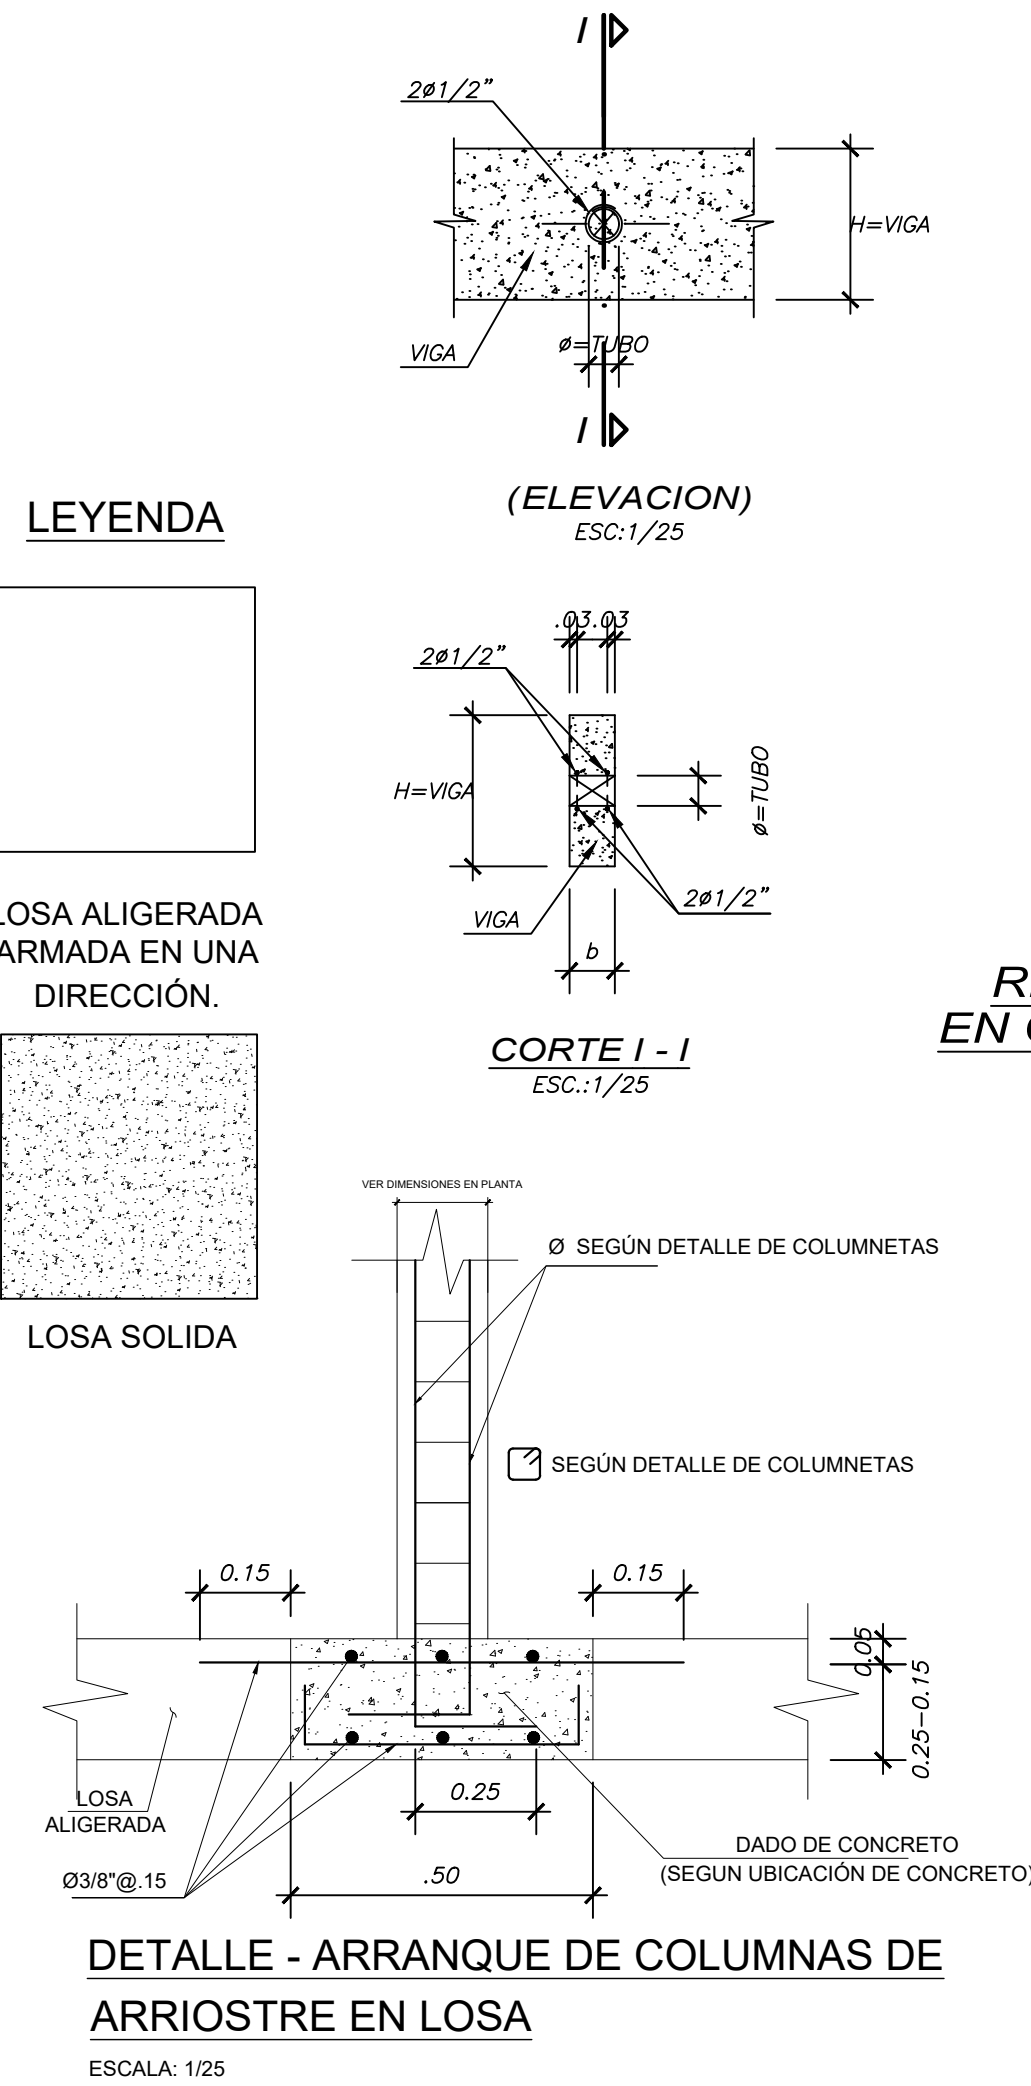

PARAMETROS SISMO - RESISTENTES

- SISTEMA ESTRUCTURAL :
X-X MUROS DE ALBAÑILERÍA CONFINADA
Y-Y MUROS DE ALBAÑILERÍA CONFINADA
- PERÍODO FUNDAMENTAL DE VIBRACIÓN :
Tp = 0.10 seg
- PARÁMETROS DE FUERZA SÍSMICA
Z = 0.45 , U = 1.0 , S = 1.20 , Tp = 0.90 seg ,
Tl = 1.6 seg , Ro = 3 Ip = 1.00 Ia = 1.00 Ct = 60
- DESPLAZAMIENTOS MÁXIMOS
AZOTEA : Dx = 0.72 cms Dy = 0.08 cms
MÁXIMA DISTORSION : Drx = 0.003 Dry = 0.0003
- JUNTA SISMICA
S = 5 cms (Altura del Azotea 8.10 m)

SOBRECARGAS

ESCALERA	200 Kg/cm2
ENTREPISO	200 Kg/cm2
AZOTEA	100 Kg/cm2

- TIPO DE SUELO :
Arena pobremente graduada (SP)
- ASENTAMIENTO MÁXIMO PERMITIDO : 2.54 cms

Tapa sanitaria hermética
removible sobreelevada
con respecto al N.P.T

Electrobomba 0.5 HP

N.P.T

Muro de protección
de ladrillo de soga

V = 1100 lt

Válvula check
de Pie

Solado de concreto fc 100 kg/cm2.

TANQUE CISTERNA

PREFABRICADO DE PVC
ESCALA : 1/25

PROYECTO:

VIVIENDA UNIFAMILIAR

UBICACIÓN :

URBANIZACIÓN CAMPESTRE LOMA BLANCA Mz. M - Lote 15 - PIURA

PROPIETARIO:

Sr. PEREYRA FARIAS JAIME DOMINGO

DNI: 02609435

Sra. CABREJOS CARBONEL DORALIZA DAMINA ELENA

DNI: 02622737

DIBUJO : JLAY

RESPONSABLE : ARQ. RENZO IZQUIERDO

ESCALA : 1 / 50


FECHA : MAYO 2026

TITULO DE LÁMINA:


ESTRUCTURAS
ALIGERADO, ESCALERA, CISTERNA Y DETALLES

Nº LÁMINA:

E-03

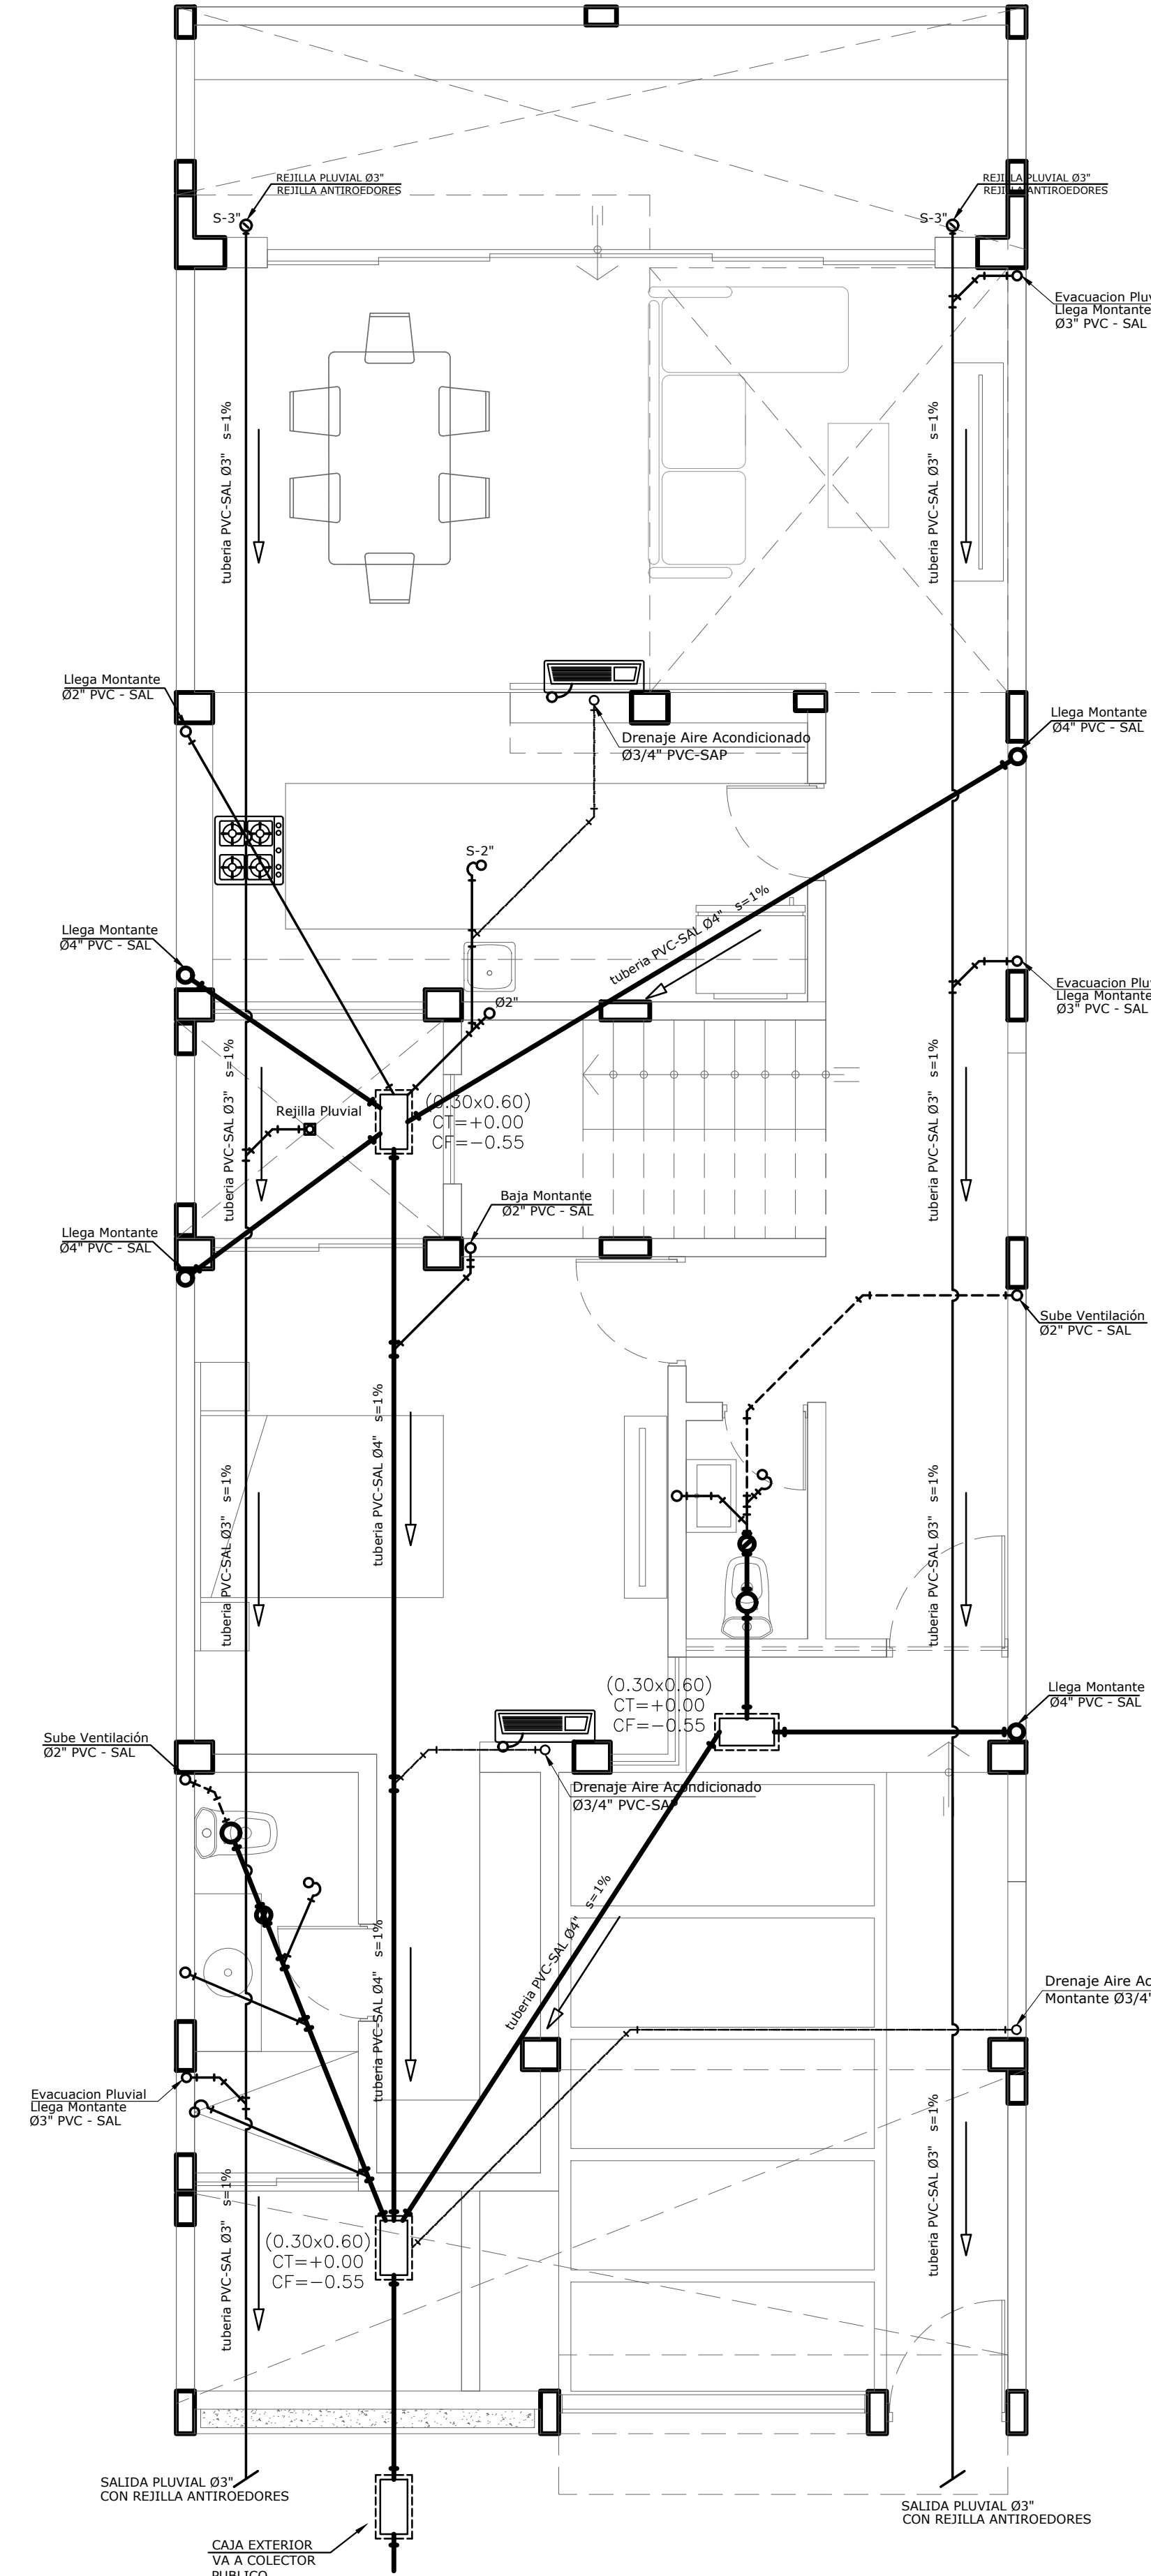


PLANTA PRIMER PISO
ESC:1/50

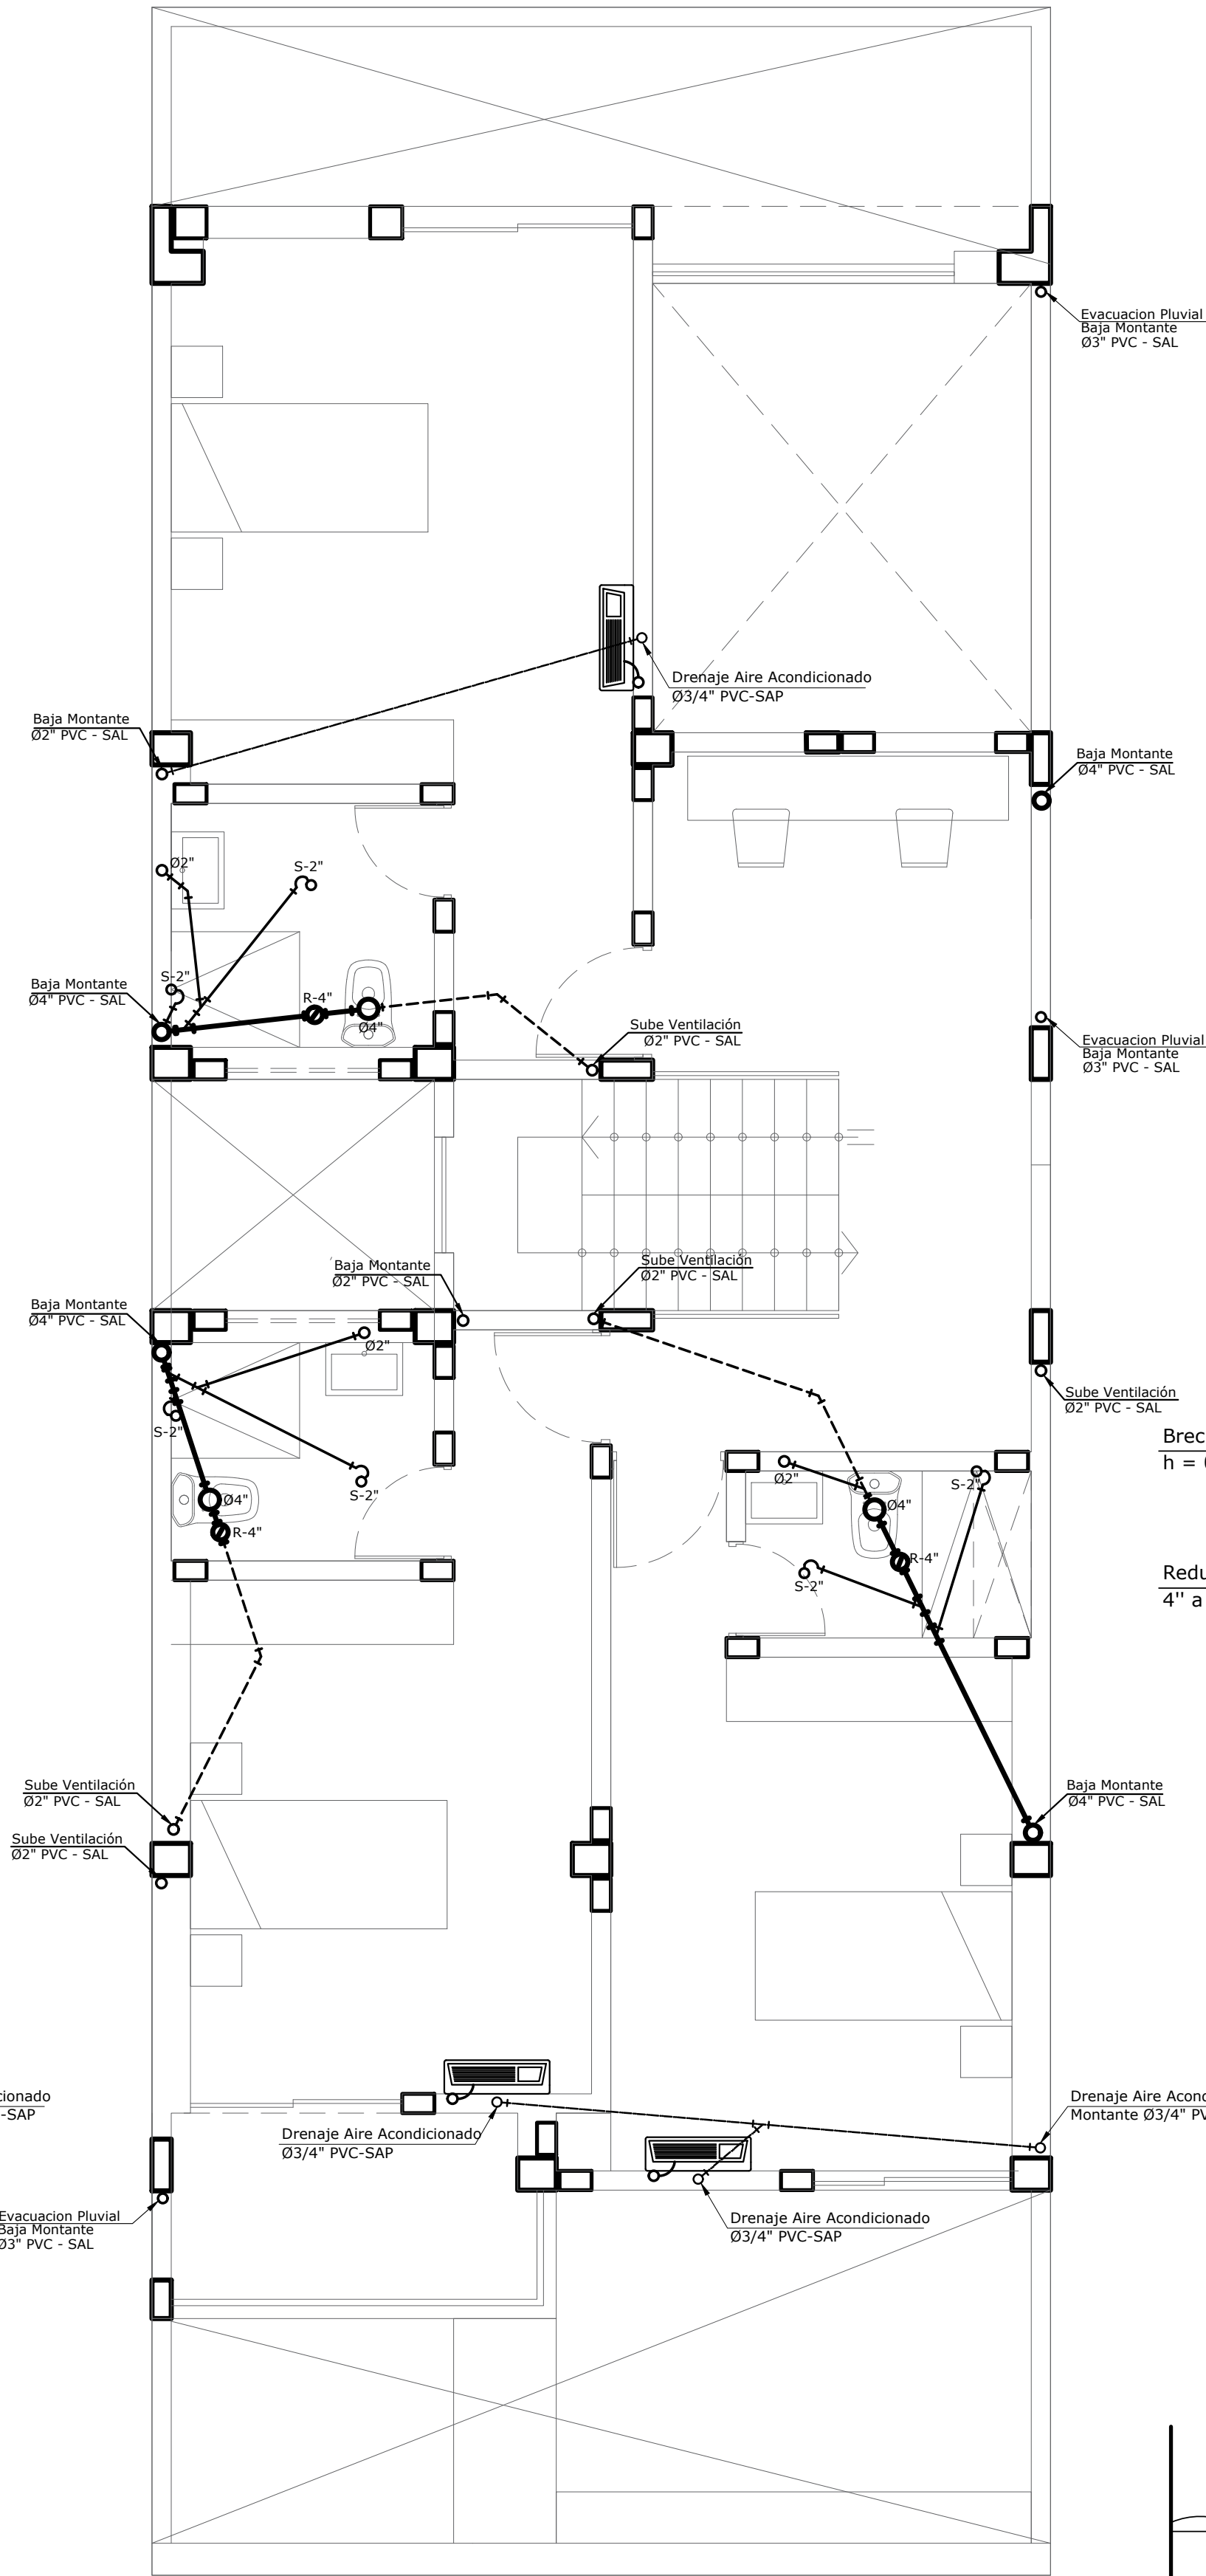


PLANTA SEGUNDO PISO
ESC:1/50

LEYENDA RED DE DESAGÜE	
SÍMBOLO	DESCRIPCION
	RED DE DESAGUE PVC-SAP Ø 4"
	RED DE DESAGUE PVC-SAP Ø 2"
	TUBERIA DE VENTILACION Ø 2" PVC- SAL
	SUMIDERO
	CAJA DE REGISTRO
	REGISTRO ROSCADO DE BRONCE
	"Y" SIMPLE
	"Y" DOBLE
	CODO 45°
S = 1%	PENDIENTE DE LA TUBERIA

SISTEMA ELECTRICO AUTOMATICO

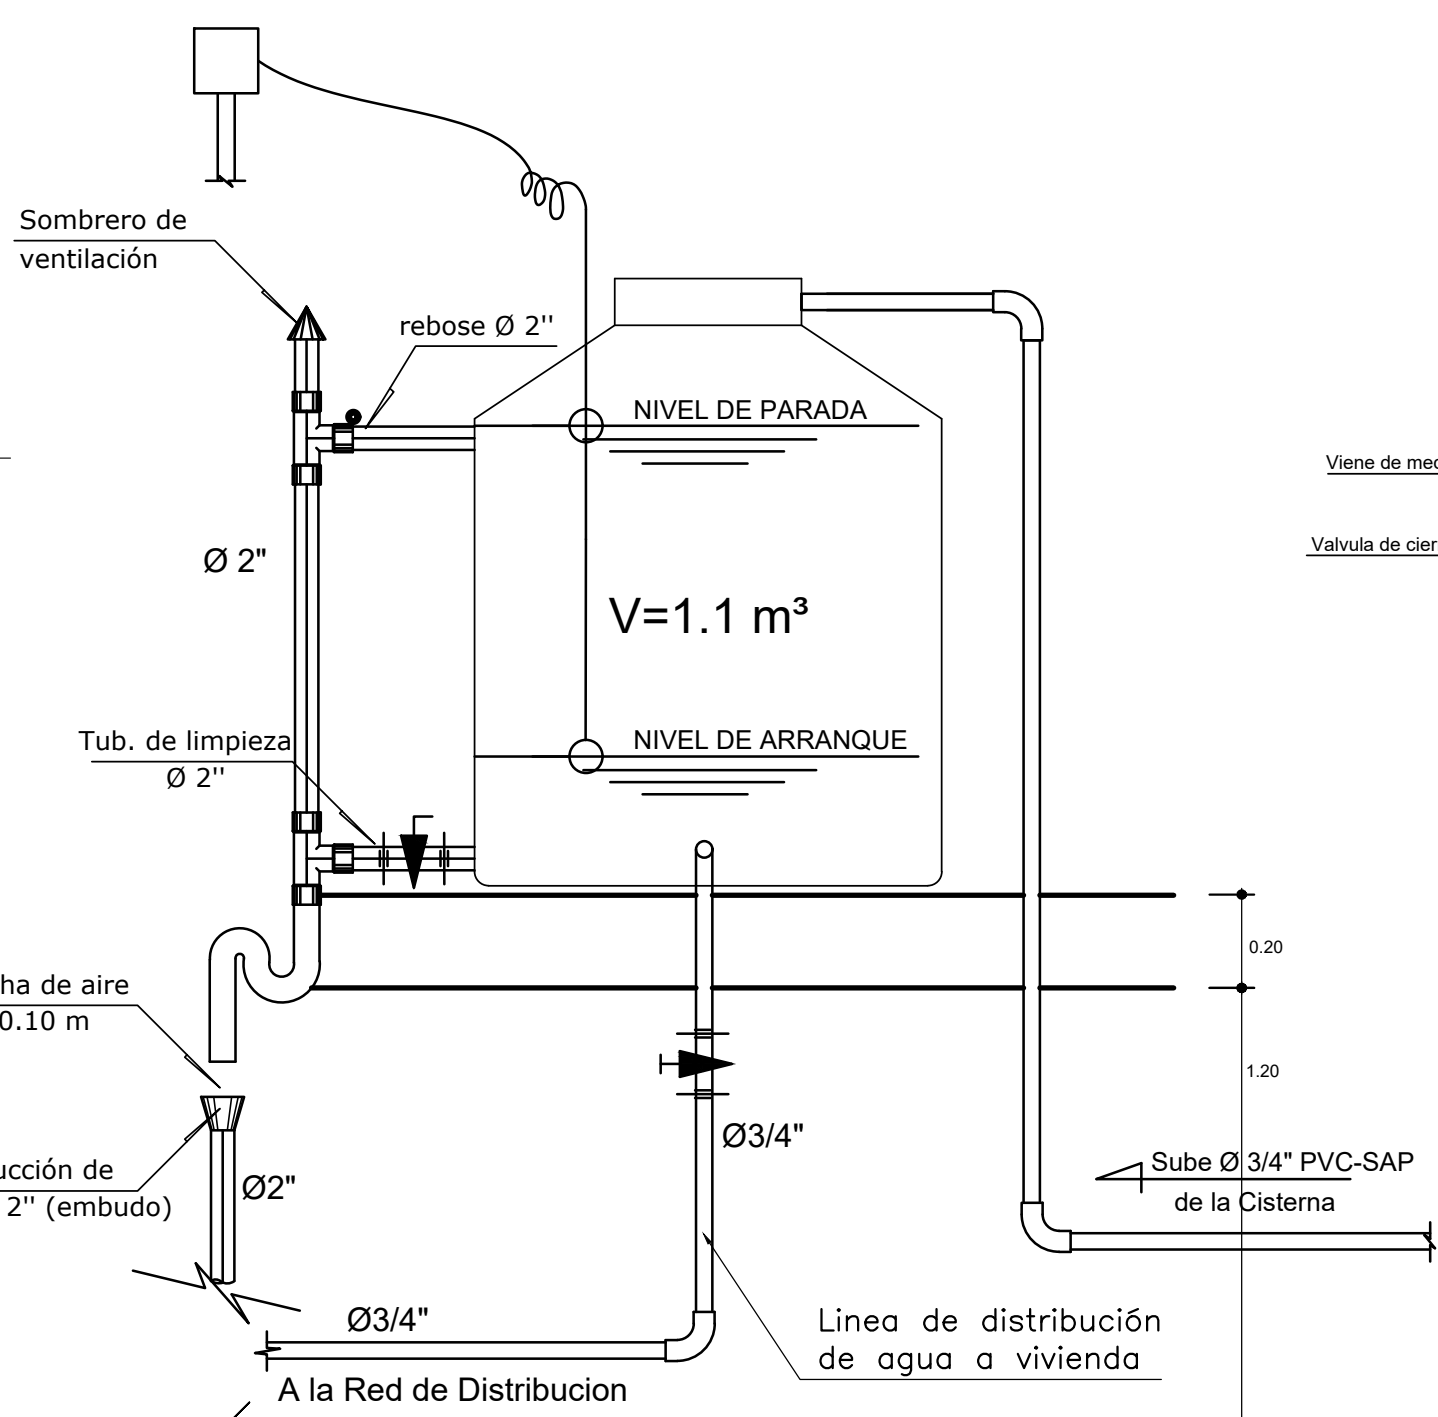


TANQUE ELEVADO
ESC 1/25

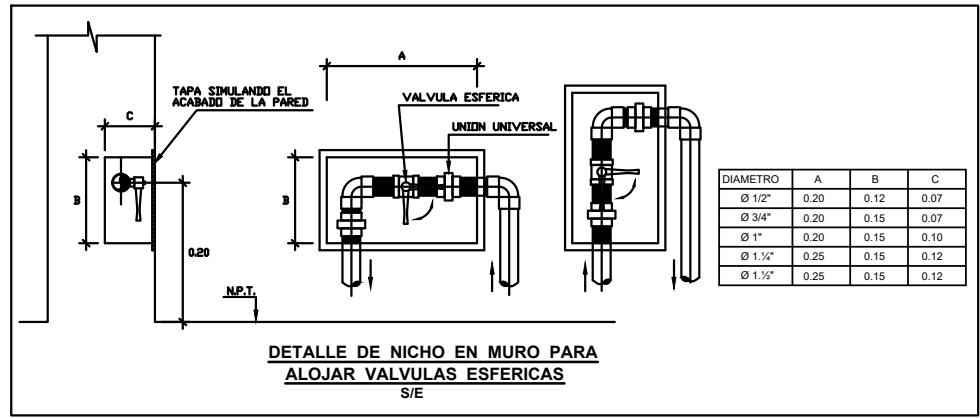


ESPECIFICACIONES TECNICAS

RED DE DESAGUE:


- LAS TUBERIAS A EMPLEARSE EN LAS REDES SERAN DE PVC TIPO LIVIANO PVC-SAL CON ACCESORIOS DEL MISMO MATERIAL, CON UNIONES SELLADOS CON PEGAMENTO ESPECIAL
- LAS CAJAS DE REGISTROS SE INSTALARAN EN LUGARES INDICADOS EN LOS PLANOS, SERAN DE ALBANILERIA IMPERMEABILIZADOS, CON MARCO Y TAPA DE FIERRO FUNDIDO Y/O CON EL MISMO MATERIAL DEL PISO TERMINADO. EN DIMENSIONES INDICADAS.
- LOS REGISTROS ROSCADOS SERAN DE BRONCE, CON TAPA ROSCADA HERMETICA E IRAN FIJADOS A LA CABEZA DEL ACCESORIO CORRESPONDIENTE .
- LAS TUBERIAS Y ACCESORIOS PARA DESAGUE Y VENTILACION, SERAN DE PVC RIGIDA SAP DE UNION A SIMPLE PRESION, PESADA Y/O LIVIANA CON PEGAMENTO O CEMENTO SOLVENTE PARA TUBERIA DE PVC. SEGUN NORMAS.
- PENDIENTES PARA TUBERIAS DE DESAGUE:
 - Ø 2" = 1.5 ‰ (MINIMO)
 - Ø 4" = 1.0 ‰ (MINIMO)
 - Ø 6" = 1.0 ‰ (MINIMO)
- LAS TUBERIAS DE VENTILACION SE PROLONGARAN 40cm. POR ENCIMA DEL N.T.T. Y LLEVARAN SOMBRERO DE VENTILACION.
- LAS TUBERIAS DE DESAGUE SERAN PROBADAS A TUBO LLENO DE AGUA DURANTE 24 HORAS SIN PRESENTAR PERDIDA DE NIVEL

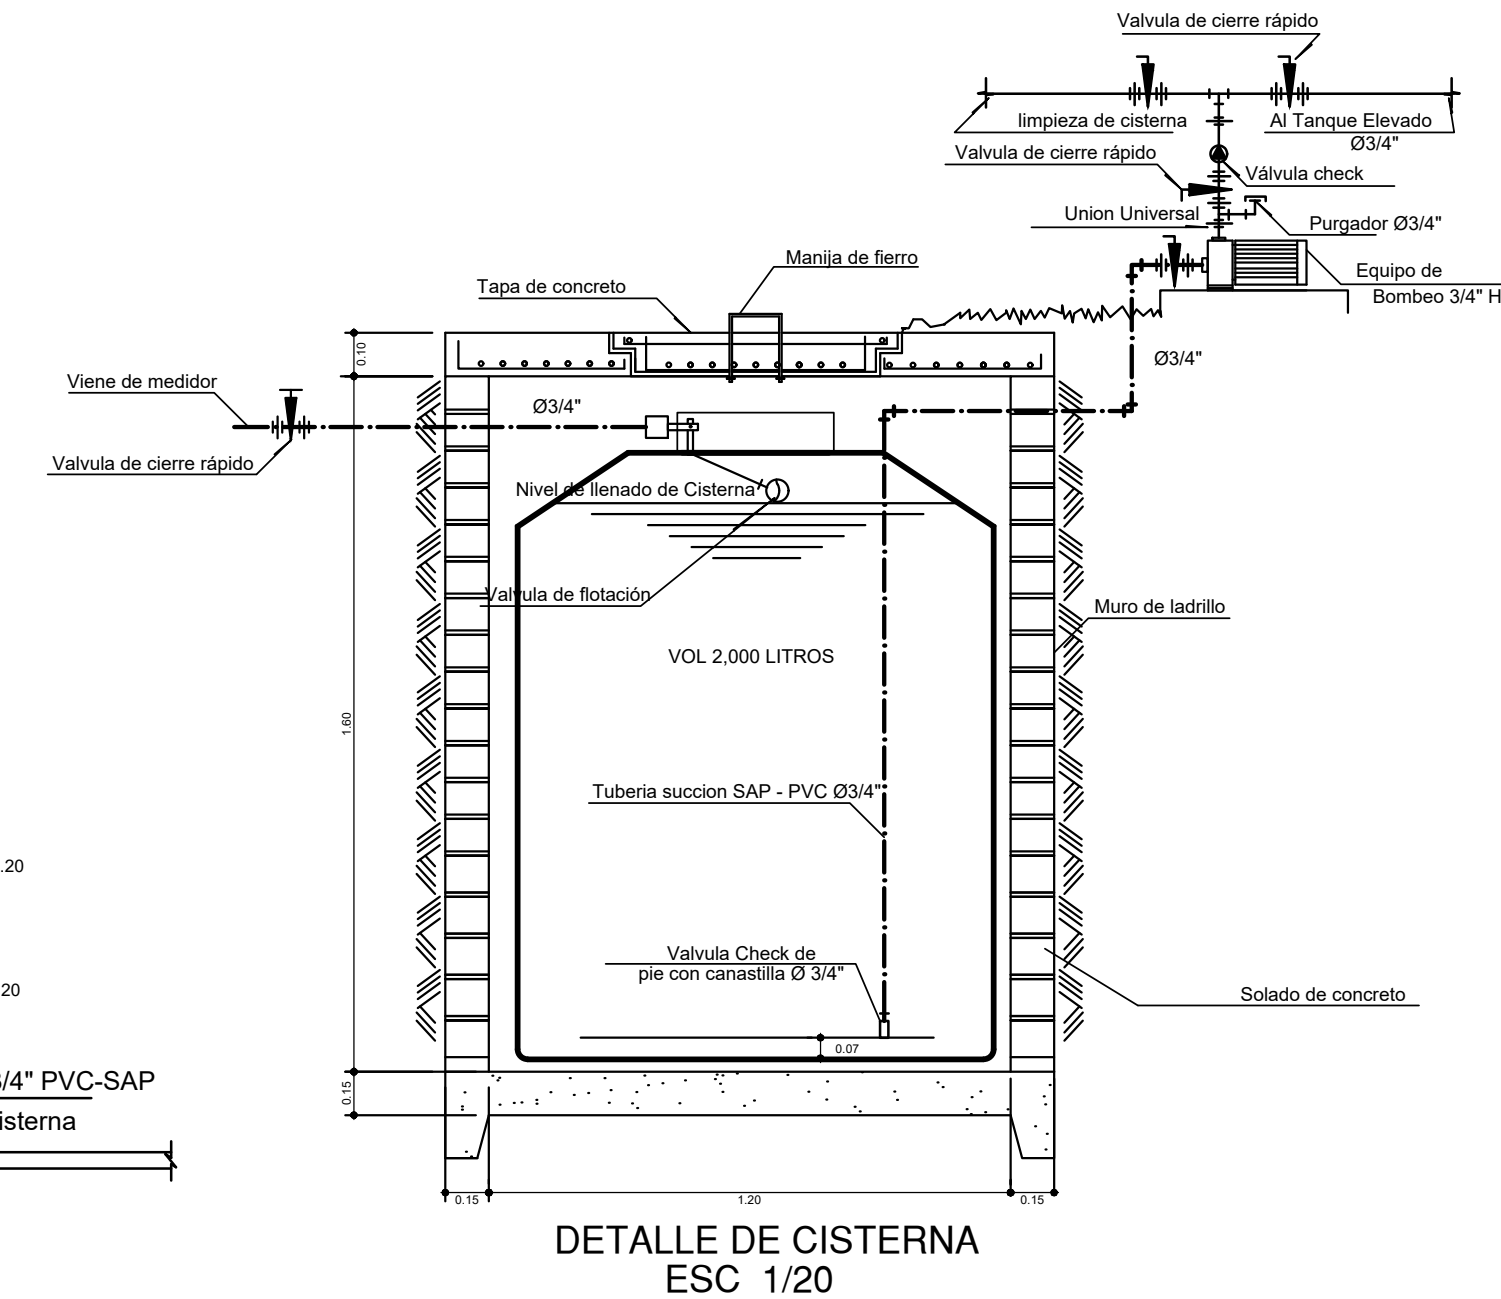

DETALLE DE CISTERNA
ESC 1/20

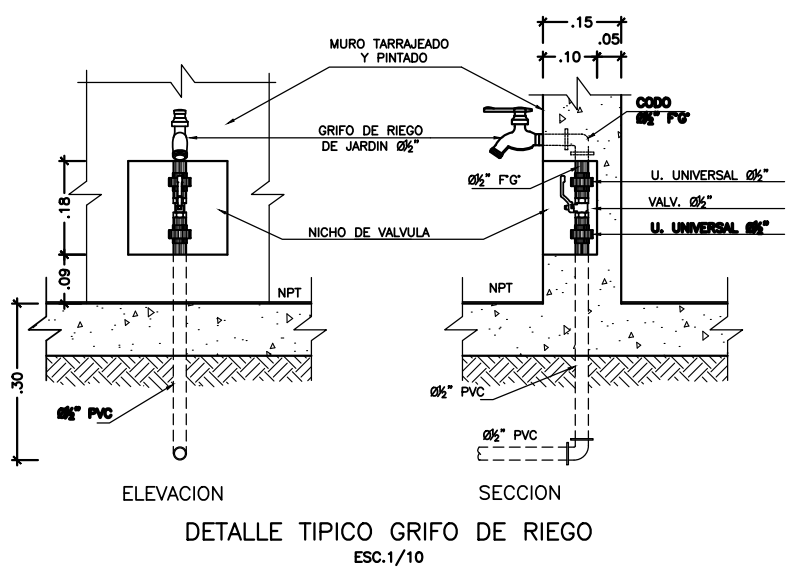

DETALLE TÍPICO GRIFO DE RIEGO
ESC:1/10

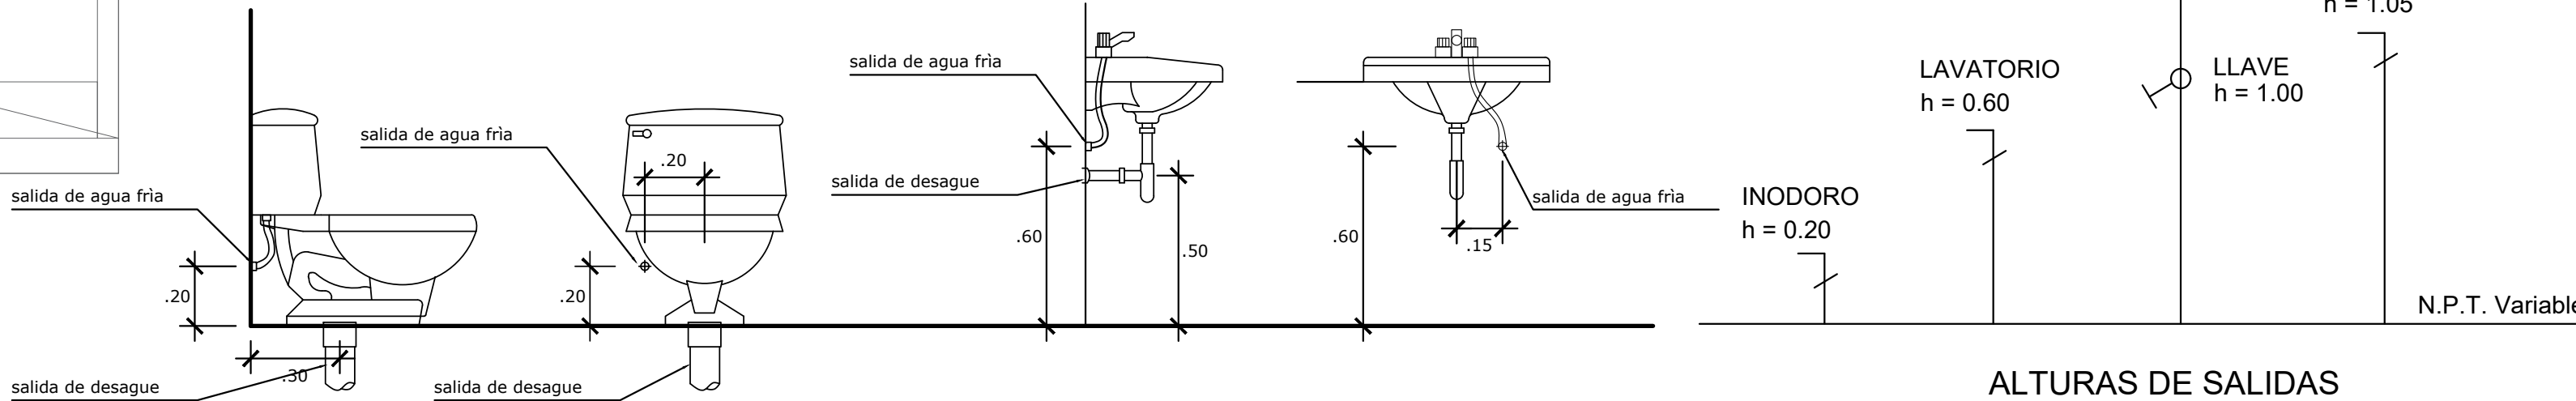

DETALLE DE SALIDAS DE AGUA Y DESAGUE EN SANITARIOS
ESC 1/20

ALTURAS DE SALIDAS
PARA APARATOS SANITARIOS

PROYECTO: VIVIENDA UNIFAMILIAR	UBICACIÓN :	DIBUJO : JLAY
	URB. MIRAFLORES BOULEVARD PARK PLAZA Mz. AN - Lote 18 - II ETAPA - CASTILLA	RESPONSABLE : ARQ. RENZO IZQUIERDO
	PROPIETARIO:	ESCALA : 1 / 50
	Sra. ROSSEMERY YANIRE FERNÁNDEZ ROJAS DNI: 80366589	FECHA : JULIO 2026

TÍTULO DE LÁMINA: INSTALACIONES SANITARIAS RED DE DESAGÜE Y EVACUACIÓN PLUVIAL - 1er y 2do PISO

Nº LÁMINA: IS-01




LEYENDA RED DE DESAGÜE	
SÍMBOLO	DESCRIPCION
	RED DE DESAGUE PVC-SAP Ø 4"
	RED DE DESAGUE PVC-SAP Ø 2"
	TUBERIA DE VENTILACION Ø 2" PVC- SAL
	SUMIDERO
	CAJA DE REGISTRO
	REGISTRO ROSCADO DE BRONCE
	"Y" SIMPLE
	"Y" DOBLE
	CODO 45°
S = 1%	PENDIENTE DE LA TUBERIA

- LAS TUBERIAS A EMPLEARSE EN LAS REDES SERAN DE PVC TIPO LIVIANO PVC-SAL CON ACCESORIOS DEL MISMO MATERIAL, CON UNIONES SELLADOS CON PEGAMENTO ESPECIAL
- LAS CAJAS DE REGISTROS SE INSTALARAN EN LUGARES INDICADOS EN LOS PLANOS, SERAN DE ALBANILERIA IMPERMEABILIZADOS, CON MARCO Y TAPA DE FIERRO FUNDIDO Y/O CON EL MISMO MATERIAL DEL PISO TERMINADO. EN DIMENSIONES INDICADAS.
- LOS REGISTROS ROSCADOS SERAN DE BRONCE, CON TAPA ROSCADA HERMETICA E IRAN FIJADOS A LA CABEZA DEL ACCESORIO CORRESPONDIENTE .
- LAS TUBERIAS Y ACCESORIOS PARA DESAGUE Y VENTILACION, SERAN DE PVC RIGIDA SAP DE UNION A SIMPLE PRESION, PESADA Y/O LIVIANA CON PEGAMENTO O CEMENTO SOLVENTE PARA TUBERIA DE PVC. SEGUN NORMAS.
- PENDIENTES PARA TUBERIAS DE DESAGUE:
 - Ø 2" = 1.5 % (MINIMO)
 - Ø 4" = 1.0 % (MINIMO)
 - Ø 6" = 1.0 % (MINIMO)
- LAS TUBERIAS DE VENTILACION SE PROLONGARAN 40cm. POR ENCIMA DEL N.T.T. Y LLEVARAN SOMBRERO DE VENTILACION.

PRUEBAS:

- LAS TUBERIAS DE DESAGUE SERAN PROBADAS A TUBO LLENO DE AGUA DURANTE 24 HORAS SIN PRESENTAR PERDIDA DE NIVEL

Detalle de Tapa Ciega
Escala: 1 /25

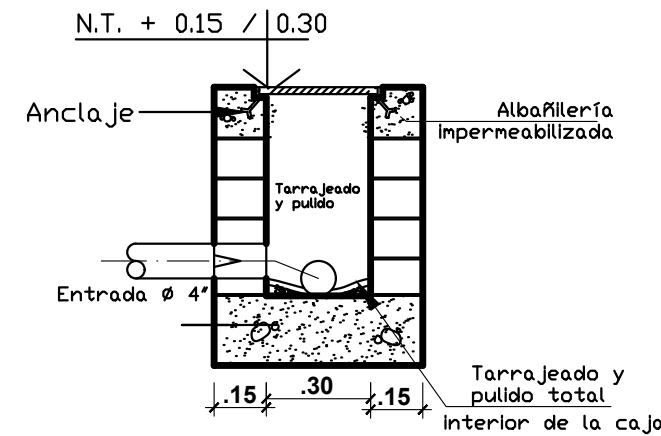

Corte A - A

N.T. + 0.15 / 0.30

Tapa y marco de P* F 10"x24"

Albañilería impermeabilizada

C.F. -0.455

C.F. -0.45

Salida Ø 4"

Terrojeado pulido total interior de la


.60

.20

.15 .60 .15

Corte B - B
Detalle de Caja de desagüe
Escala: 1 /25


DETALLE DE MONTANTE
DE EVACUACION PLUVIAL
S/E

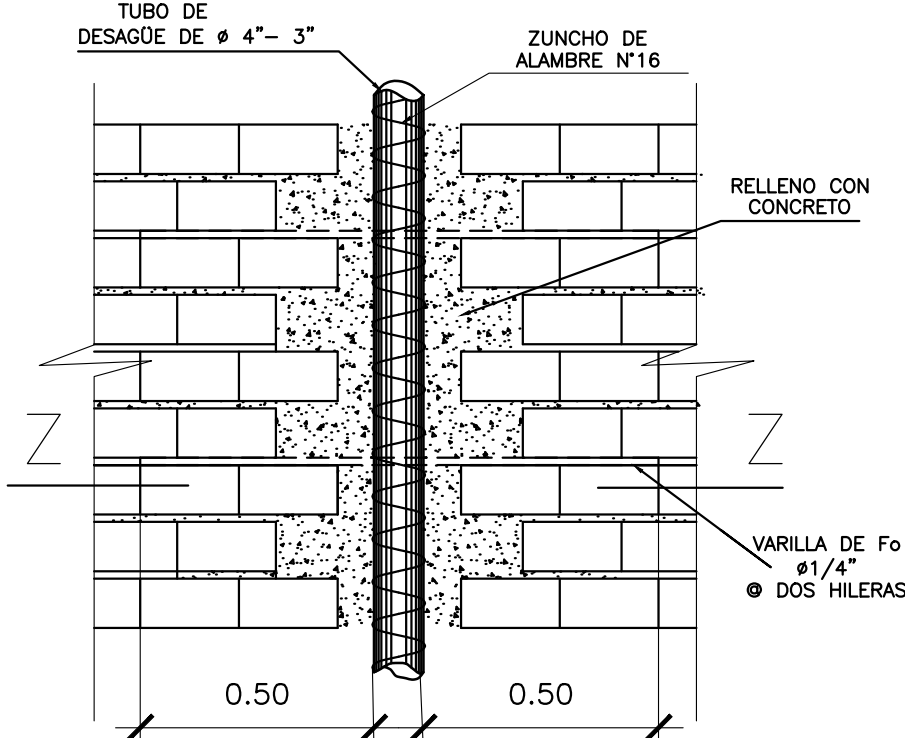


DETALLE DE REFUERZO
PARA TUBERIA DE $\phi 4"$
ESC. 1/20

CORTE Z-Z
ESC. 1/20

DETALLE DE REJILLA
DE EVACUACION PLUVIAL
S/E

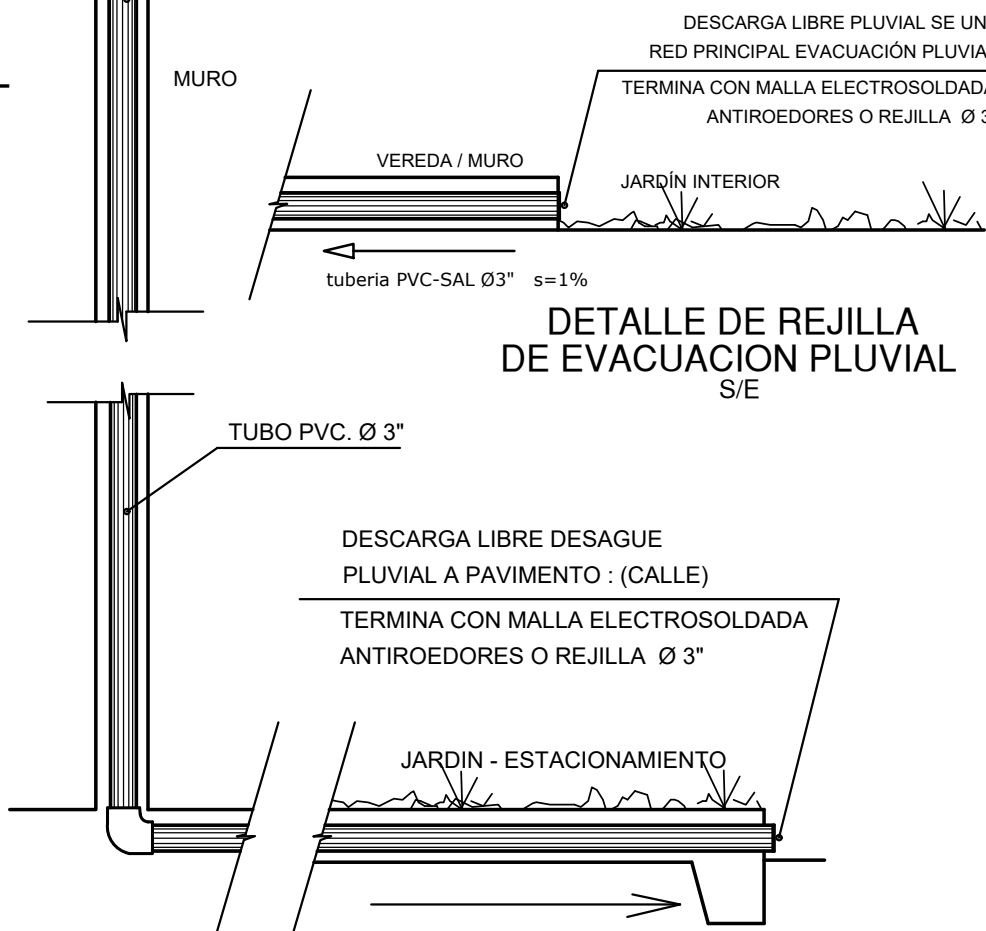

REFUERZO TIPICO DE VIGUETAS
EN ZONA DE CRUCE DE TUBERIAS


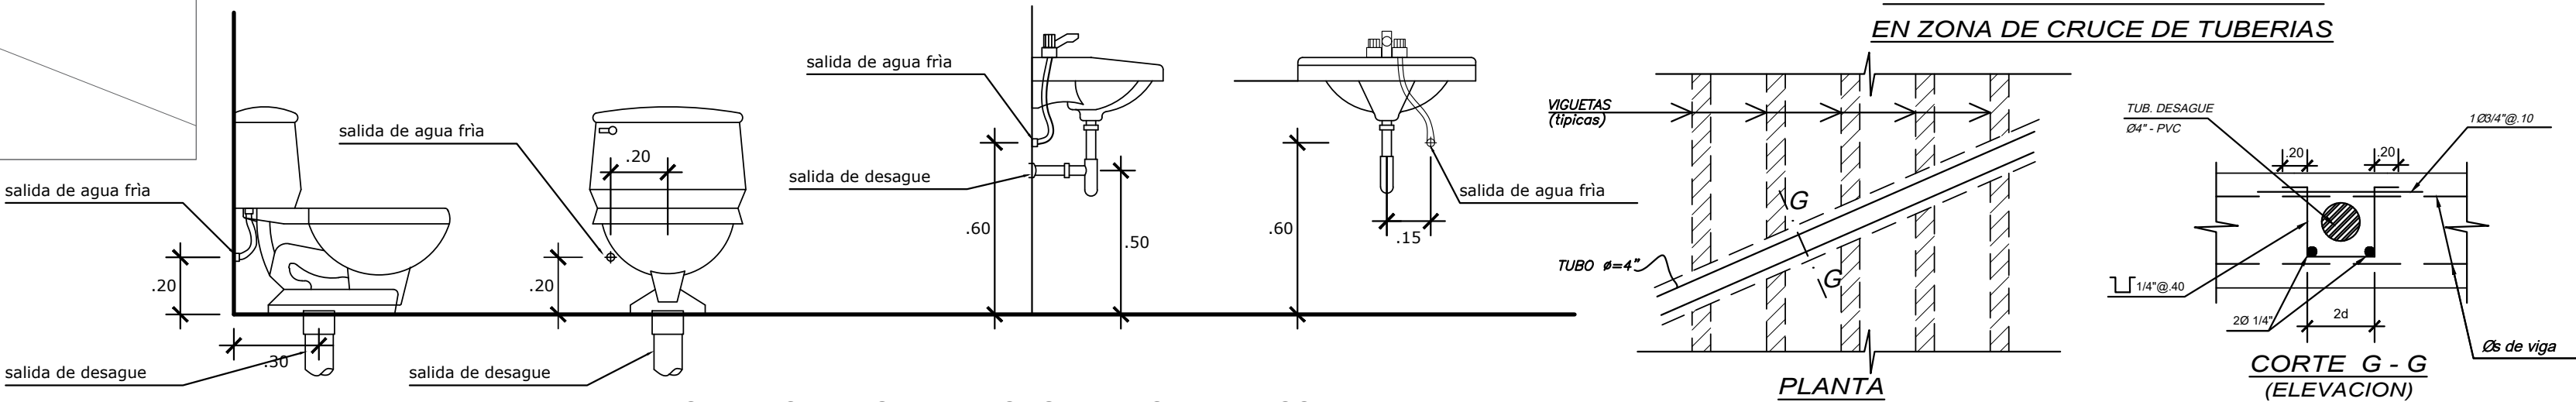


DETALLE DE SALIDAS DE AGUA Y DESAGUE EN SANITARIOS
ESC 1/20

PROYECTO:	UBICACIÓN :	DIBUJO :	TÍTULO DE LÁMINA:
	URB. MIRAFLORES BOULEVARD PARK PLAZA Mz. AN - Lote 18 - II ETAPA - CASTILLA	RESPONSABLE :	
	PROPIETARIO:	ESCALA :	
	Sra. ROSSEMERY YANIRE FERNÁNDEZ ROJAS DNI: 80366589	FECHA :	






Nº LÁMINA:

IS-02

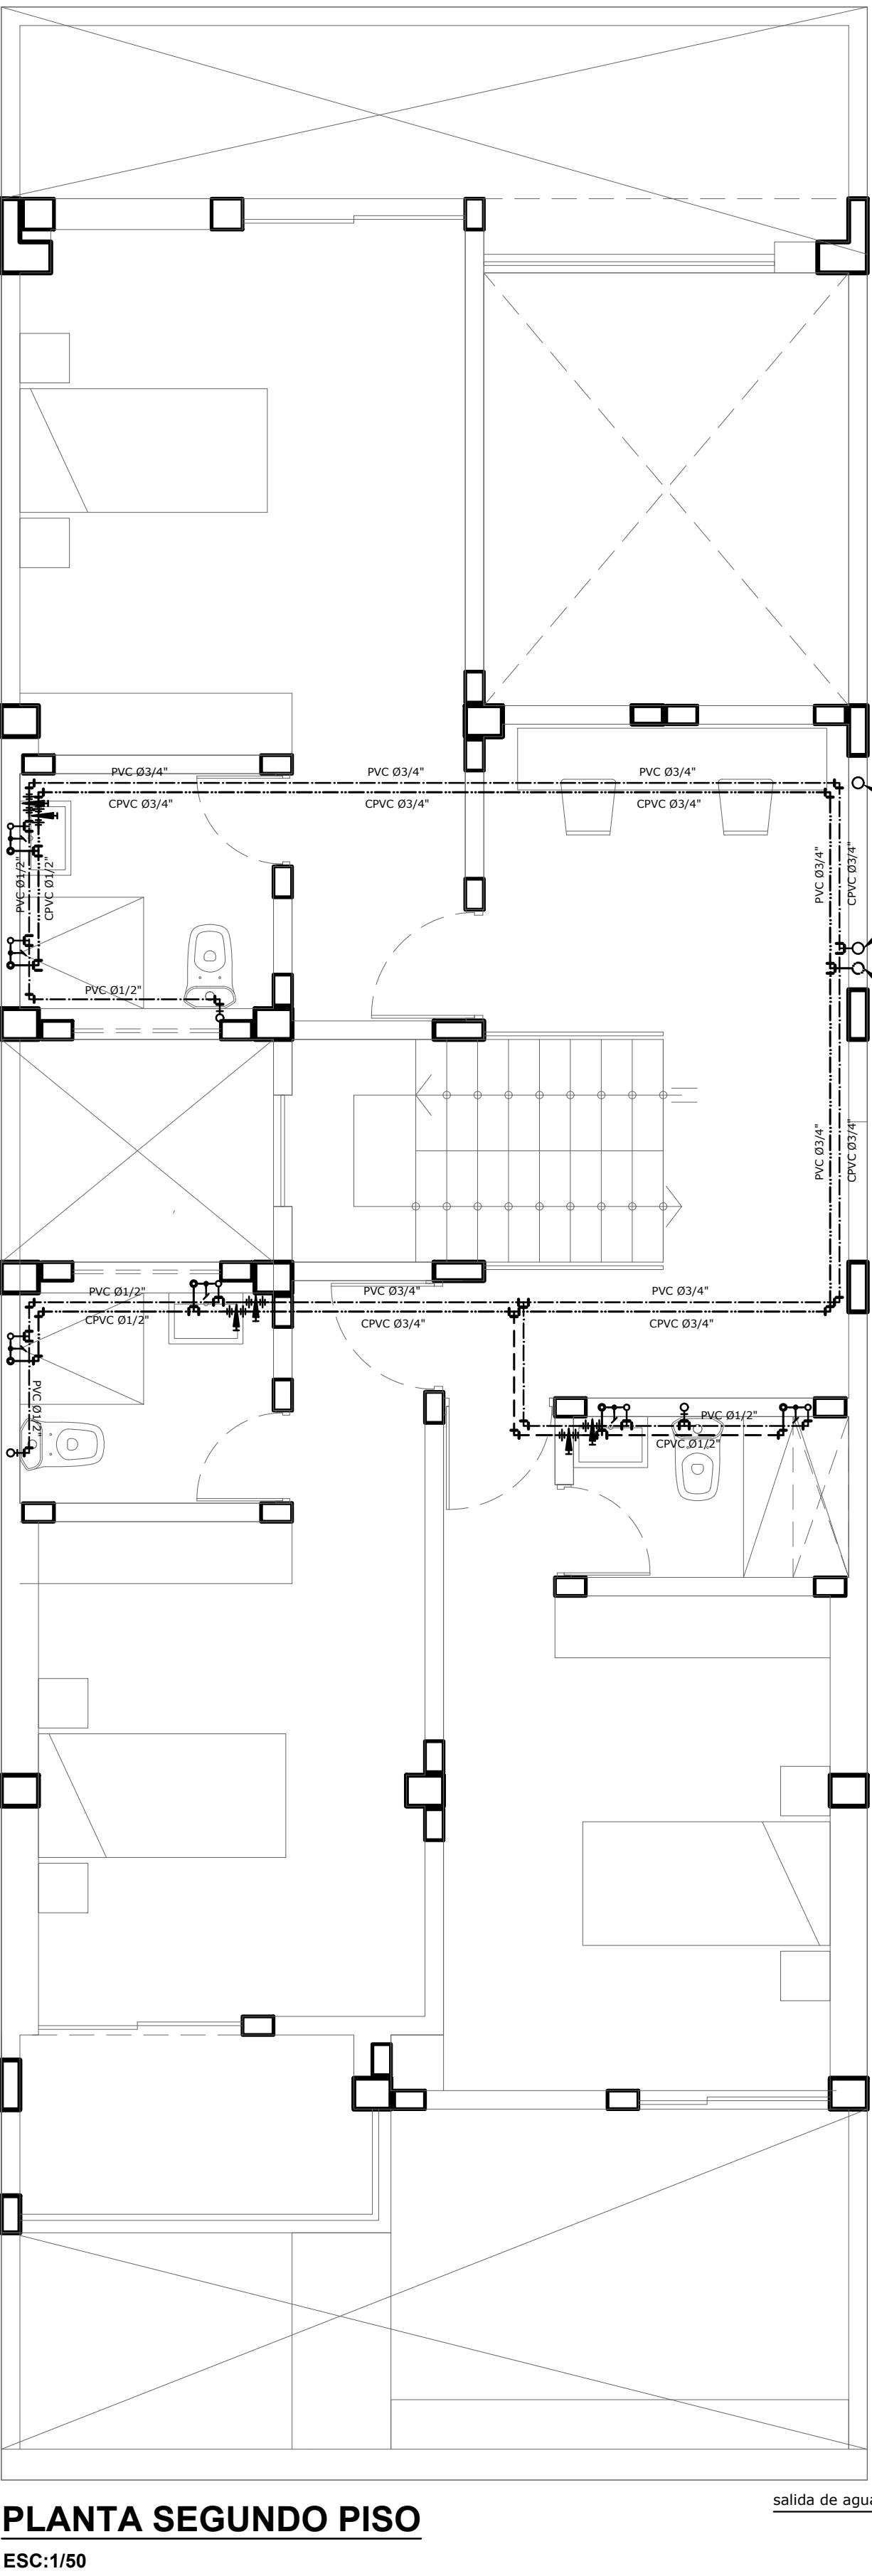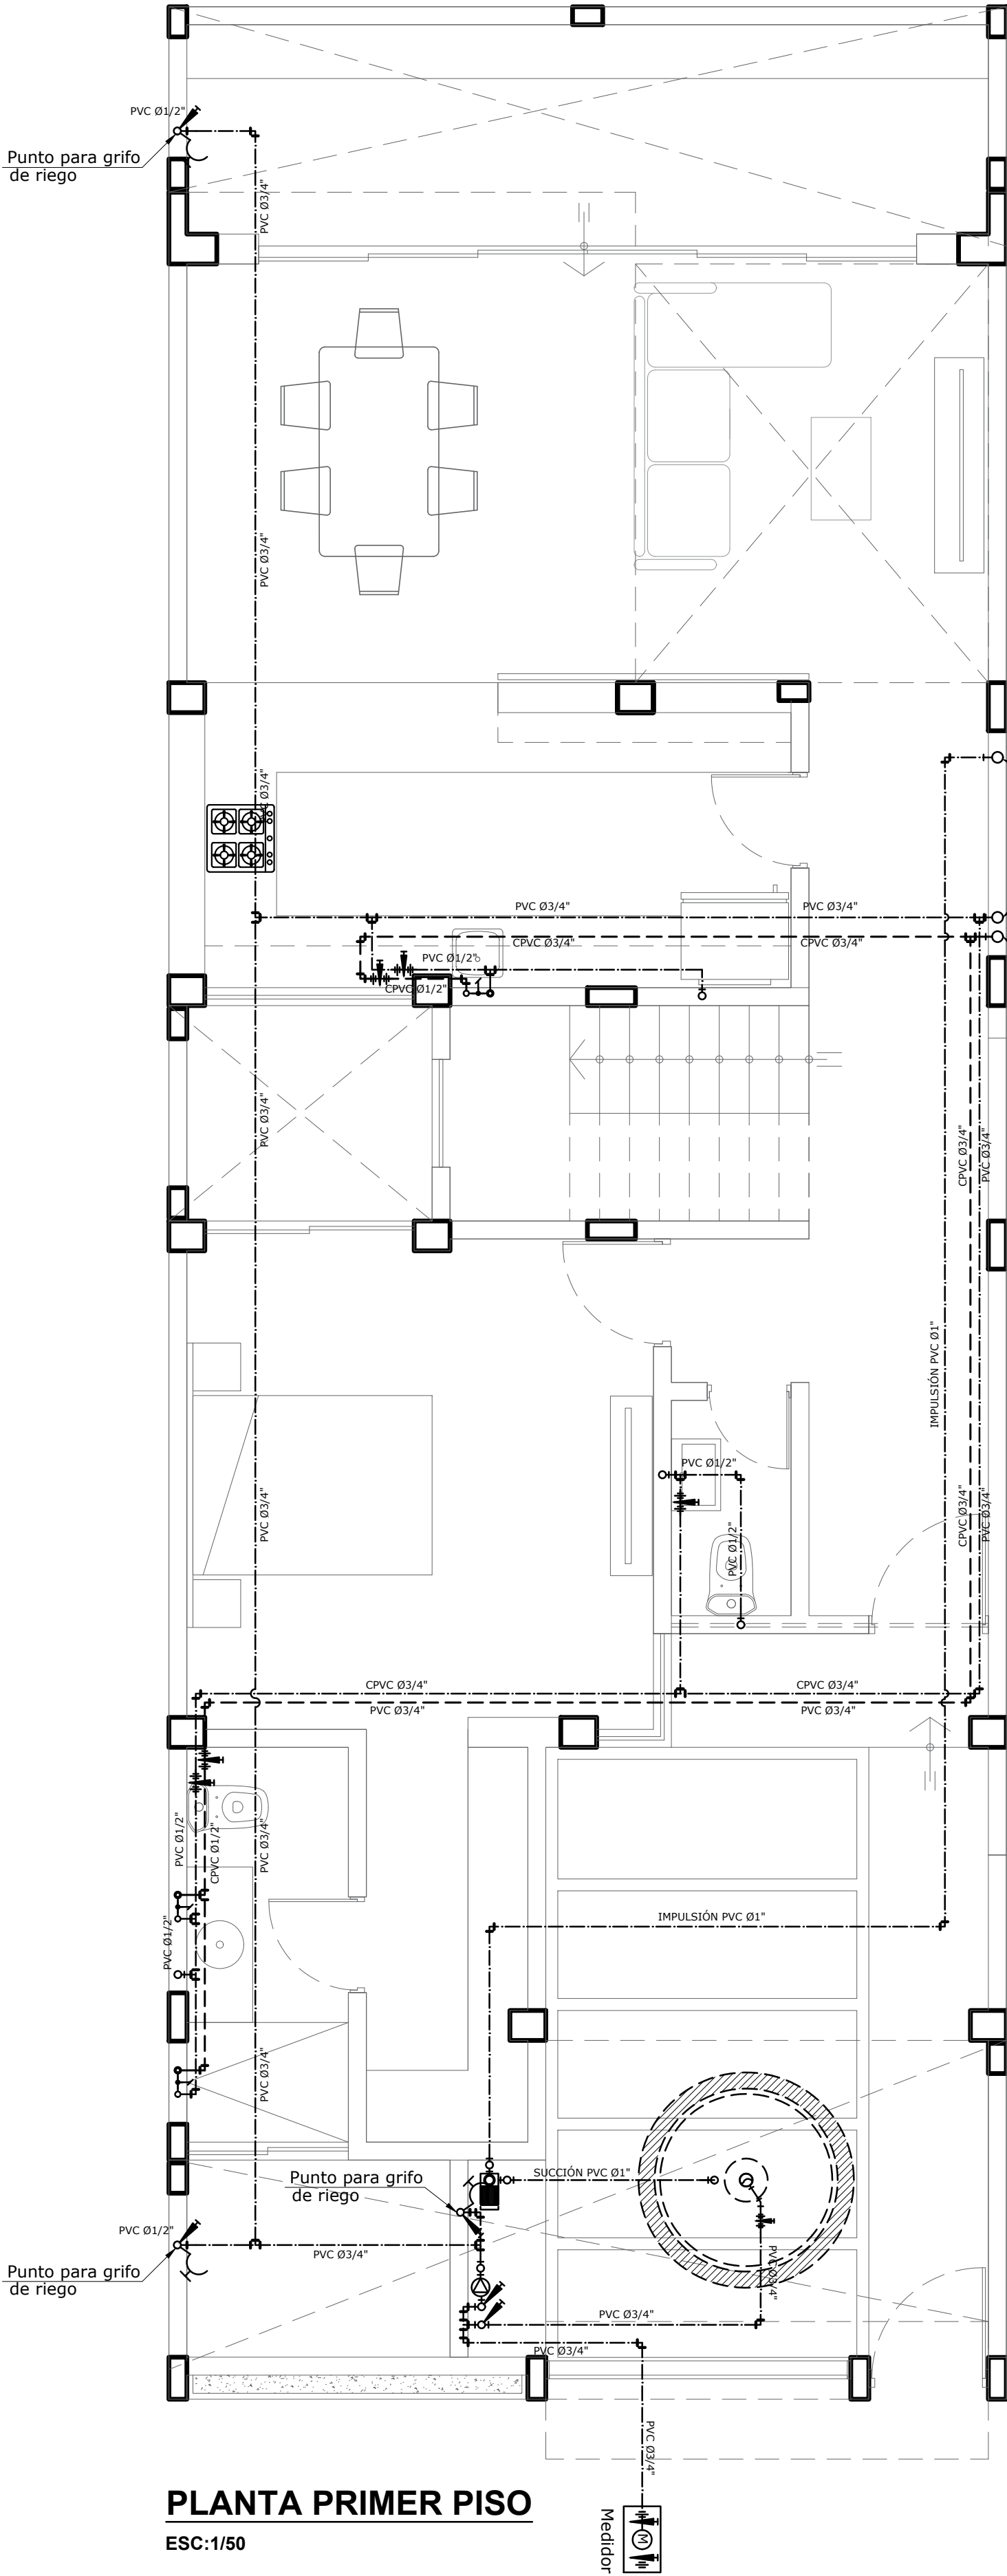


LEYENDA RED DE DESAGÜE	
SÍMBOLO	DESCRIPCION
	RED DE DESAGUE PVC-SAP Ø 4"
	RED DE DESAGUE PVC-SAP Ø 2"
	TUBERIA DE VENTILACION Ø 2" PVC- SAL
	SUMIDERO
	CAJA DE REGISTRO
	REGISTRO ROSCADO DE BRONCE
	"Y" SIMPLE
	"Y" DOBLE
	CODO 45°
S = 1%	PENDIENTE DE LA TUBERIA


ESPECIFICACIONES TECNICAS	
RED DE DESAGUE:	
- LAS TUBERIAS A EMPLEARSE EN LAS REDES SERAN DE PVC TIPO LIVIANO PVC-SAL CON ACCESORIOS DEL MISMO MATERIAL, CON UNIONES SELLADOS CON PEGAMENTO ESPECIAL	
- LAS CAJAS DE REGISTROS SE INSTALARAN EN LUGARES INDICADOS EN LOS PLANOS, SERAN DE ALBANILERIA IMPERMEABILIZADOS, CON MARCO Y TAPA DE FIERRO FUNDIDO Y/O CON EL MISMO MATERIAL DEL PISO TERMINADO. EN DIMENSIONES INDICADAS.	
- LOS REGISTROS ROSCADOS SERAN DE BRONCE, CON TAPA ROSCADA HERMETICA E IRAN FIJADOS A LA CABEZA DEL ACCESORIO CORRESPONDIENTE .	
- LAS TUBERIAS Y ACCESORIOS PARA DESAGUE Y VENTILACION, SERAN DE PVC RIGIDA SAP DE UNION A SIMPLE PRESION, PESADA Y/O LIVIANA CON PEGAMENTO O CEMENTO SOLVENTE PARA TUBERIA DE PVC. SEGUN NORMAS.	
- PENDIENTES PARA TUBERIAS DE DESAGUE:	
- Ø 2" = 1.5 ‰ (MINIMO)	
- Ø 4" = 1.0 ‰ (MINIMO)	
- Ø 6" = 1.0 ‰ (MINIMO)	
- LAS TUBERIAS DE VENTILACION SE PROLONGARAN 40cm. POR ENCIMA DEL N.T.T. Y LLEVARAN SOMBRERO DE VENTILACION.	
PRUEBAS:	
- LAS TUBERIAS DE DESAGUE SERAN PROBADAS A TUBO LLENO DE AGUA DURANTE 24 HORAS SIN PRESENTAR PERDIDA DE NIVEL	

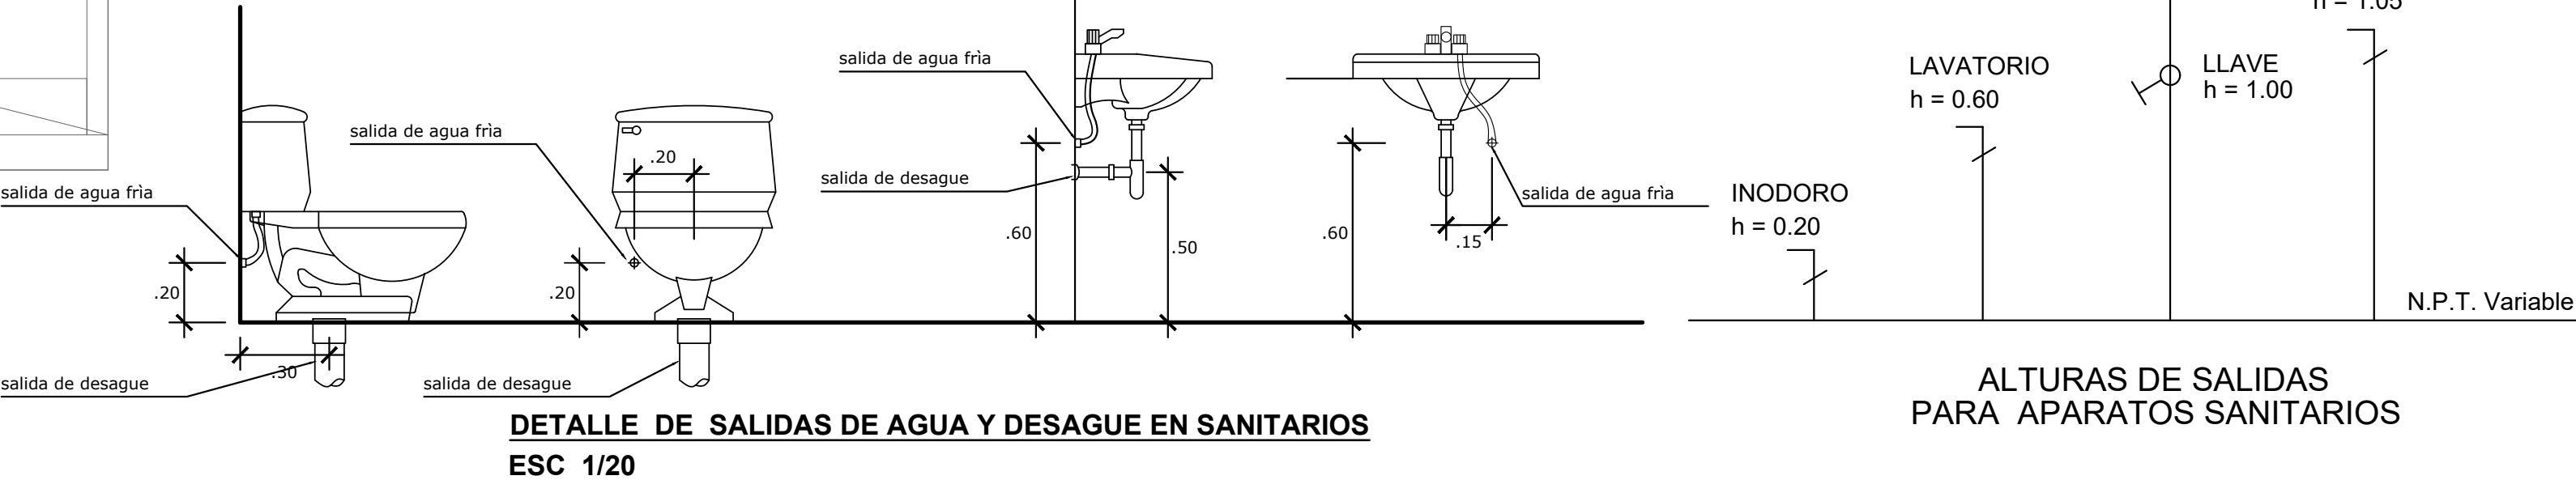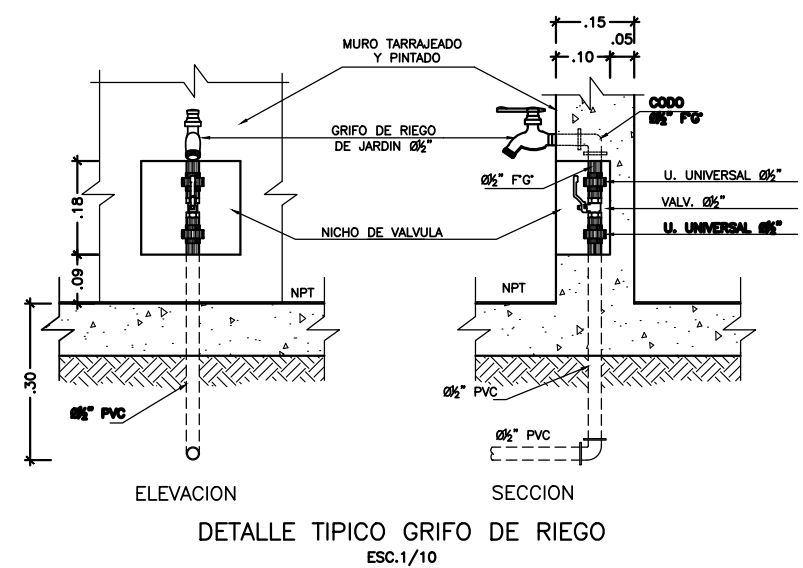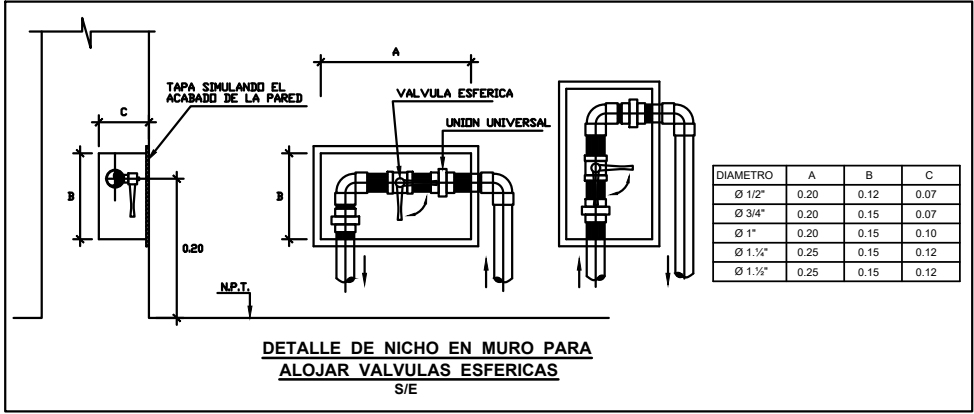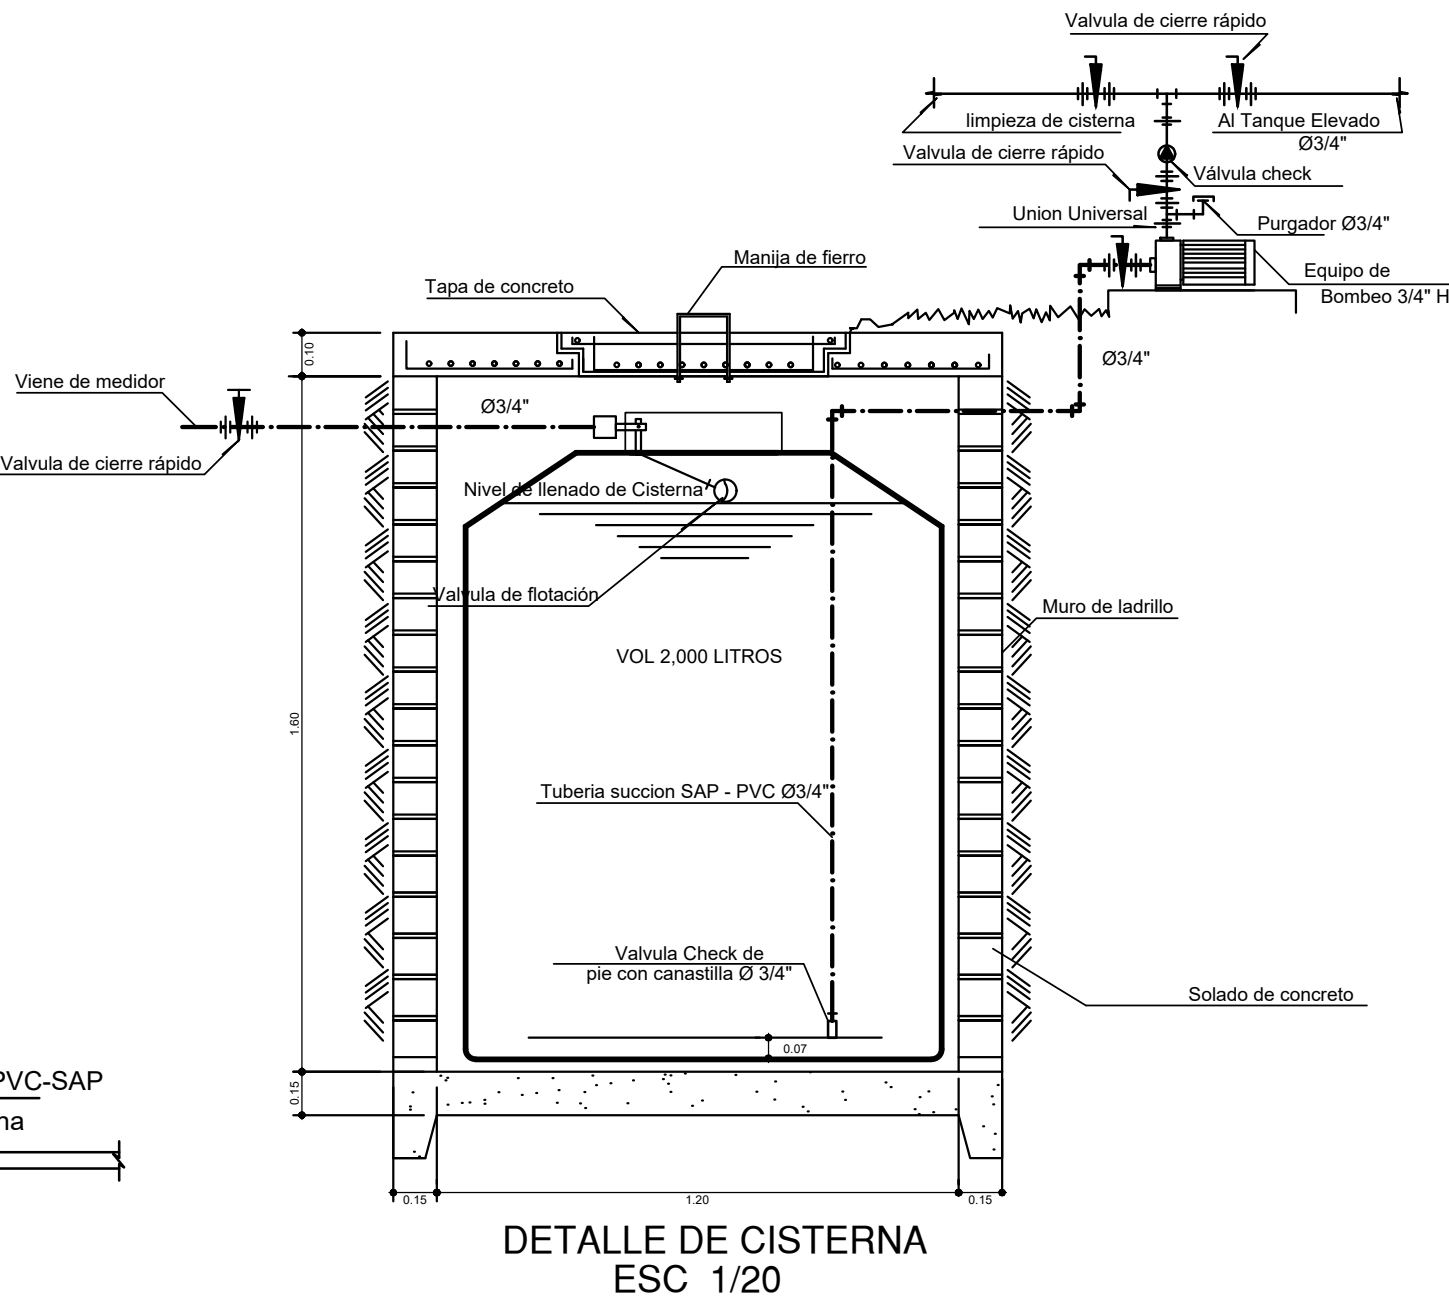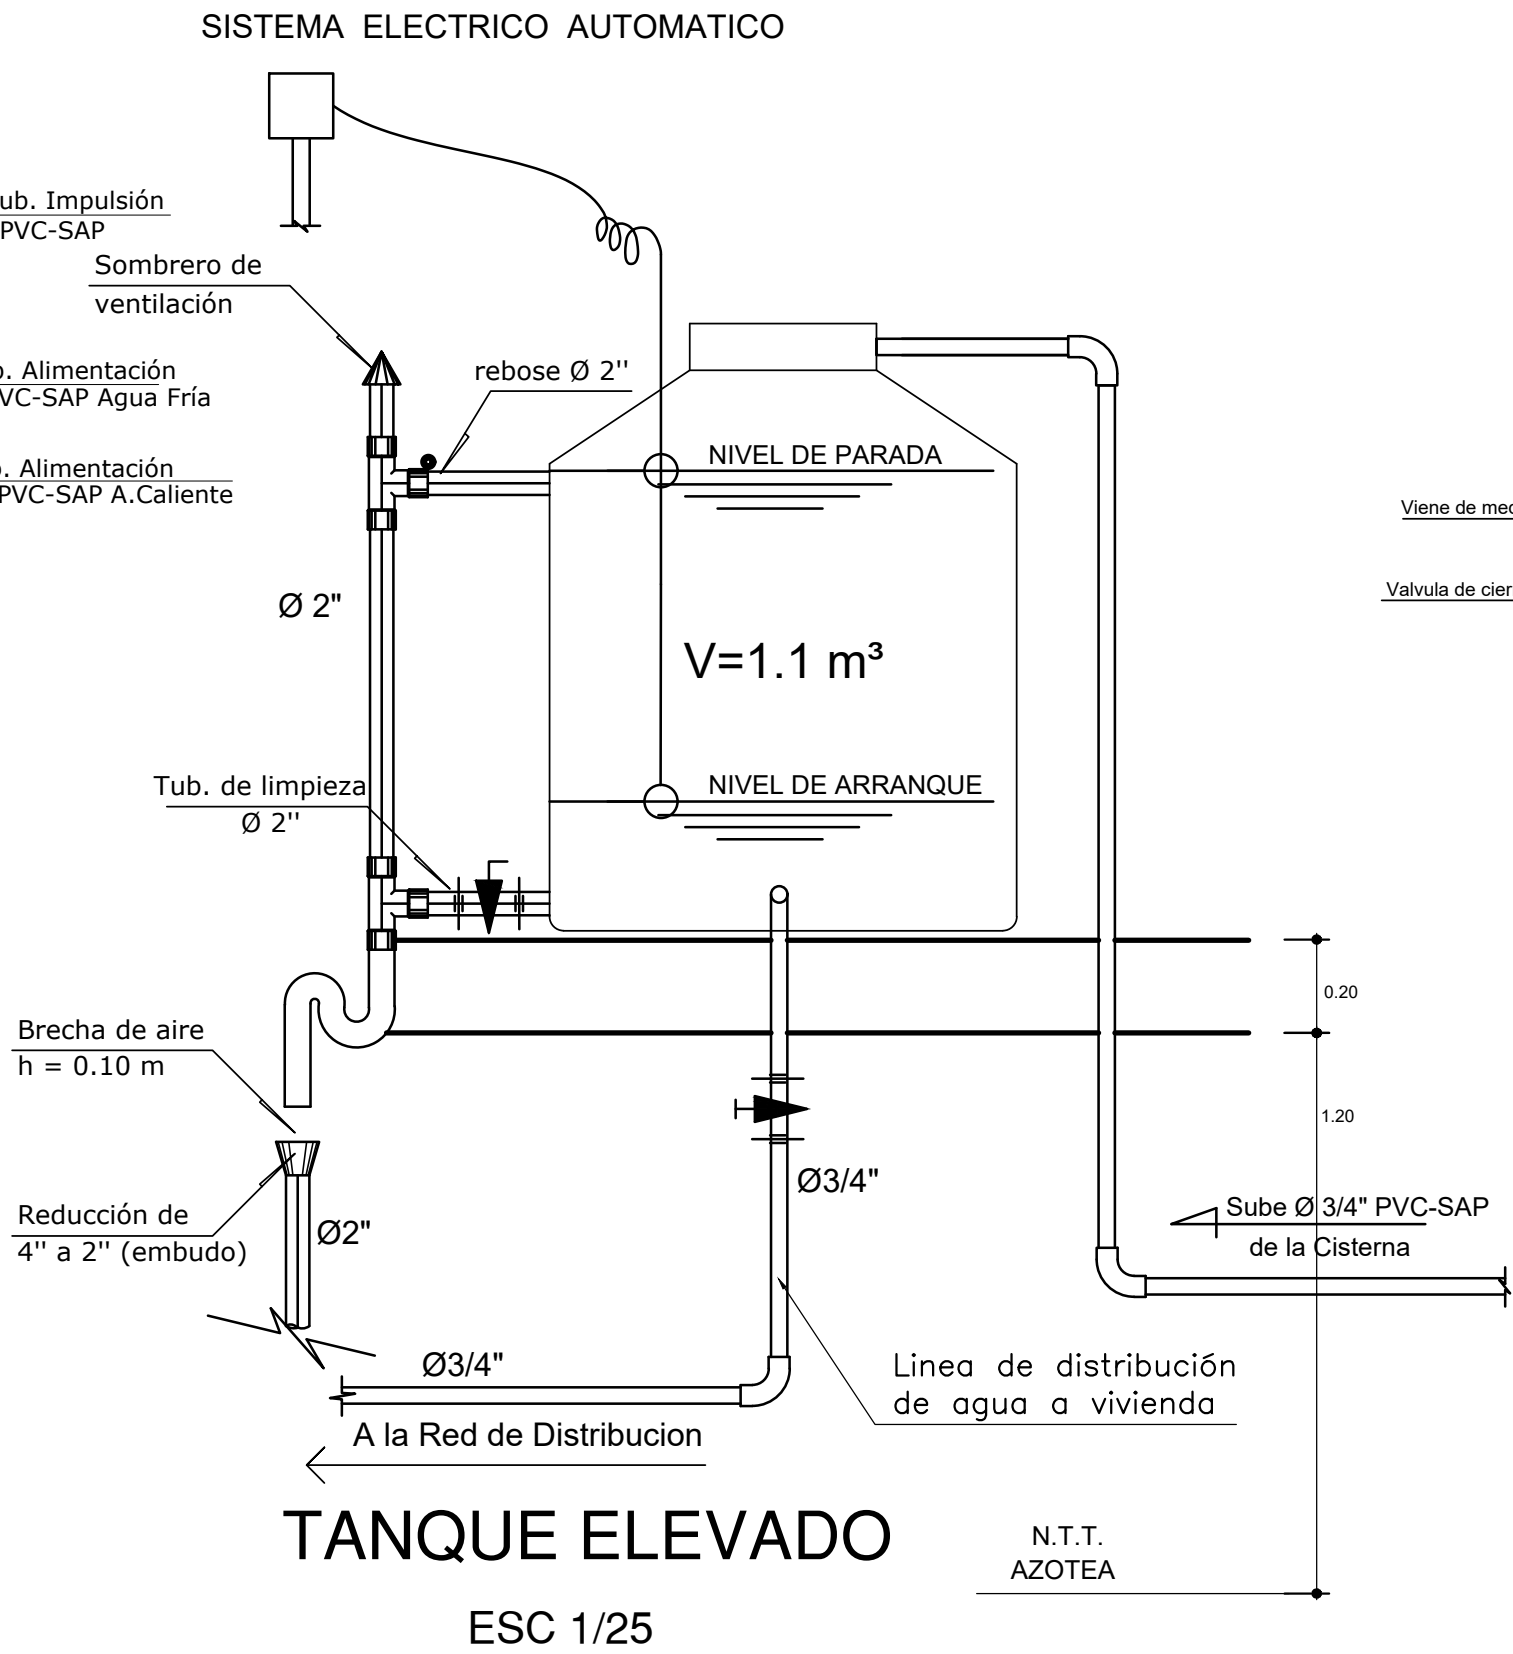

PROYECTO: VIVIENDA UNIFAMILIAR	UBICACIÓN :	DIBUJO : JLAY	TÍTULO DE LÁMINA: INSTALACIONES SANITARIAS RED DISTRIBUCIÓN AGUA FRÍA Y CALIENTE - 1er y 2do PISO	Nº LÁMINA: IS-03
	URB. MIRAFLORES BOULEVARD PARK PLAZA Mz. AN - Lote 18 - II ETAPA - CASTILLA	RESPONSABLE : ARQ. RENZO IZQUIERDO		
	PROPIETARIO:	ESCALA : 1 / 50		
	Sra. ROSSEMARY YANIRE FERNÁNDEZ ROJAS DNI: 80366589	FECHA : JULIO 2026		

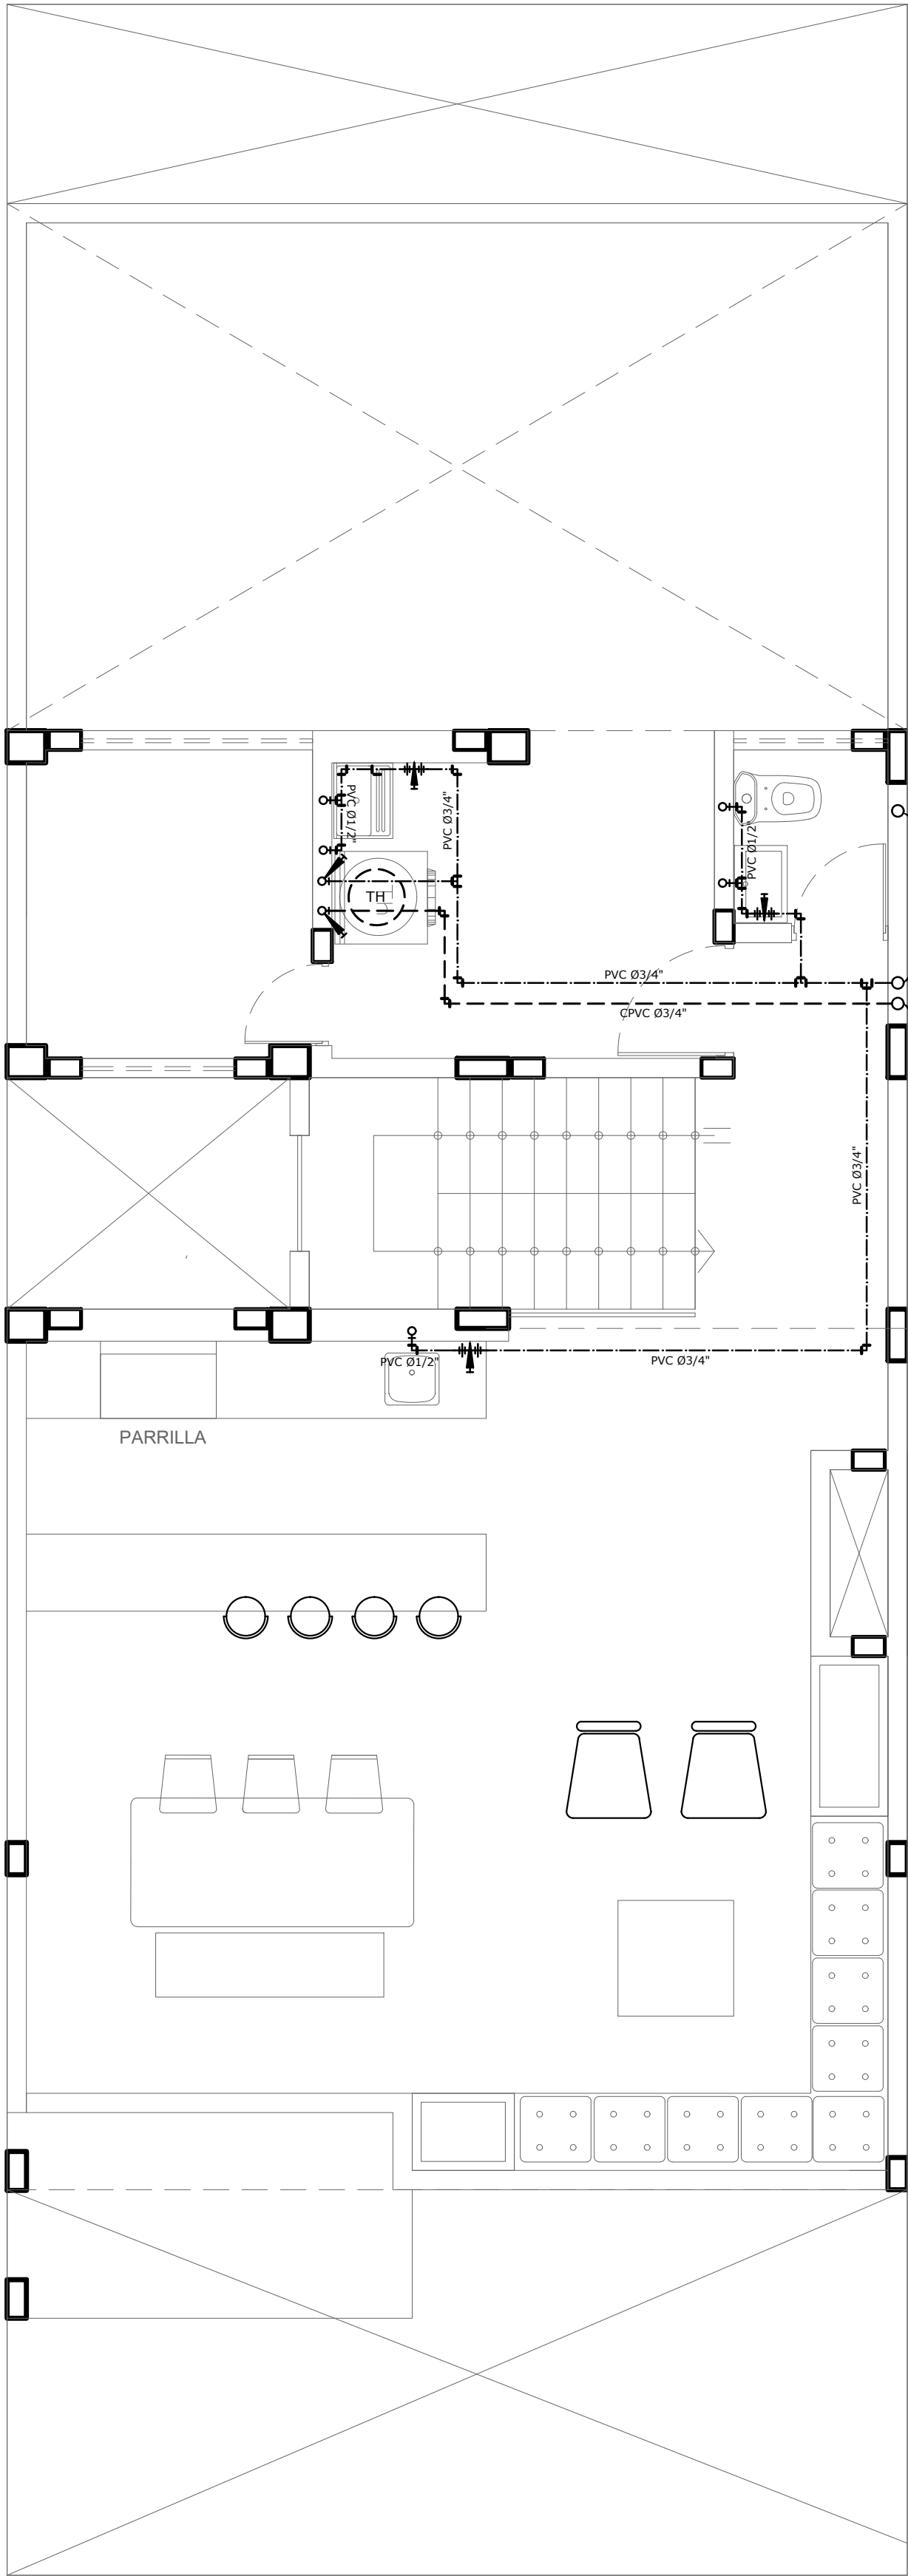






PLANTA AZOTEA
ESC:1/50

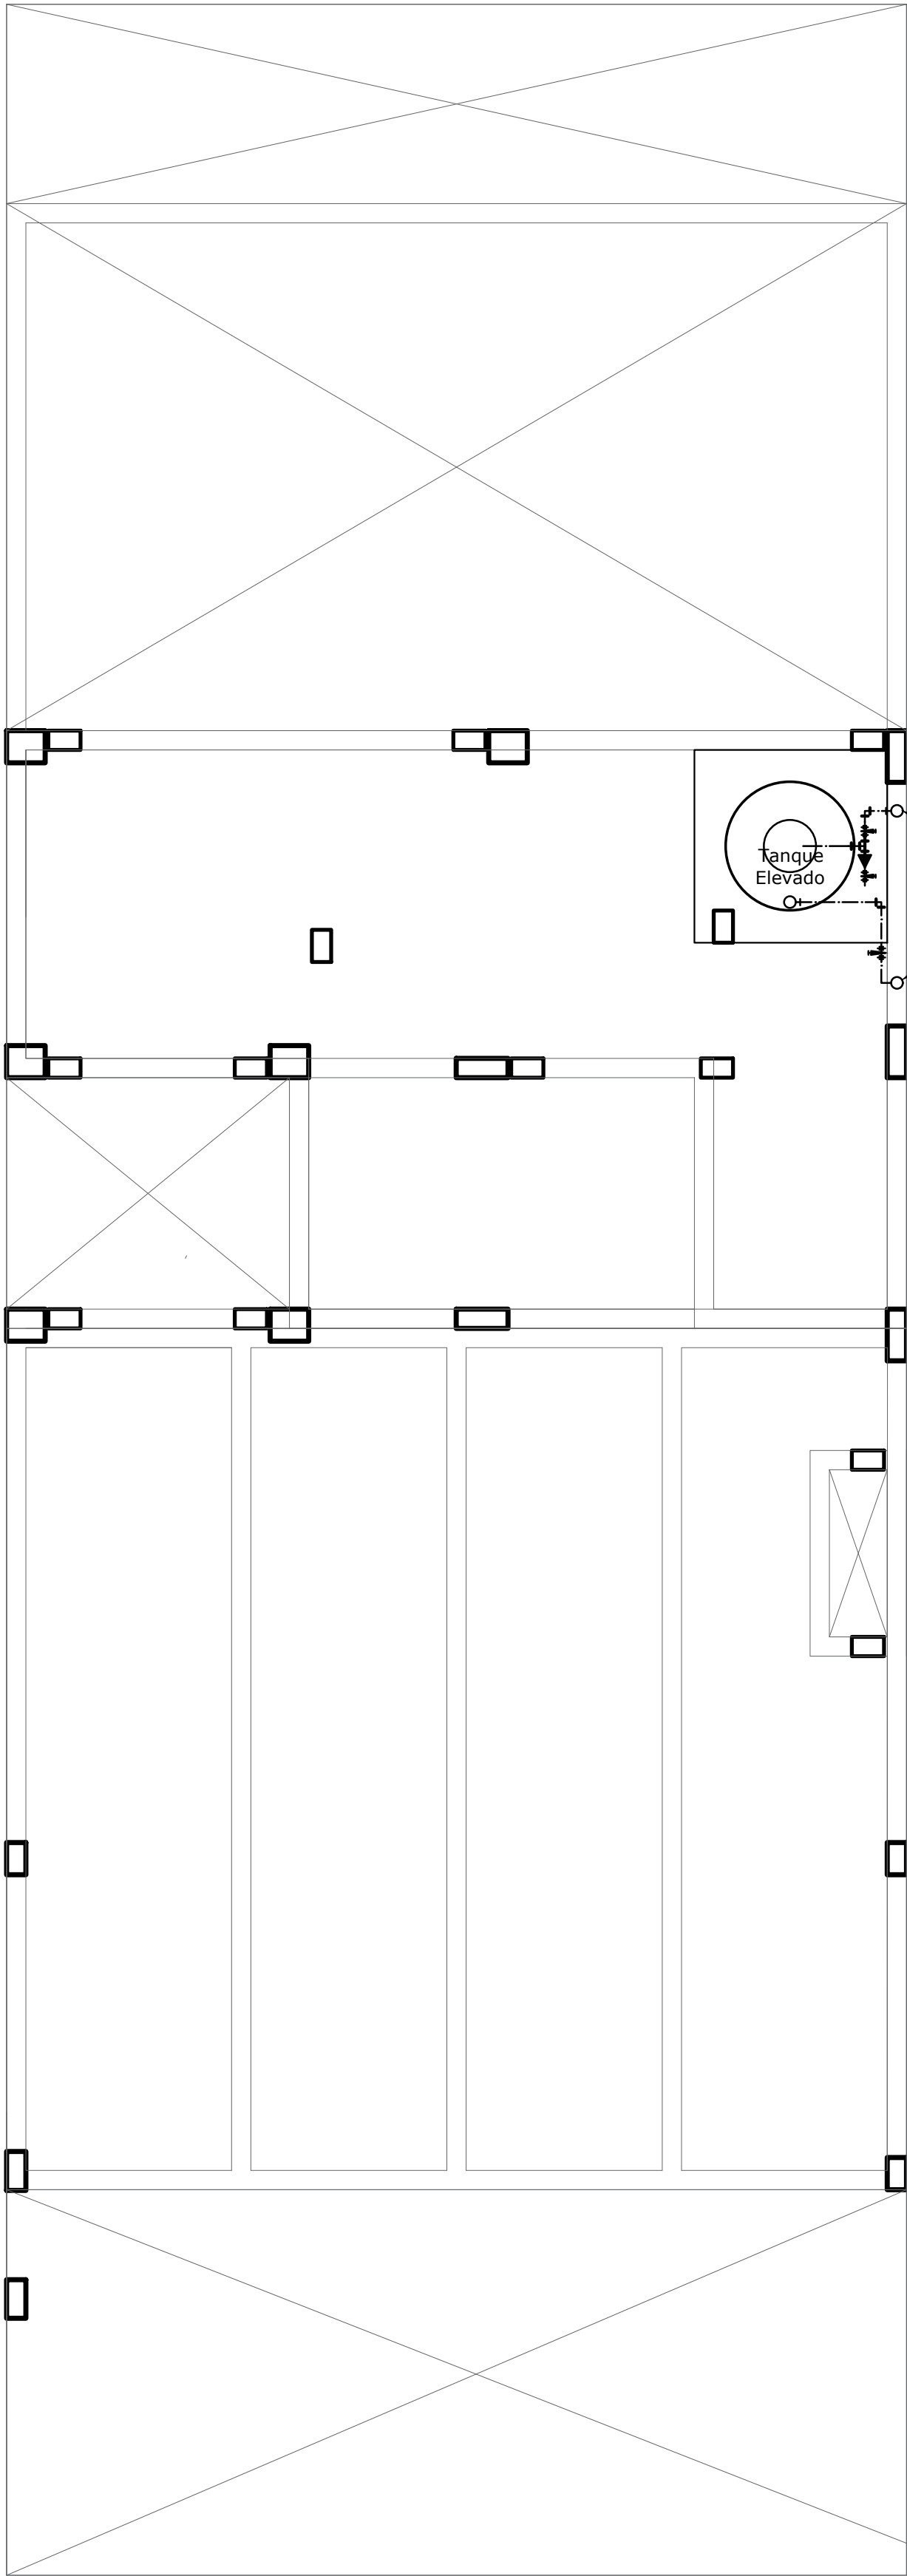

PLANTA TECHO
ESC:1/50

LEYENDA RED DE DESAGÜE	
SÍMBOLO	DESCRIPCION
	RED DE DESAGUE PVC-SAP Ø 4"
	RED DE DESAGUE PVC-SAP Ø 2"
	TUBERIA DE VENTILACION Ø 2" PVC- SAL
	SUMIDERO
	CAJA DE REGISTRO
	REGISTRO ROSCADO DE BRONCE
	"Y" SIMPLE
	"Y" DOBLE
	CODO 45°
S = 1%	PENDIENTE DE LA TUBERIA



ESPECIFICACIONES TECNICAS
RED DE DESAGUE: - LAS TUBERIAS A EMPLEARSE EN LAS REDES SERAN DE PVC TIPO LIVIANO PVC-SAL CON ACCESORIOS DEL MISMO MATERIAL, CON UNIONES SELLADOS CON PEGAMENTO ESPECIAL - LAS CAJAS DE REGISTROS SE INSTALARAN EN LUGARES INDICADOS EN LOS PLANOS, SERAN DE ALBANILERIA IMPERMEABILIZADOS, CON MARCO Y TAPA DE FIERRO FUNDIDO Y/O CON EL MISMO MATERIAL DEL PISO TERMINADO. EN DIMENSIONES INDICADAS. - LOS REGISTROS ROSCADOS SERAN DE BRONCE, CON TAPA ROSCADA HERMETICA E IRAN FIJADOS A LA CABEZA DEL ACCESORIO CORRESPONDIENTE . - LAS TUBERIAS Y ACCESORIOS PARA DESAGUE Y VENTILACION, SERAN DE PVC RIGIDA SAP DE UNION A SIMPLE PRESION, PESADA Y/O LIVIANA CON PEGAMENTO O CEMENTO SOLVENTE PARA TUBERIA DE PVC. SEGUN NORMAS. - PENDIENTES PARA TUBERIAS DE DESAGUE: - Ø 2" = 1.5 ‰ (MINIMO) - Ø 4" = 1.0 ‰ (MINIMO) - Ø 6" = 1.0 ‰ (MINIMO) - LAS TUBERIAS DE VENTILACION SE PROLONGARAN 40cm. POR ENCIMA DEL N.T.T. Y LLEVARAN SOMBRERO DE VENTILACION. PRUEBAS: - LAS TUBERIAS DE DESAGUE SERAN PROBADAS A TUBO LLENO DE AGUA DURANTE 24 HORAS SIN PRESENTAR PERDIDA DE NIVEL

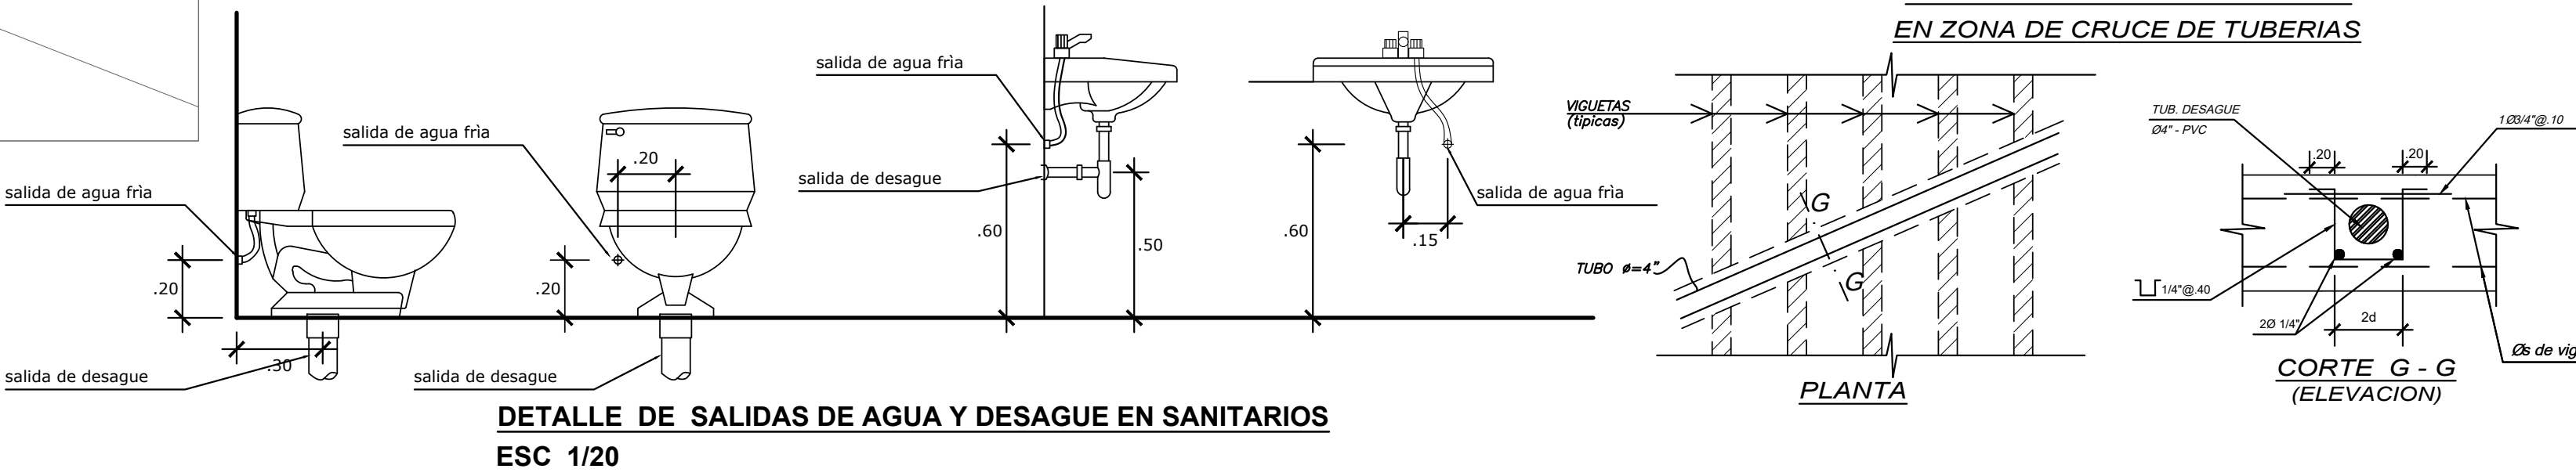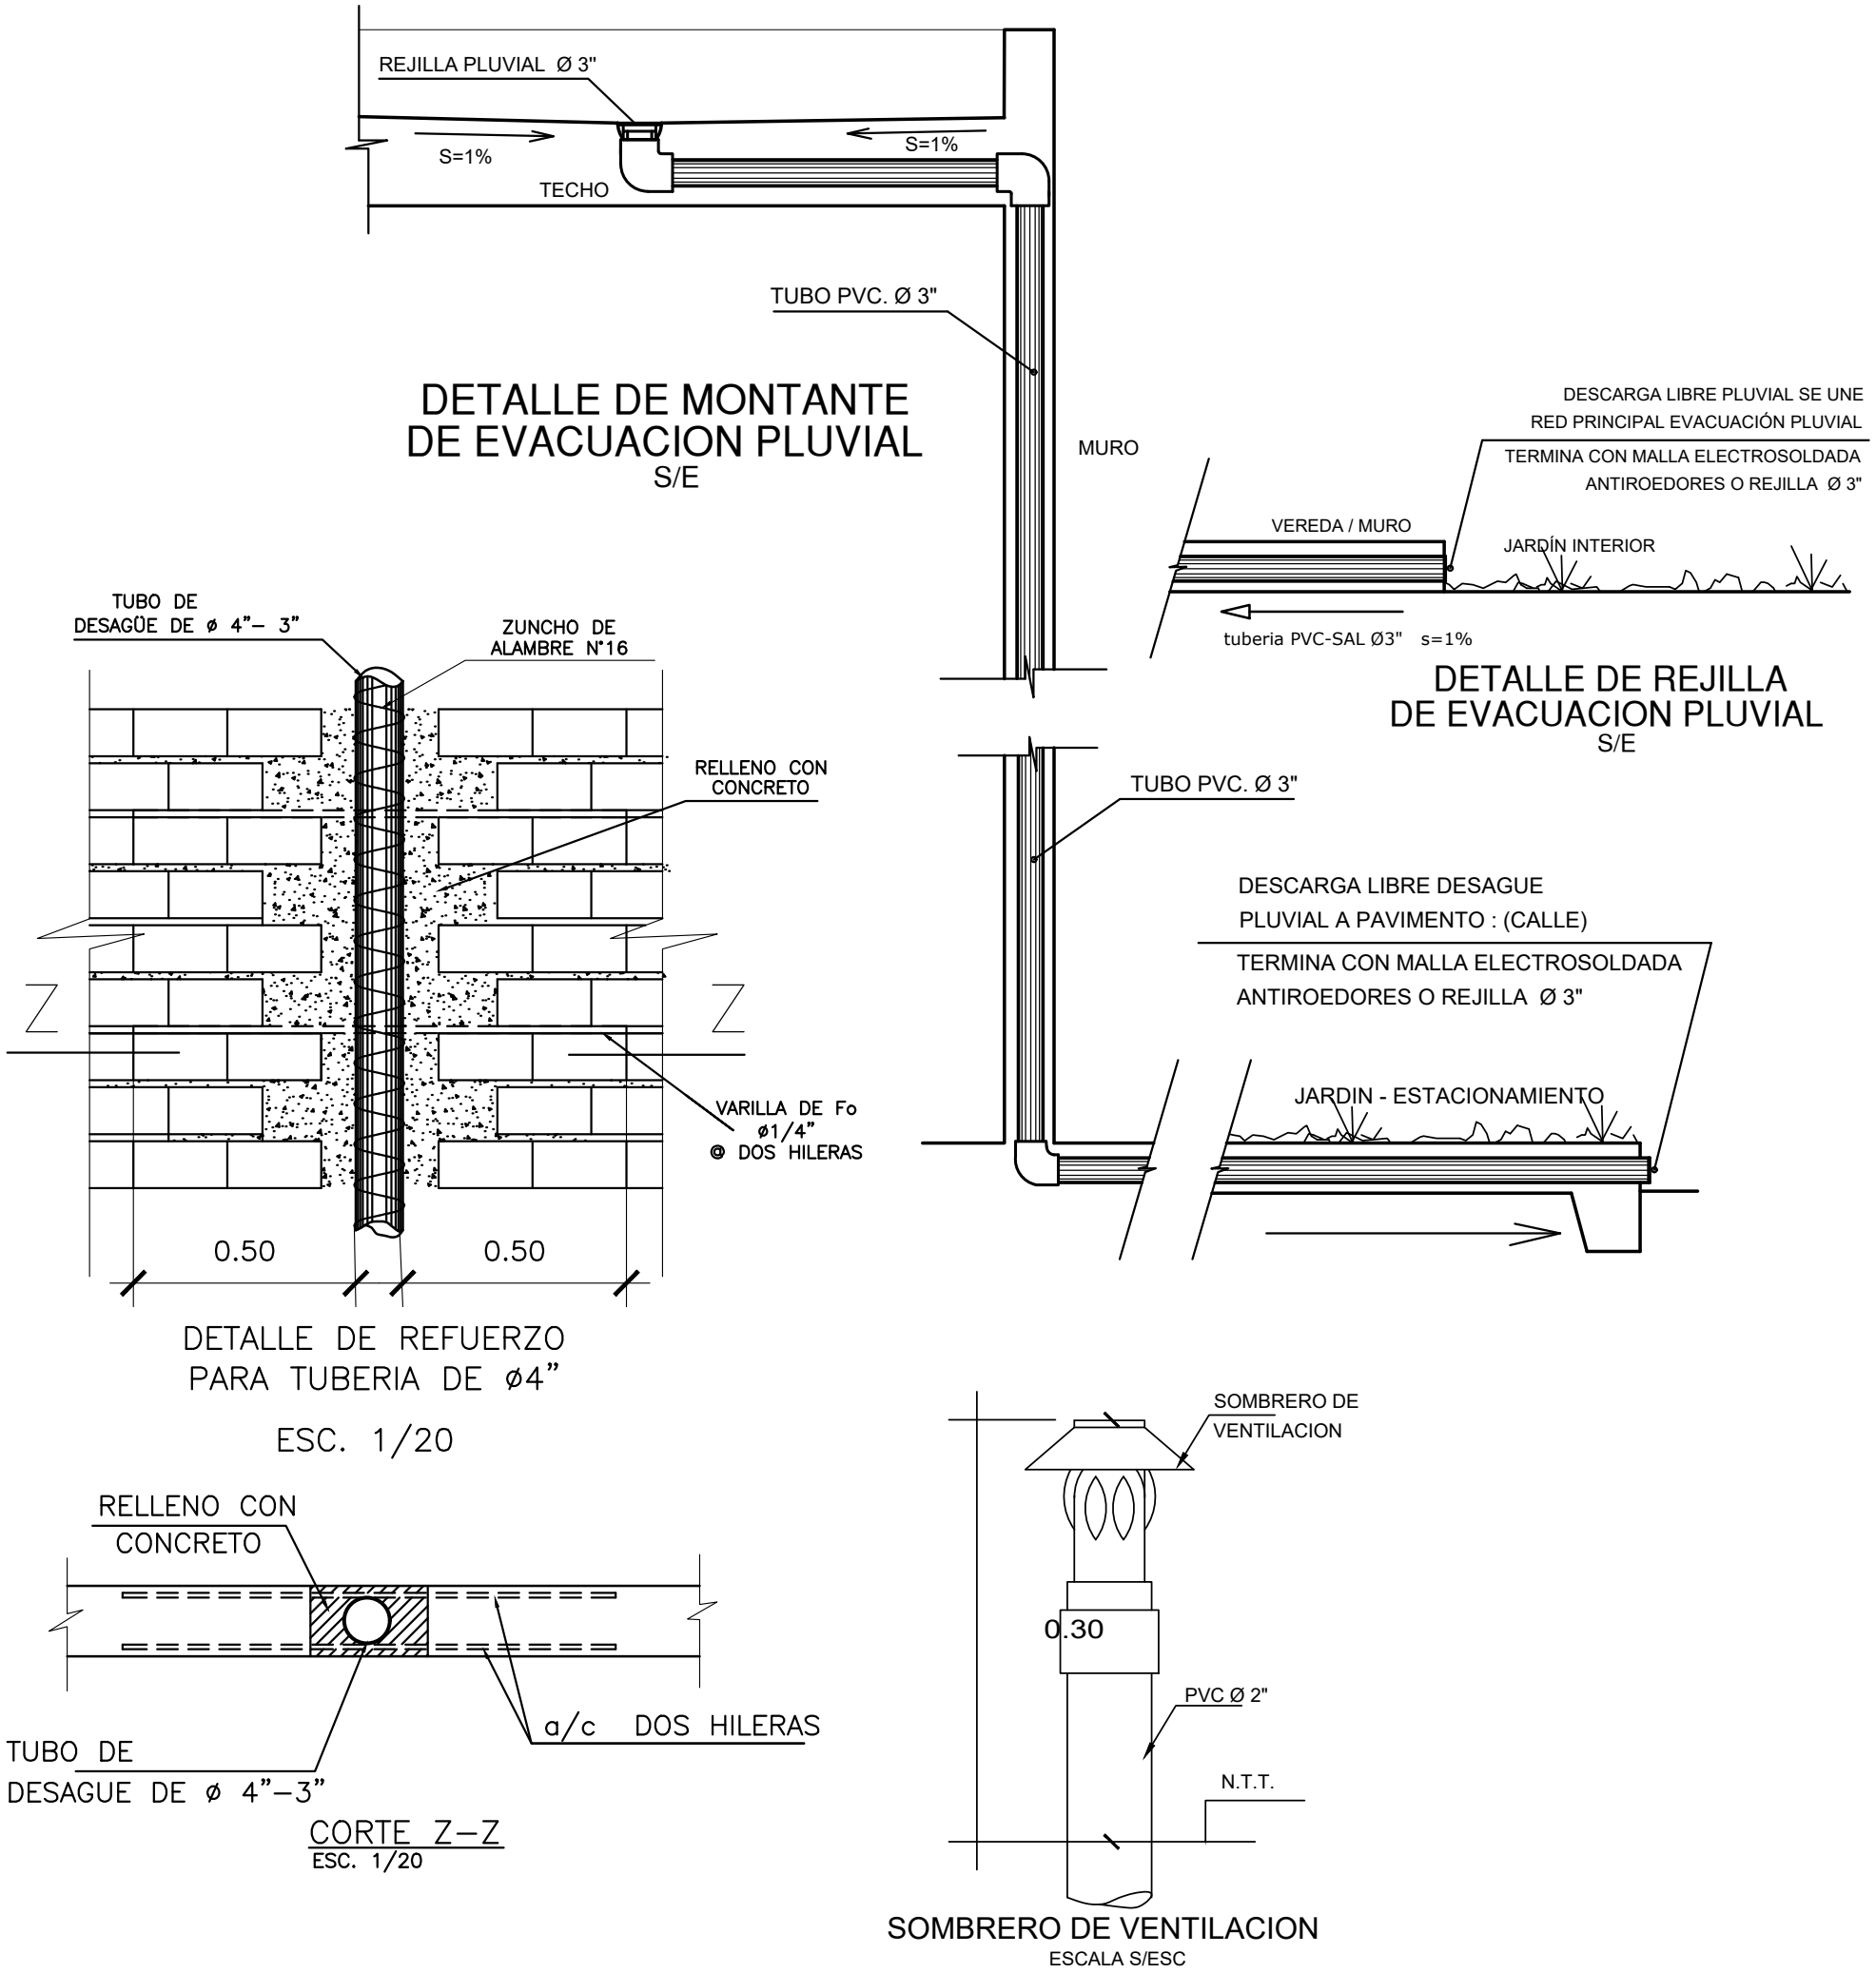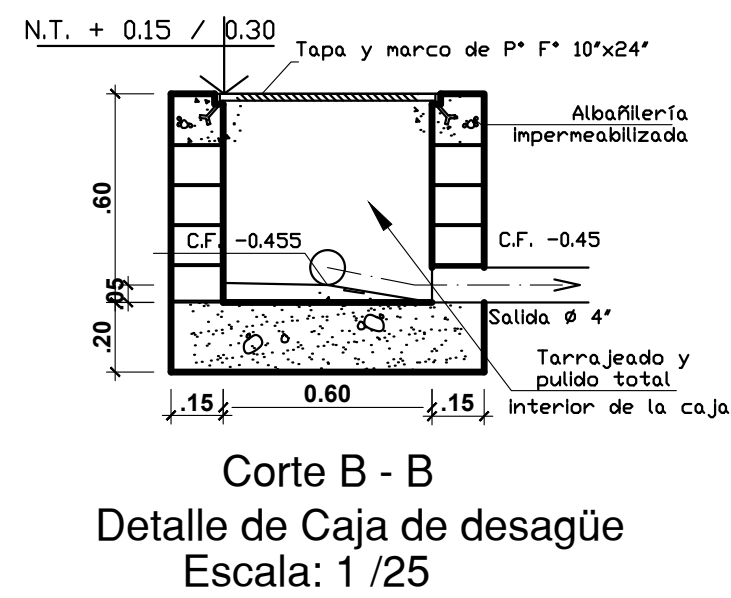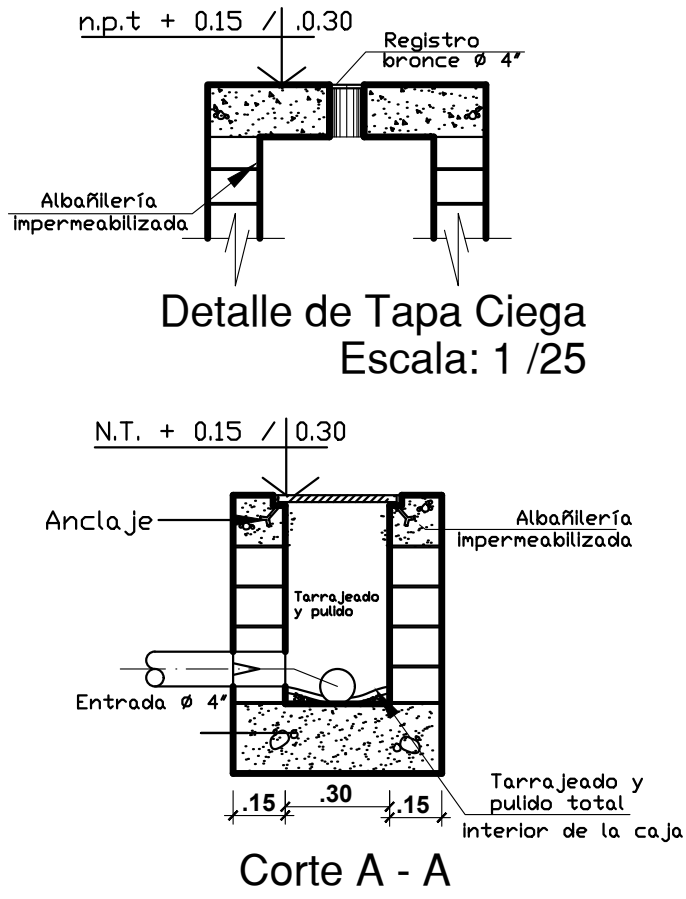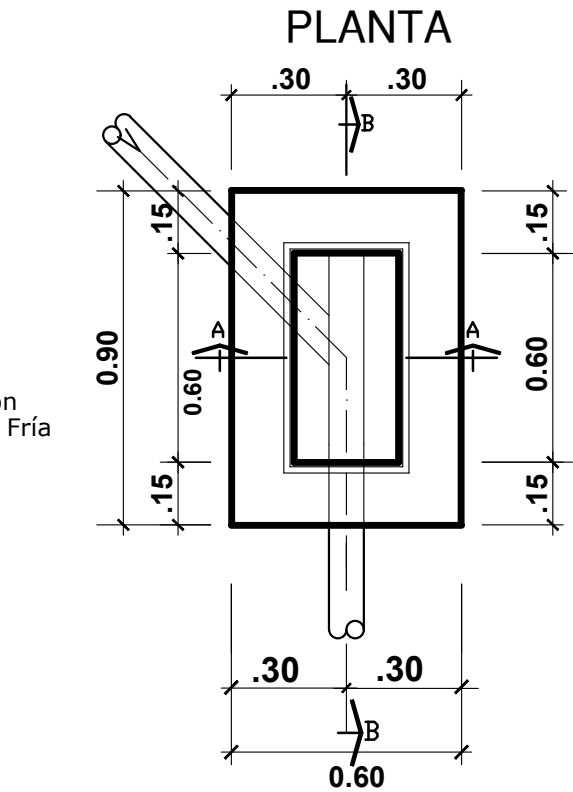

PROYECTO: VIVIENDA UNIFAMILIAR	UBICACIÓN :	DIBUJO : JLAY
	URB. MIRAFLORES BOULEVARD PARK PLAZA Mz. AN - Lote 18 - II ETAPA - CASTILLA	RESPONSABLE : ARQ. RENZO IZQUIERDO
	PROPIETARIO:	ESCALA : 1 / 50
	Sra. ROSSEMERY YANIRE FERNÁNDEZ ROJAS DNI: 80366589	FECHA : JULIO 2026

TITULO DE LÁMINA: INSTALACIONES SANITARIAS RED DISTRIBUCIÓN AGUA FRÍA Y CALIENTE - AZOTEA Y TECHO

N° LÁMINA: IS-04

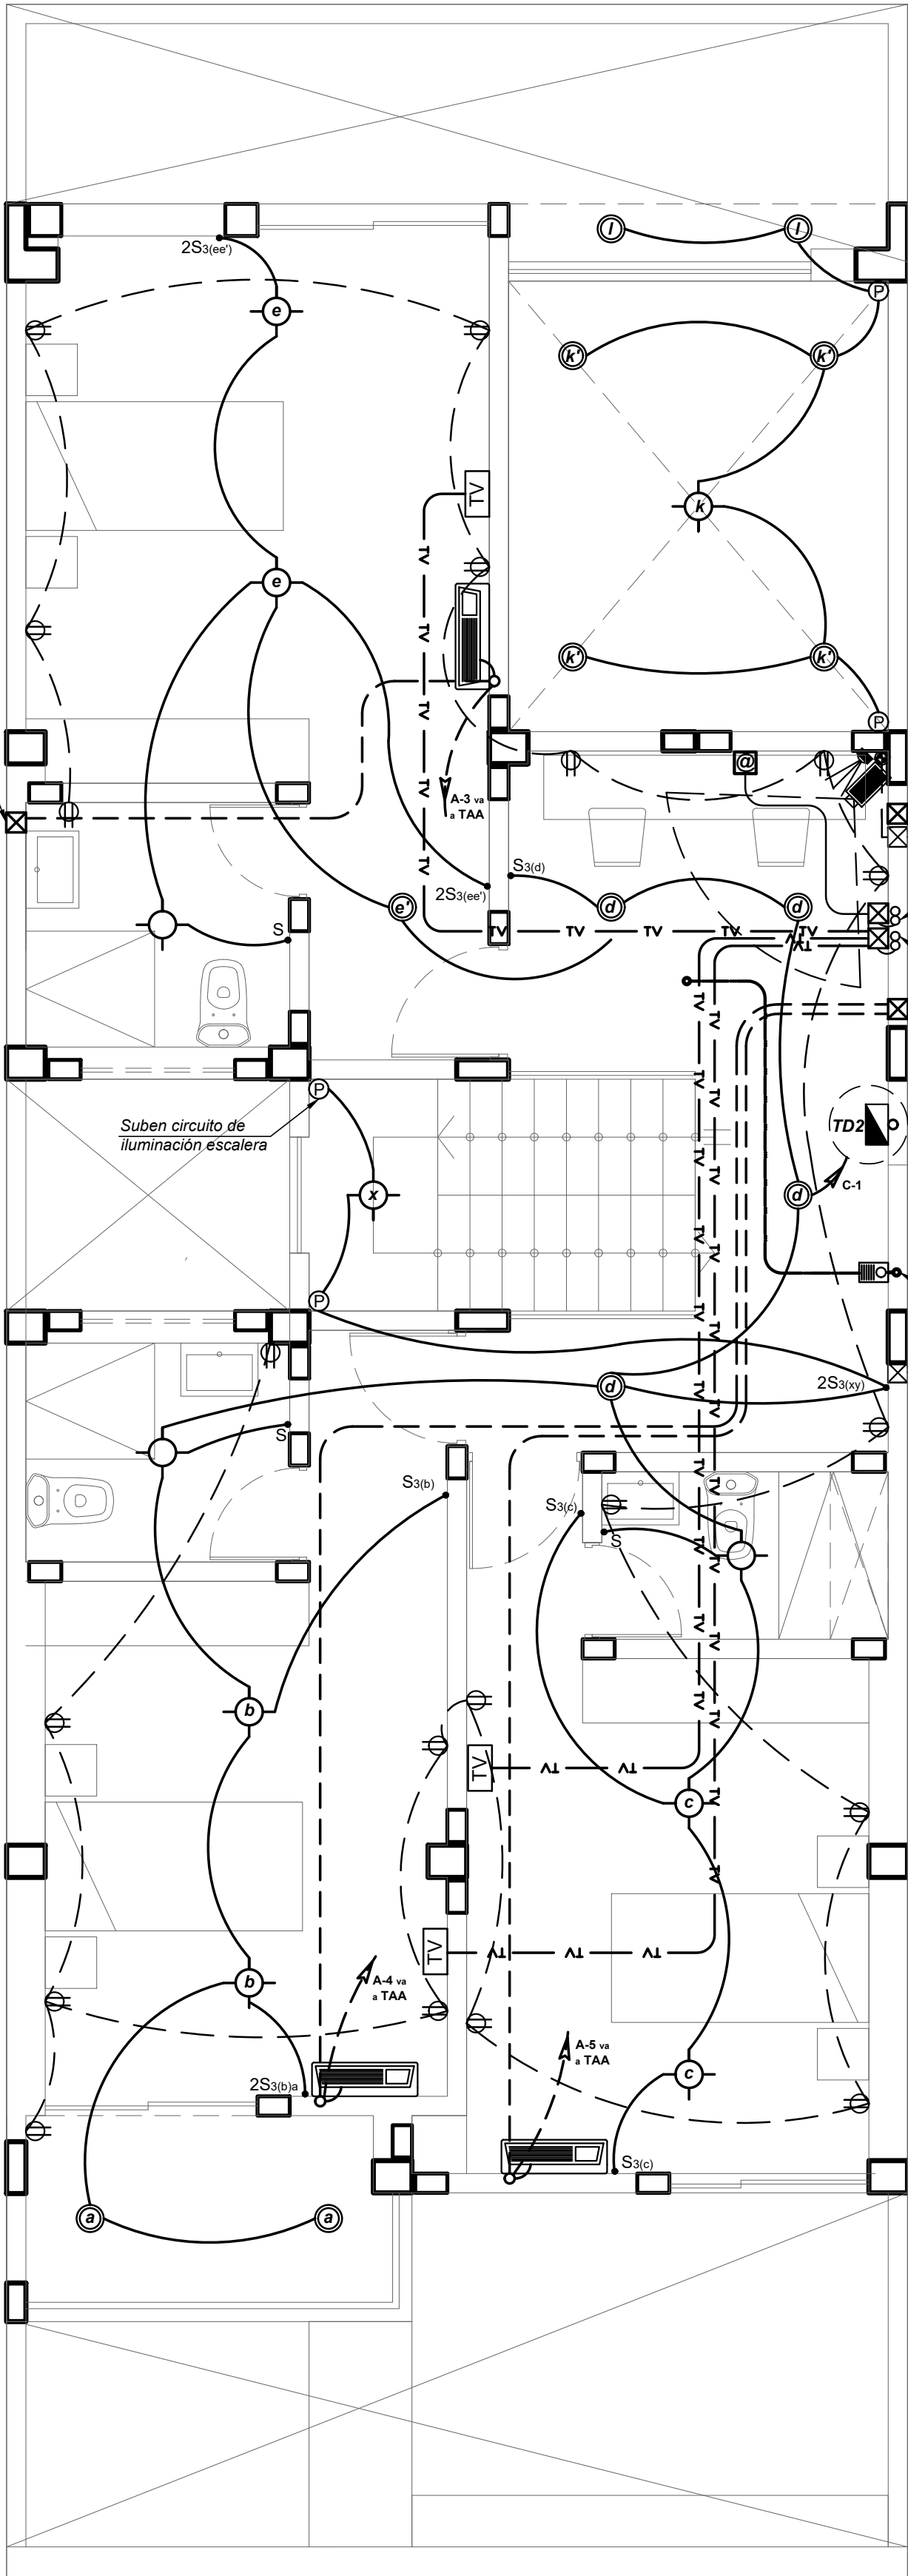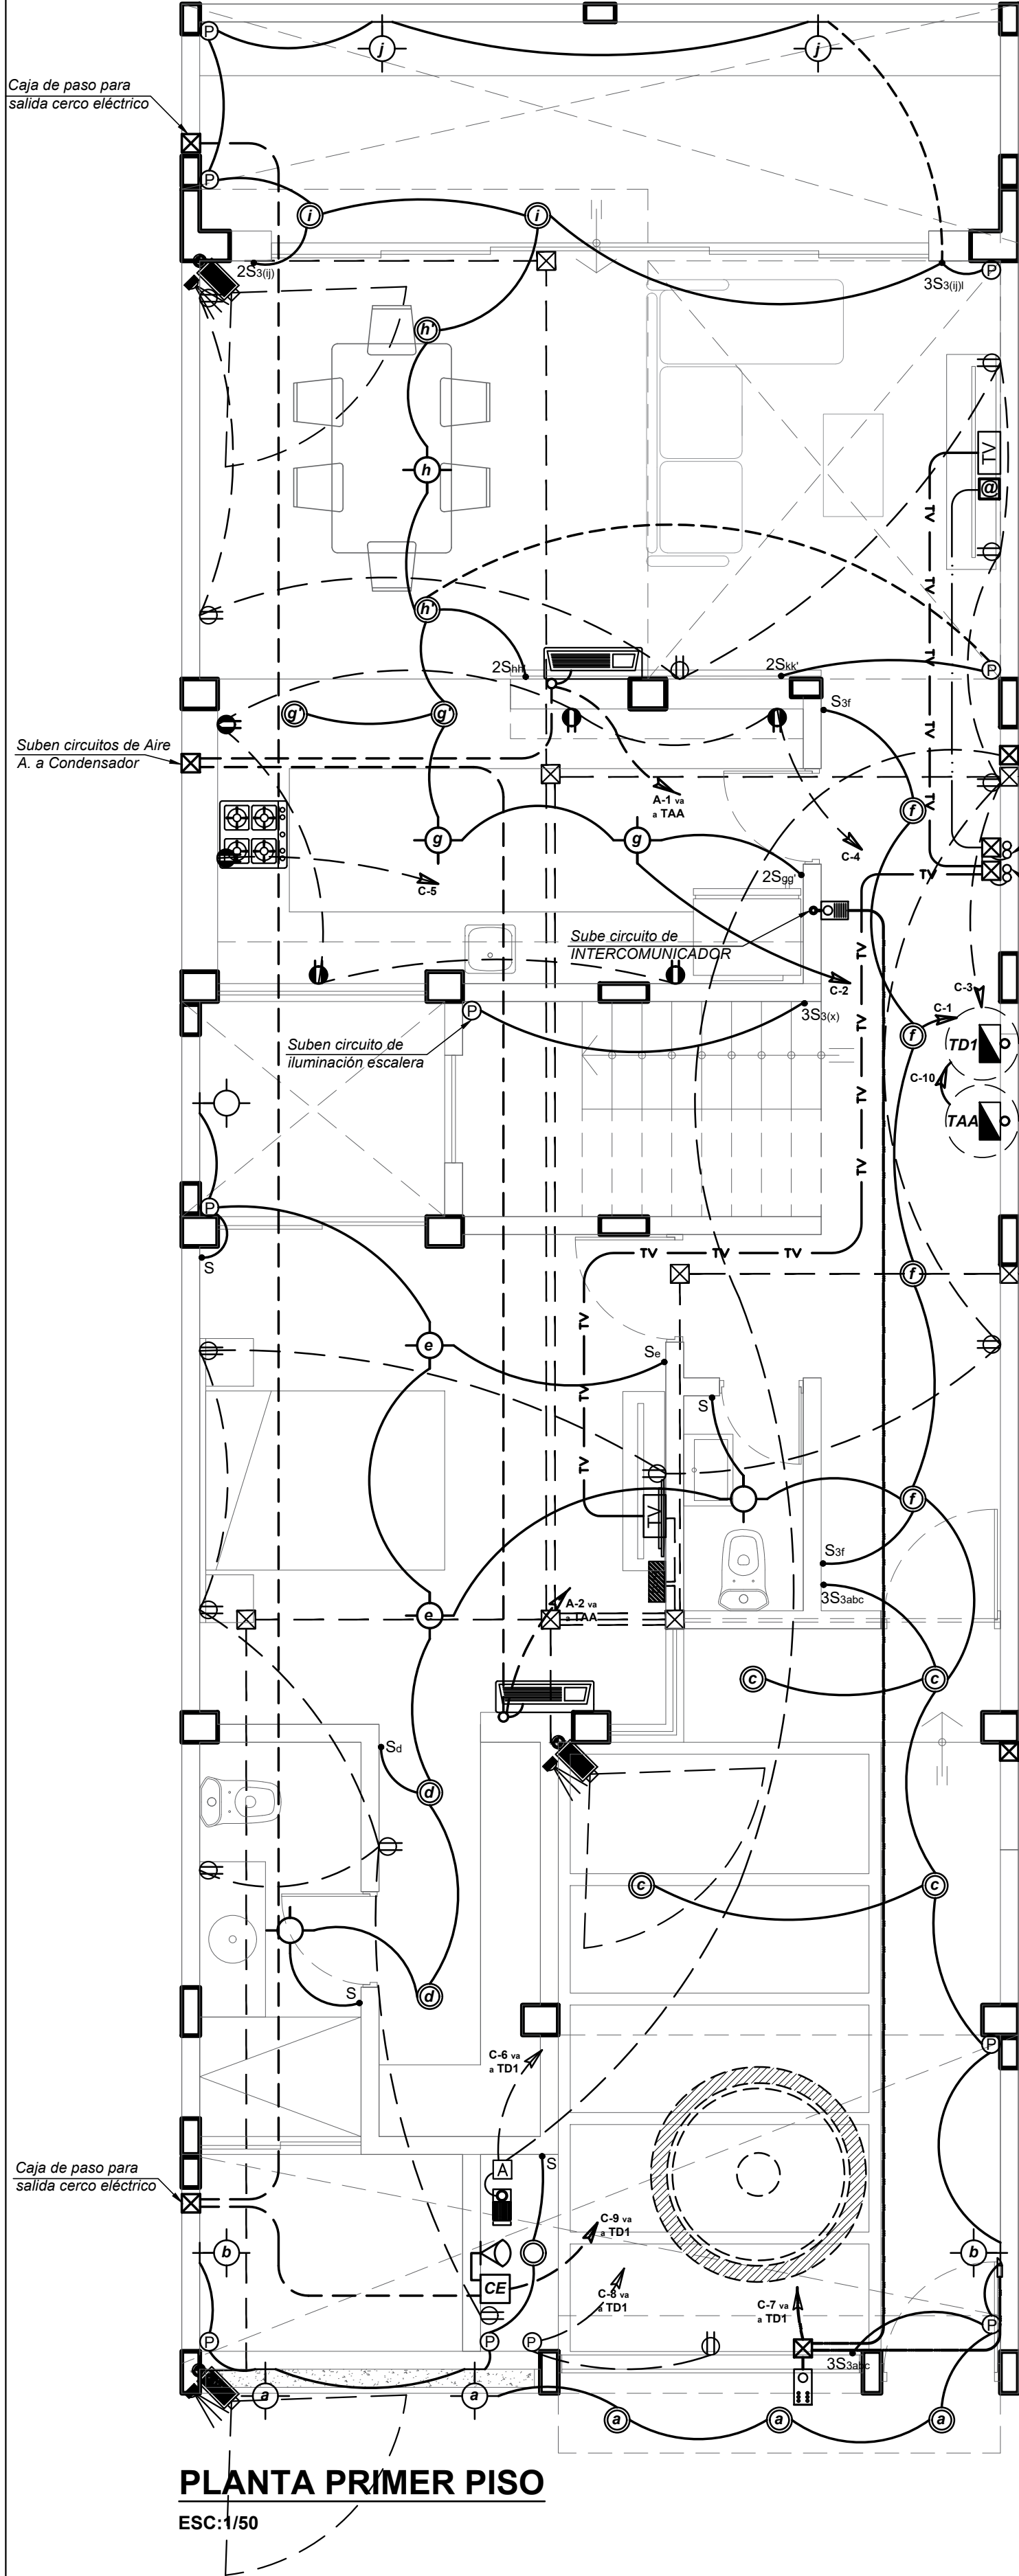

LEYENDA			
SÍMBOLO	DESCRIPCIÓN	CAJA	ALTURA
	SALIDA PARA ARTEFACTO DE TECHO	OCT. 100 x 55	CIELO RASO
	SALIDA PARA BRAQUETE DE PARED	OCT. 100 x 55	2,10
	SALIDA PARA DÍCRICO DE TECHO	OCT. 100 x 55	CIELO RASO
	SALIDA PARA DÍCRICO EN PISO	OCT. 100 x 55	0,00
	SALIDA PARA DÍCRICO EN PARED		2,40
	SALIDA PUNTO DE LUZ LED		
	TOMACORRIENTE BIPOLAR DOBLE, CON TIERRA, 10A 615A-220V	RECT. 100 x 50	0,40
	TOMACORRIENTE BIPOLAR DOBLE, CON TIERRA, 10A 615A-220V	RECT. 100 x 50	1,40
	TOMACORRIENTE BIPOLAR DOBLE, CON TIERRA, 10A 615A-220V	RECT. 100 x 50	1,80
	INTERRUPTOR UNIPOLAR, 5A-220V	RECT. 100 x 50	1,00
	INTERRUPTOR DOBLE, 5A-220V	RECT. 100 x 50	1,00
	INTERRUPTOR DE CONMUTACION 220V - 5A	ESPECIAL	1,00
	SALIDA PARA TELÉFONO E INTERNET (REPETIDORES)	RECT. 100 x 50	0,30
	CAJA DE PASE EN PISO O PARED	OCT. 100 x 55	0,40
	BOMBA DE AGUA		
	TABLERO DE DISTRIBUCIÓN	ESPECIAL	1,40
	CAJA PORTAMEDIDOR DE LUZ	TIPO LT 6 L	1,2
	SALIDA DE AUDIO - PARLANTES		
	SALIDA PARA TV-CABLE	RECT. 100 x 50	h=xxx
	SALIDA INTERCOMUNICADOR CON TRANSFORMADOR 220V/6V	RECT. 100 x 50	1,40
	POZO DE TIERRA		
	CIRCUITO EN CONDUCTO EMPOTRADO EN LA PARED O TECHO		
	CIRCUITO EN CONDUCTO EMPOTRADO EN EL PISO		
	CIRCUITO EN CONDUCTO EMPOTRADO TELEVISION		
	CIRCUITO EN CONDUCTO EMPOTRADO INTERCOMUNICADOR		
	CIRCUITO EN CONDUCTO EMPOTRADO TELÉFONO - INTERNET		

DIAGRAMA UNIFILAR TABLERO GENERAL (TD1)

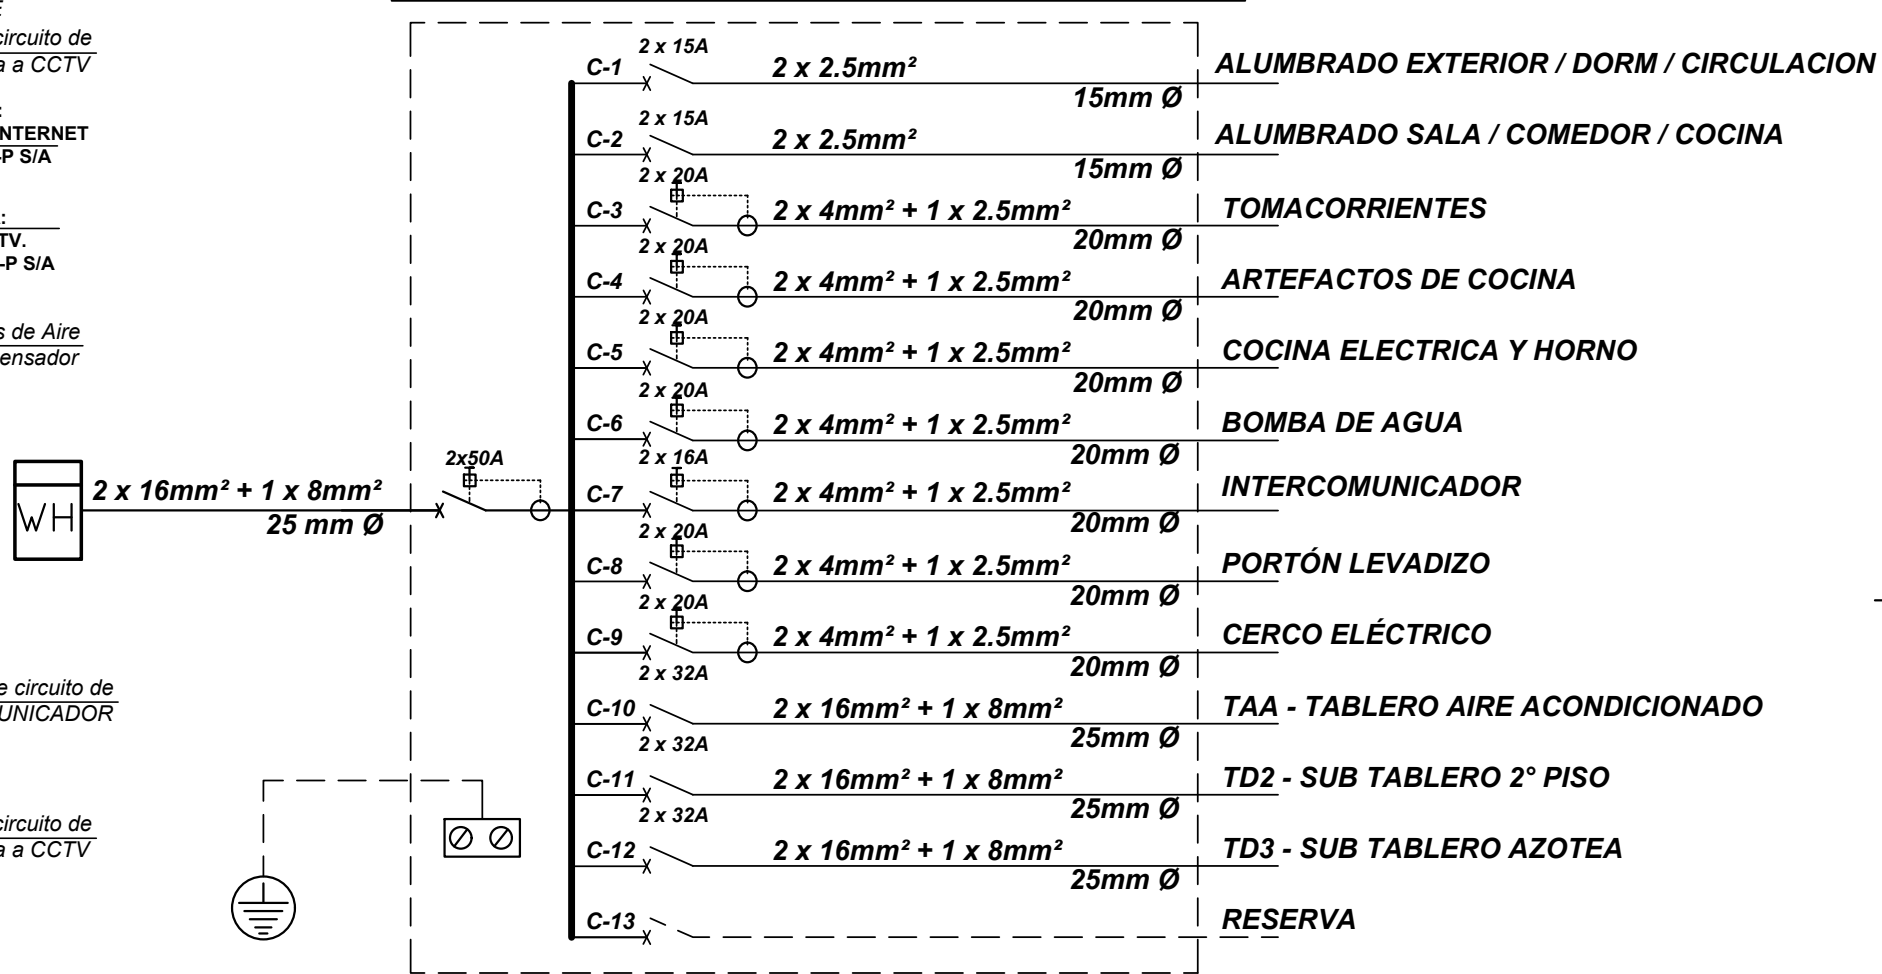


DIAGRAMA UNIFILAR TABLERO 2do PISO (TD2)

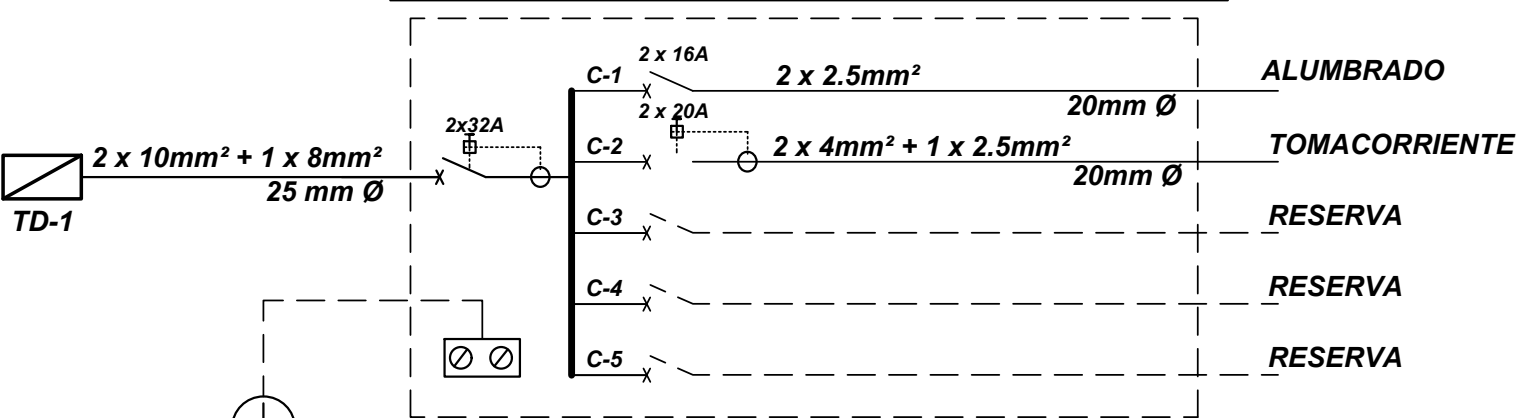


DIAGRAMA UNIFILAR TABLERO AZOTEA (TD3)


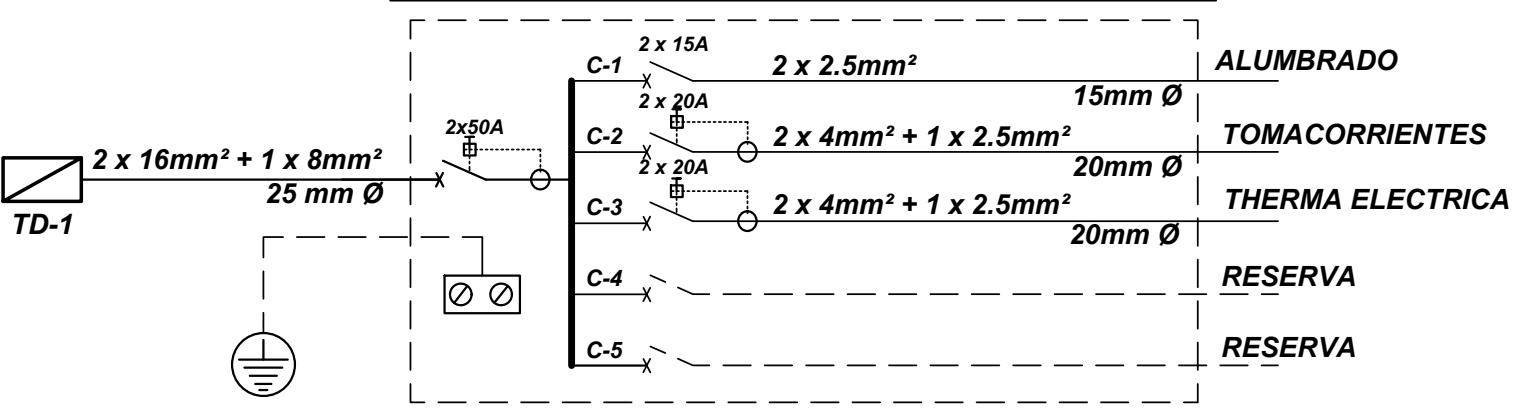




DIAGRAMA UNIFILAR TAB. AIRE ACOND. (TAA)

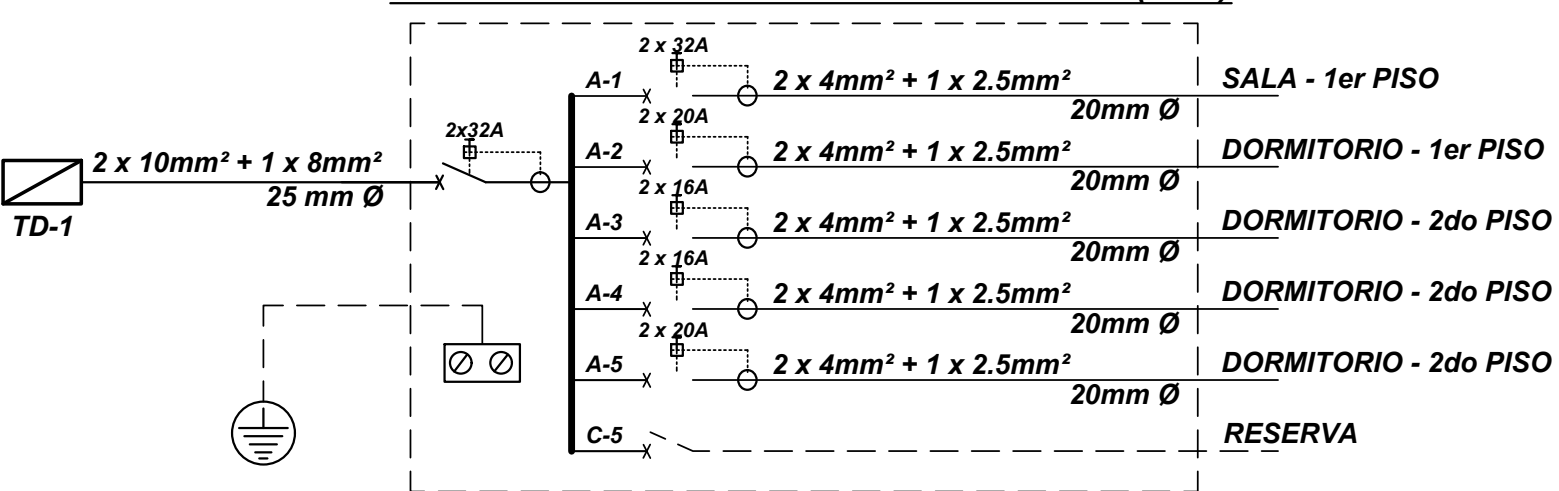

ESPECIFICACIONES TECNICAS

- 1.- Características del Sistema Monofásico 2 hilos 220 voltios 60 Hz.cos. Ø= 0.9
- 2.- El mínimo conductor THW y tubería PVC SAP a usar será de 2.5 mm - 15 mm Ø toda la tubería a empotrará en techo y/o piso será del tipo pesado (SAP) y la empotrada en pared del tipo liviana SEL.
- 3.- Las cajas para interiores serán metálicas de características siguientes
 - Octogonales: Para salida de iluminación
 - Rectangulares: Para salida de interruptores, tomacorrientes, telef. interno tv. y pulsador.
- Cuadradas: Para pase y/o empalme
- 4.- Los tomacorrientes monofásicos de baño serán del tipo con puesta a tierra y se conectarán junto con los tableros al pozo de tierra con conductor TW - 4 mm²
- 5.- Todos los equipos y materiales que se instalan a la intemperie serán del tipo a prueba de agua
- 6.- Los tableros serán de tipo metálico para empotrar
- 7.- Los conductores para comunicaciones no deberán instalarse a menos de 5 cm de alumbardo y/o fuerza.


DETALLE DE CONEXION DE TABLERO DE DISTRIBUCION

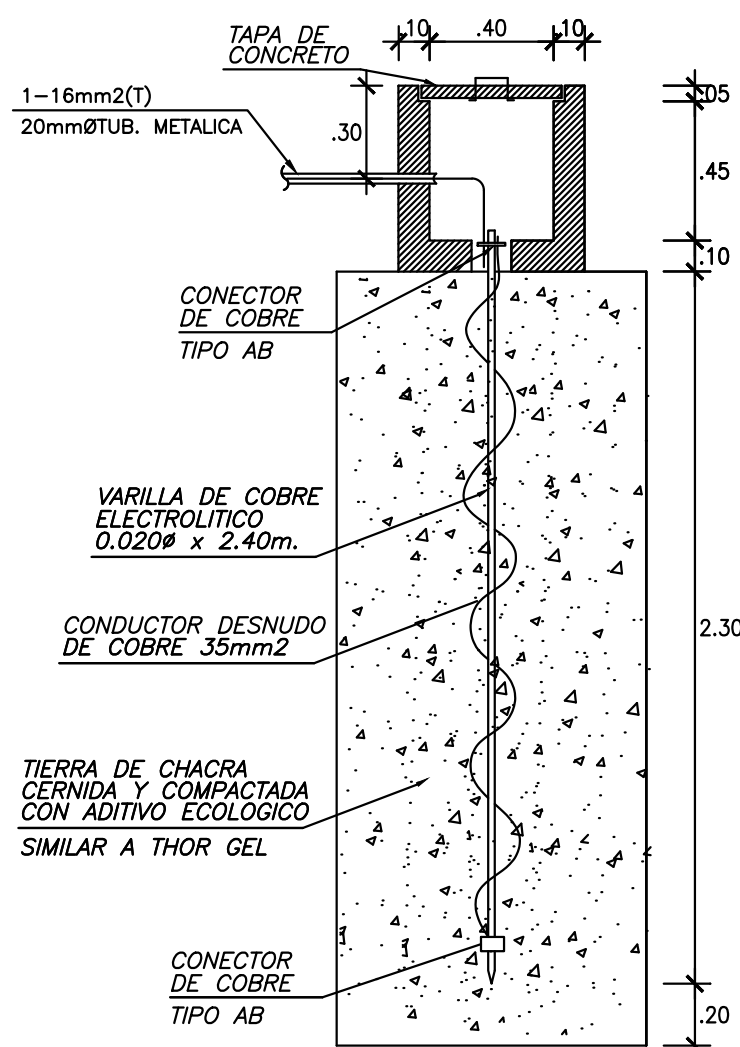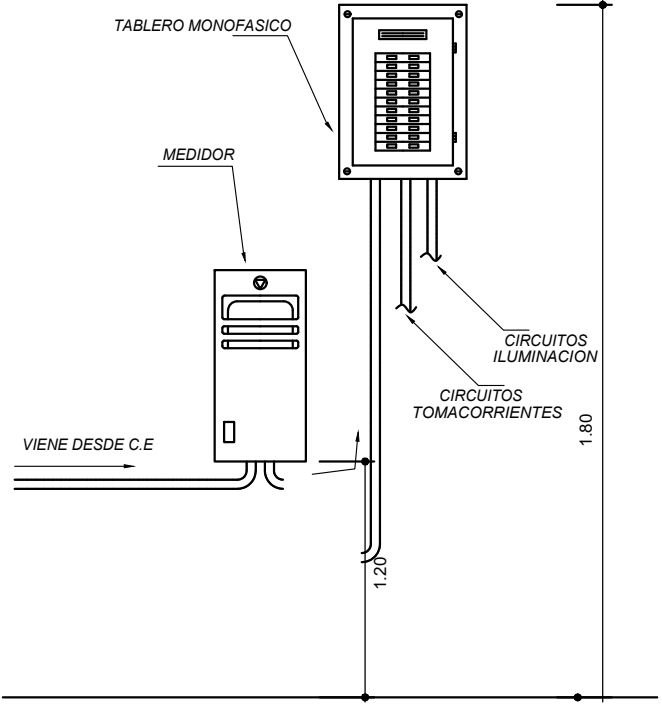

POZO DE TIERRA
RESISTENCIA <20 ohmios
Esc. = 1/25


NOTA:
EL CONTRATISTA INSTALARA
EL NUMERO DE POZOS
NECESARIOS PARA OBTENER
LA RESISTENCIA SOLICITADA

DETALLE DE SALIDAS

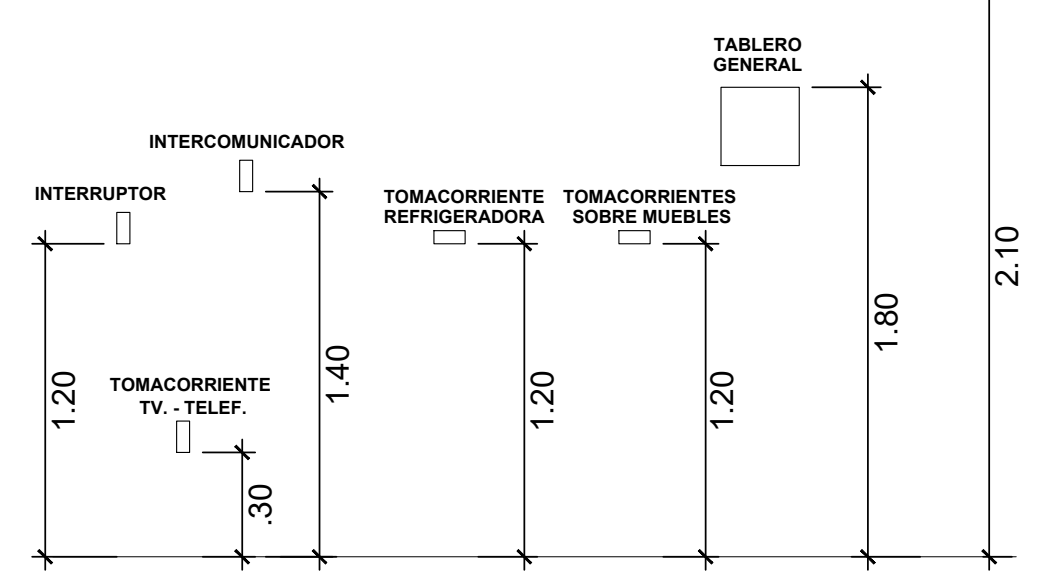


PROYECTO: VIVIENDA UNIFAMILIAR	UBICACIÓN :	DIBUJO : JLAY
	URB. MIRAFLORES BOULEVARD PARK PLAZA Mz. AN - Lote 18 - II ETAPA - CASTILLA	RESPONSABLE : ARQ. RENZO IZQUIERDO
	PROPIETARIO:	ESCALA : 1 / 50
	Sra. ROSSEMERY YANIRE FERNÁNDEZ ROJAS DNI: 80366589	FECHA : JULIO 2026

TITULO DE LÁMINA: INSTALACIONES ELÉCTRICAS CIRCUITOS ELÉCTRICOS - 1er y 2do PISO	Nº LÁMINA: IE-01
--	-------------------------

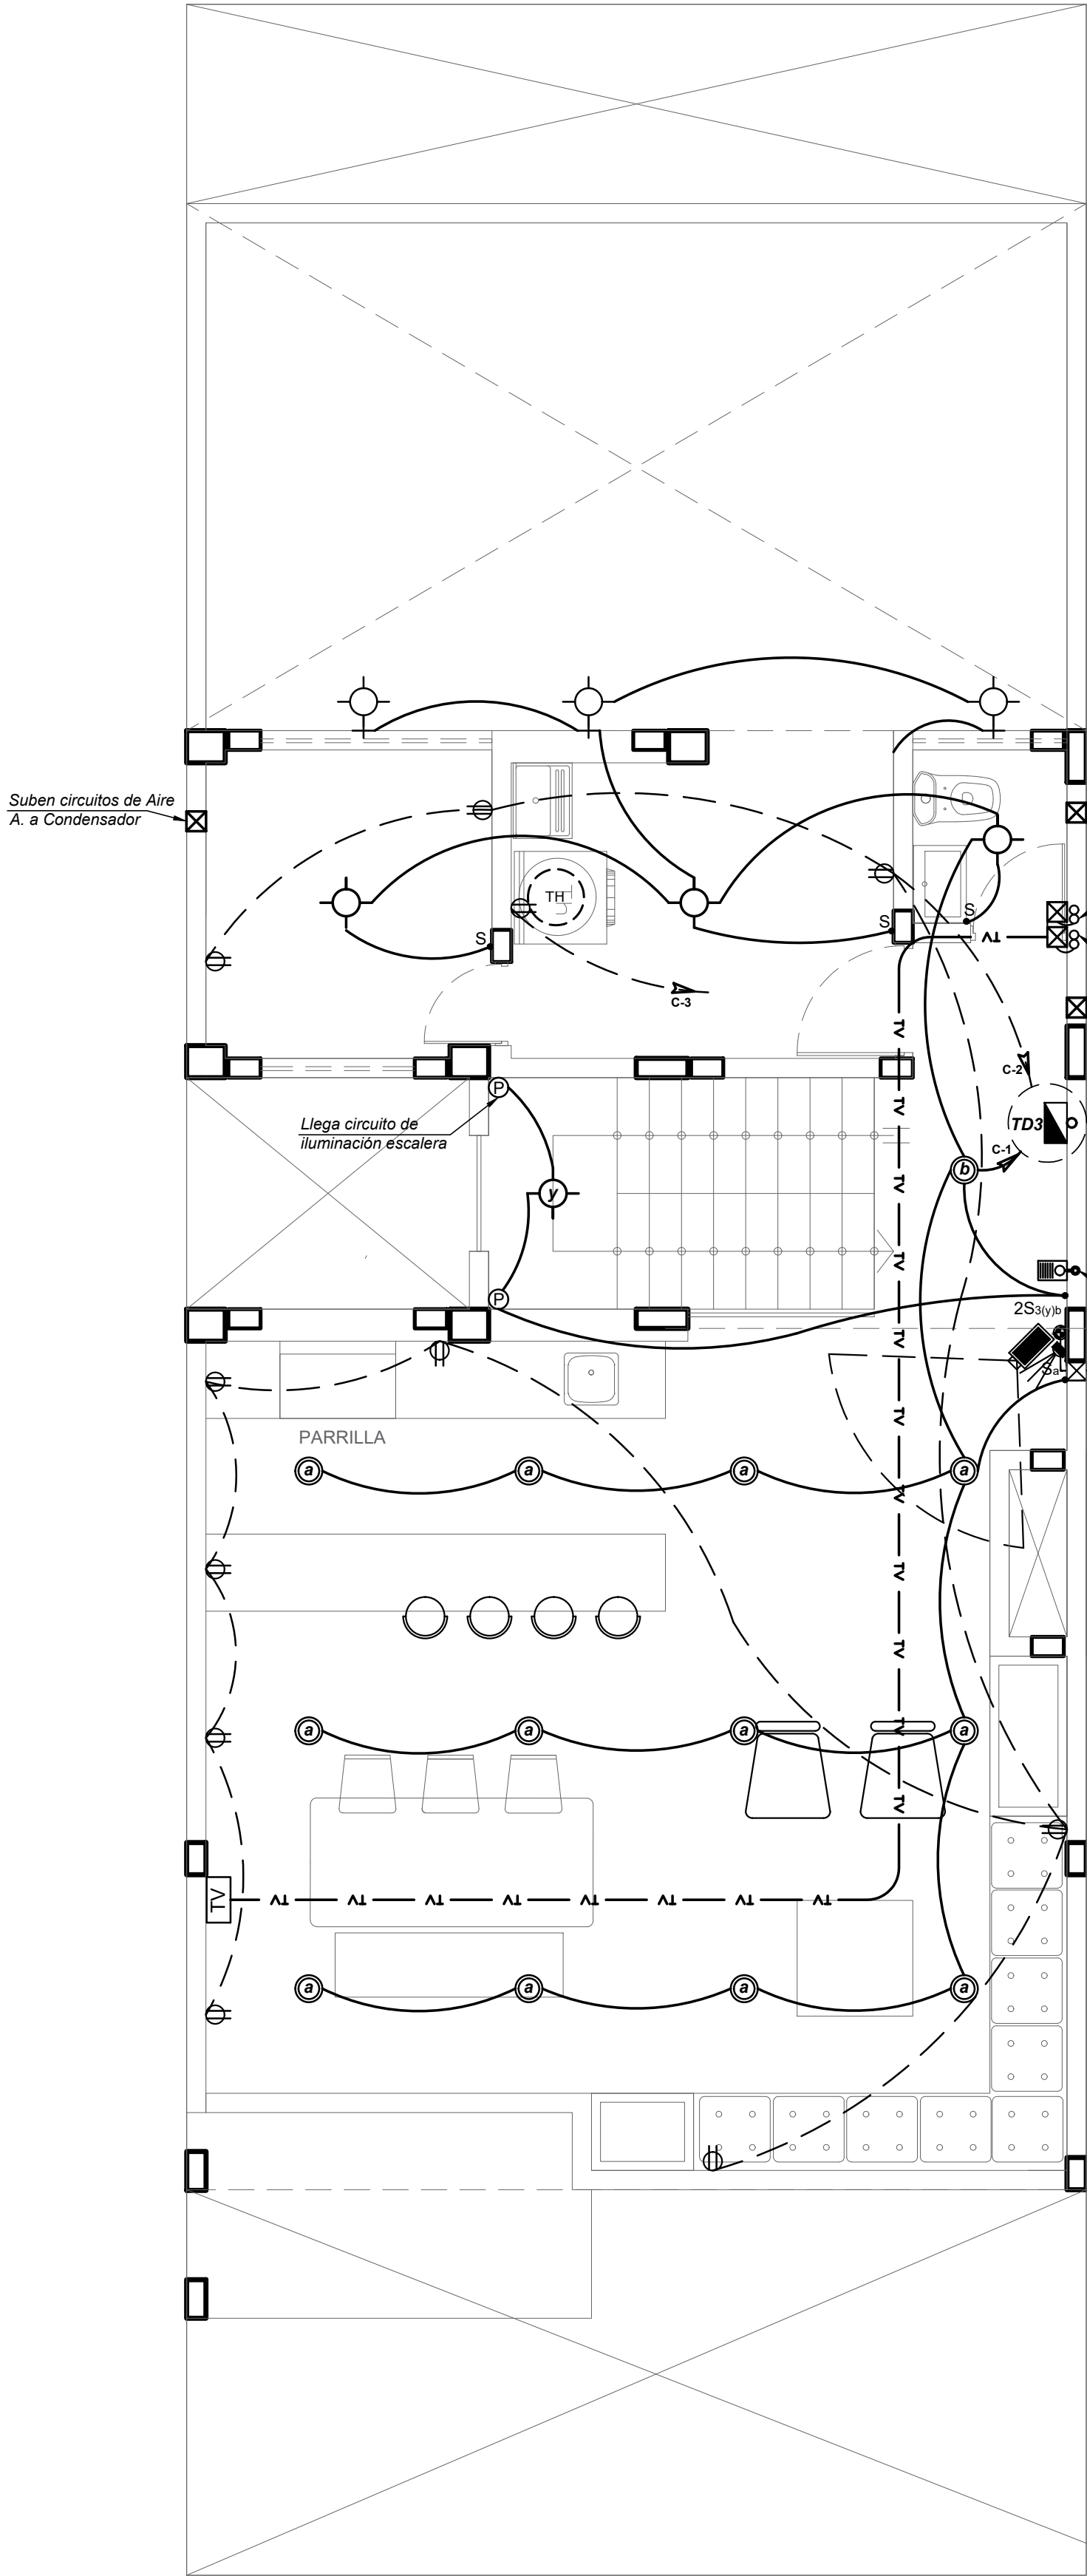



PLANTA AZOTEA
ESC:1/50

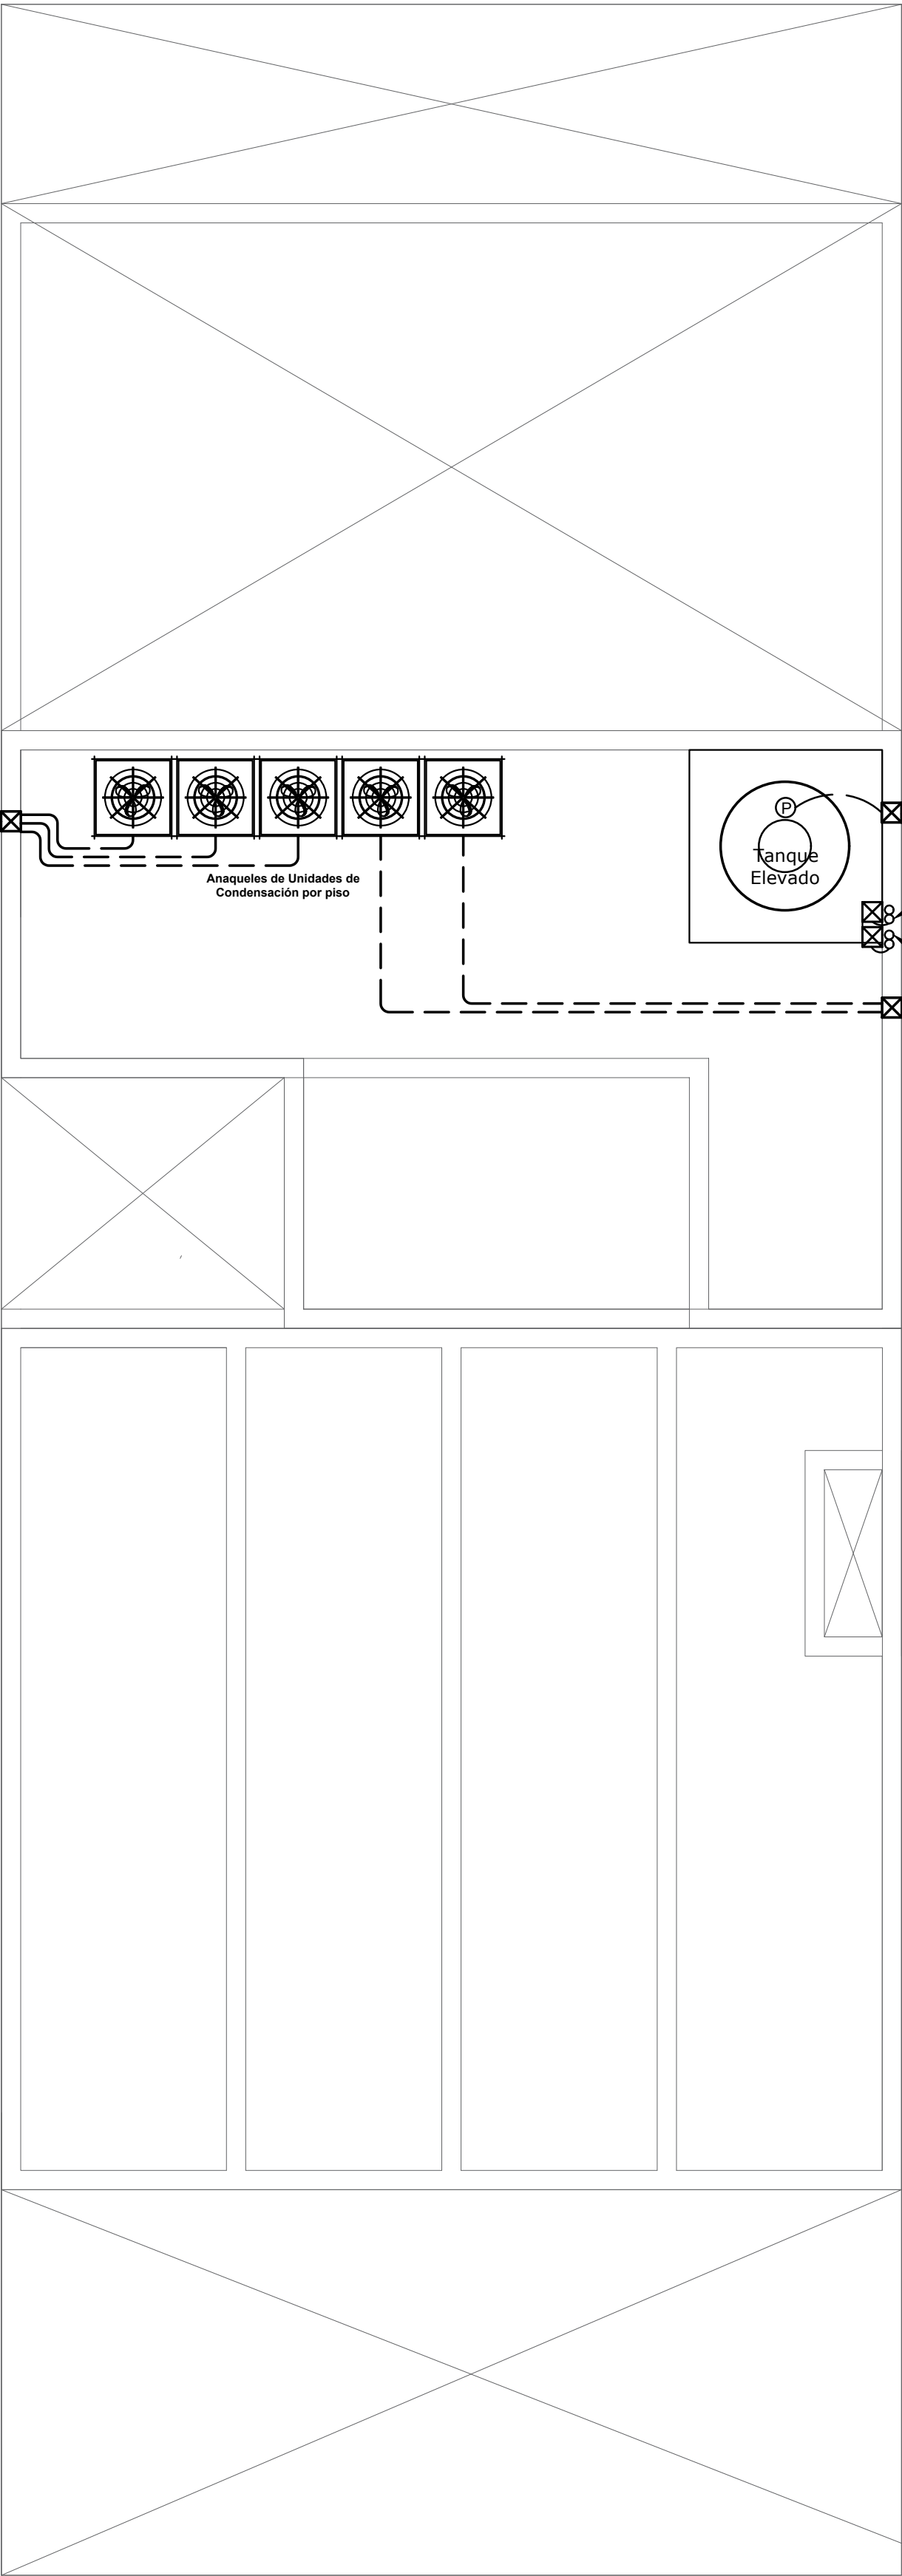

PLANTA TECHO
ESC:1/50

LEYENDA			
SÍMBOLO	DESCRIPCIÓN	CAJA	ALTURA
	SALIDA PARA ARTEFACTO DE TECHO	OCT. 100 x 55	CIELO RASO
	SALIDA PARA BRAQUETE DE PARED	OCT. 100 x 55	2.10
	SALIDA PARA DICROICO DE TECHO	OCT. 100 x 55	CIELO RASO
	SALIDA PARA DICROICO EN PISO	OCT. 100 x 55	0.00
	SALIDA PARA DICROICO EN PARED		2.40
	SALIDA PUNTO DE LUZ LED		
	TOMACORRIENTE BIPOLAR DOBLE, CON TIERRA, 10A 615A-220V	RECT. 100 x 50	0.40
	TOMACORRIENTE BIPOLAR DOBLE, CON TIERRA, 10A 615A-220V	RECT. 100 x 50	1.40
	TOMACORRIENTE BIPOLAR DOBLE, CON TIERRA, 10A 615A-220V	RECT. 100 x 50	1.80
	INTERRUPTOR UNIPOLAR, 5A-220V	RECT. 100 x 50	1.00
	INTERRUPTOR DOBLE, 5A-220V	RECT. 100 x 50	1.00
	INTERRUPTOR DE CONMUTACION 220V - 5A	ESPECIAL	1.00
	SALIDA PARA TELÉFONO E INTERNET (REPETIDORES)	RECT. 100 x 50	0.30
	CAJA DE PASE EN PISO O PARED	OCT. 100 x 55	0.40
	BOMBA DE AGUA		
	TABLERO DE DISTRIBUCIÓN	ESPECIAL	1.40
	CAJA PORTAMEDIDOR DE LUZ	TIPO LT 6 L	1.2
	SALIDA DE AUDIO - PARLANTES		
	SALIDA PARA TV-CABLE	RECT. 100 x 50	h=xxx
	SALIDA INTERCOMUNICADOR CON TRANSFORMADOR 220V/6V	RECT. 100 x 50	1.40
	POZO DE TIERRA		
	CIRCUITO EN CONDUCTO EMPOTRADO EN LA PARED O TECHO		
	CIRCUITO EN CONDUCTO EMPOTRADO EN EL PISO		
	CIRCUITO EN CONDUCTO EMPOTRADO TELEVISION		
	CIRCUITO EN CONDUCTO EMPOTRADO INTERCOMUNICADOR		
	CIRCUITO EN CONDUCTO EMPOTRADO TELÉFONO - INTERNET		


DETALLE DE CONEXION DE
TABLERO DE DISTRIBUCION

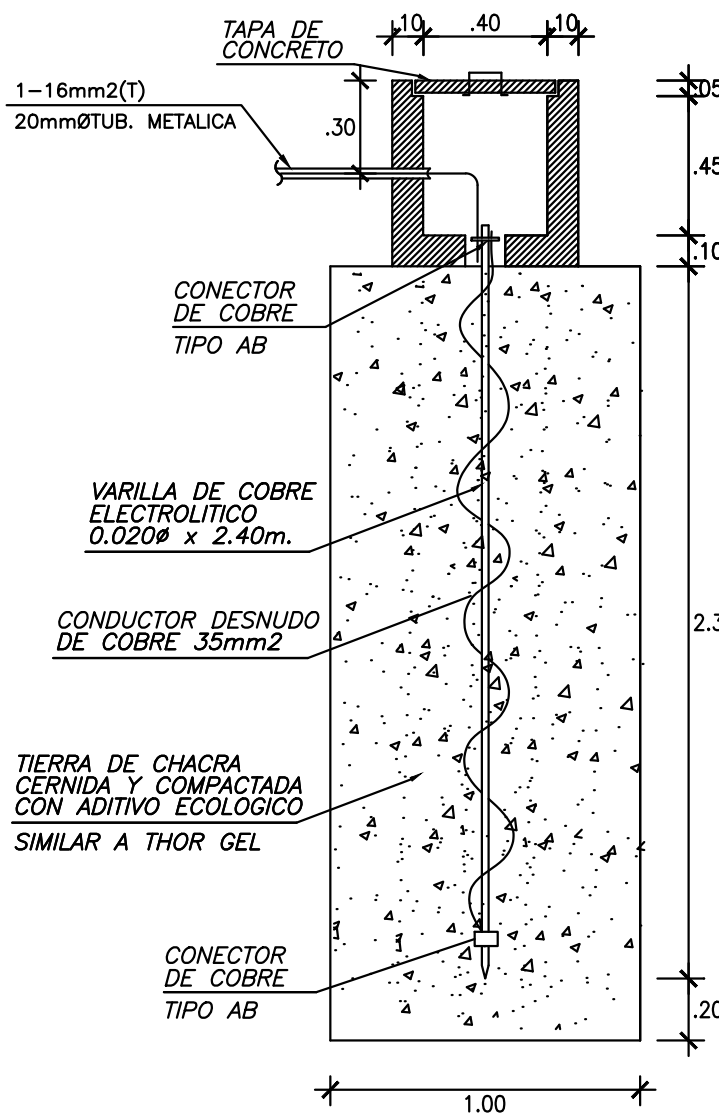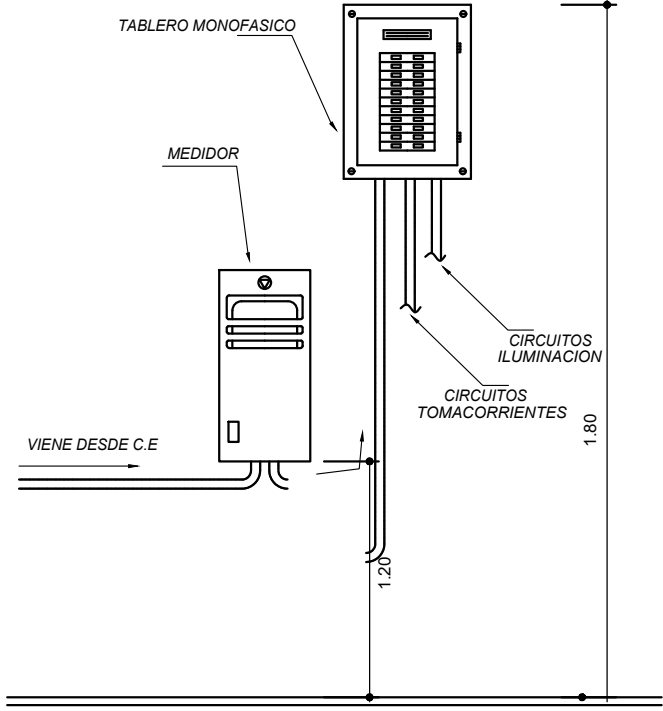

POZO DE TIERRA
RESISTENCIA <20 ohmios
Esc. = 1/25


NOTA:
EL CONTRATISTA INSTALARA
EL NUMERO DE POZOS
NECESARIOS PARA OBTENER
LA RESISTENCIA SOLICITADA

SIMBOLOGIA ALARMA Y CIRCUITO CERRADO	
	DESCRIPCION
	TUBERIA DE P.V.C. DE 1/4"
	VIDEO CAMARA GIRA 90°
	Grabadora DVR
	SENSOR DE MOVIMIENTO
	SUBE TUBERIA A CAMARA CCTV

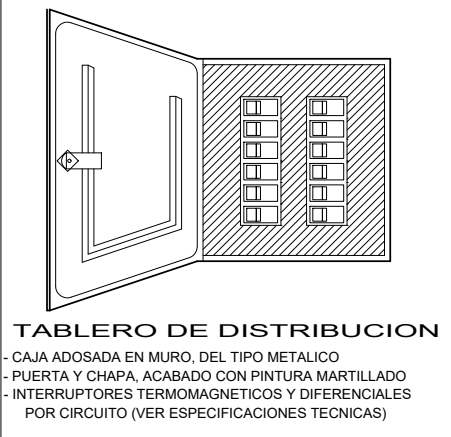

ESPECIFICACIONES TECNICAS


- Características del Sistema Monofásico 2 hilos 220 voltios 60 Hz.cos. Ø= 0.9
- El mínimo conductor THW y tubería PVC SAP a usar será de 2.5 mm - 15 mm Ø toda la tubería a empotrará en techo y/o piso será del tipo pesado (SAP) y la empotrada en pared del tipo liviana SEL
- Las cajas para interiores serán metálicas de características siguientes
Octogonales: Para salida de iluminación
Rectangulares: Para salida de interruptores, tomacorrientes, telef. interno tv. y pulsador.
Cuadradas: Para pase y/o empalme
- Los tomacorrientes monofásicos de baño serán del tipo con puesta a tierra y se conectarán junto con los tableros al pozo de tierra con conductor TW - 4 mm²
- Todos los equipos y materiales que se instalen a la intemperie serán del tipo a prueba de agua
- Los tableros serán de tipo metálico para empotrar
- Los conductores para comunicaciones no deberán instalarse a menos de 5 cm de alumbrado y/o fuerza.

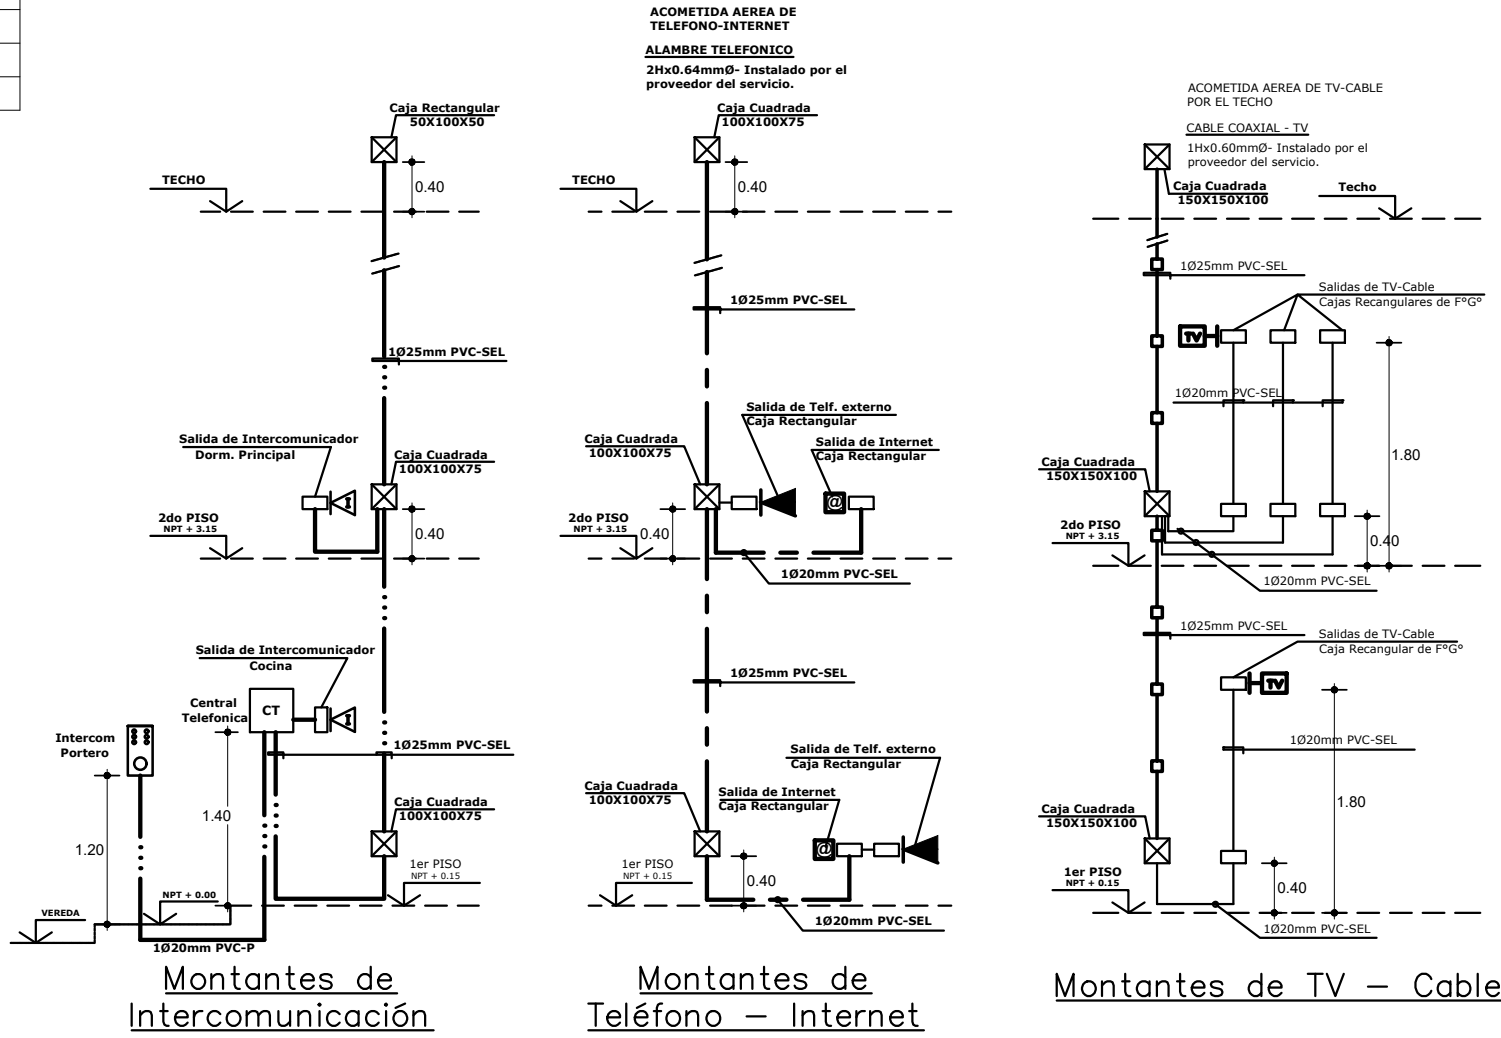


Montantes de
Intercomunicación

Montantes de
Teléfono - Internet

Montantes de TV - Cable

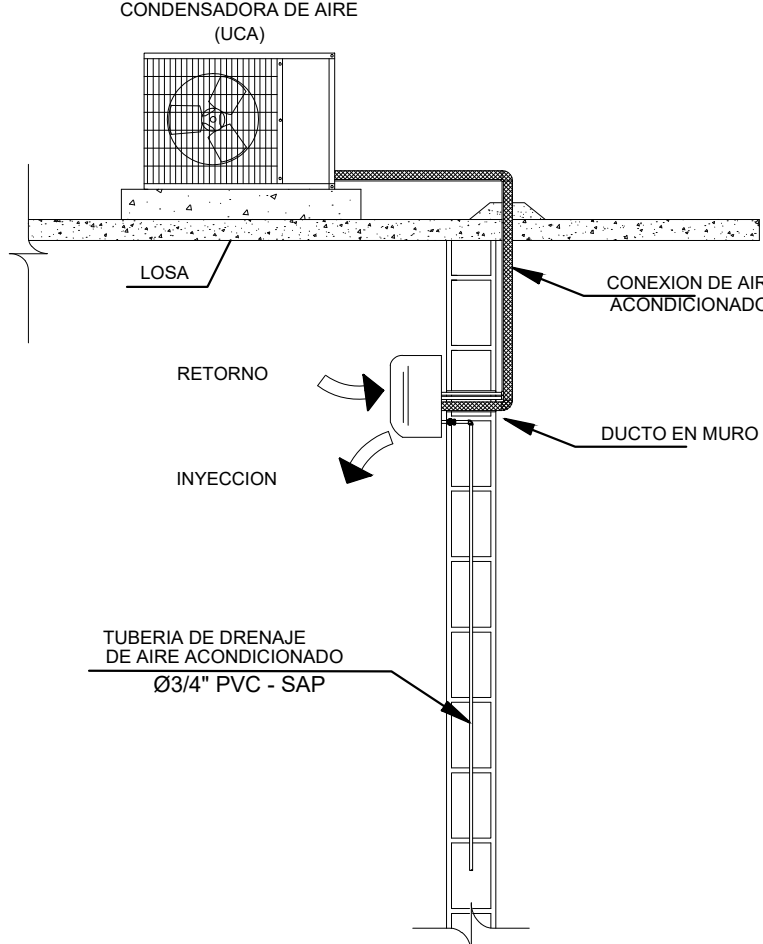

DETALLE - 01
INSTALACION TIPO DE UNIDAD EN MURO

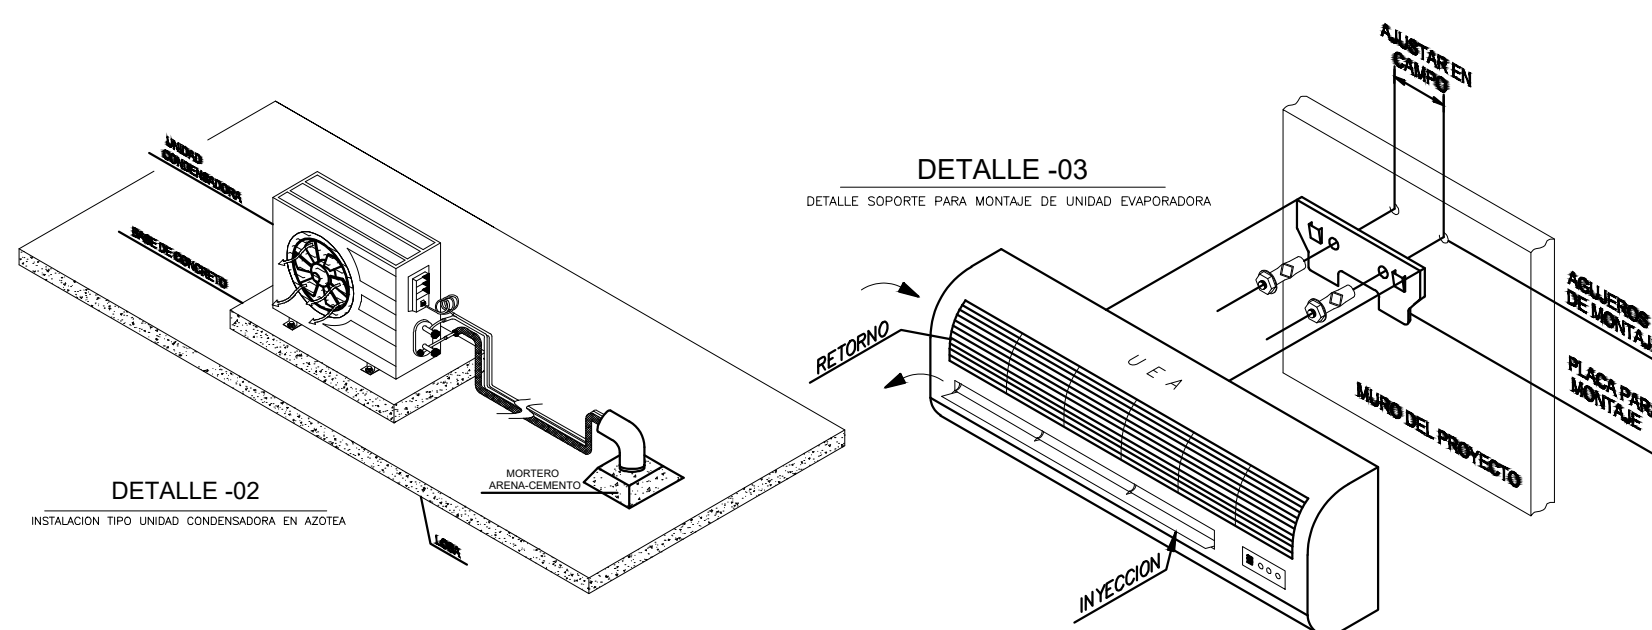

DETALLE - 02
INSTALACION TIPO UNIDAD CONDENSADORA EN AZOTEA

DETALLE - 03
DETALLE SOPORTE PARA MONTAJE DE UNIDAD EVAPORADORA

SIMBOLOGIA

- UNIDAD EVAPORADORA
- UNIDAD CONDENSADORA EN AZOTEA

NOMENCLATURA

- Ø INDICA DIÁMETRO
- UEA UNIDAD EVAPORADORA DE AIRE
- UCA UNIDAD CONDESADORA DE AIRE.

PROYECTO: VIVIENDA UNIFAMILIAR	UBICACIÓN :	DIBUJO : JLAY
	URB. MIRAFLORES BOULEVARD PARK PLAZA Mz. AN - Lote 18 - II ETAPA - CASTILLA	RESPONSABLE : ARQ. RENZO IZQUIERDO
	PROPIETARIO:	ESCALA : 1 / 50
	Sra. ROSSEMERY YANIRE FERNÁNDEZ ROJAS DNI: 80366589	FECHA : JULIO 2026

TITULO DE LÁMINA: INSTALACIONES ELÉCTRICAS CIRCUITOS ELÉCTRICOS - AZOTEA Y TECHO
--

N° LÁMINA: IE-02
